


OLLYWOOD



LEMONICA KIOSK DETAIL

01633 547 979 | info@ollywoodservices.co.uk


Unit 19B Springvale Industrial Estate, Cwmbran, South Wales NP44 5BA

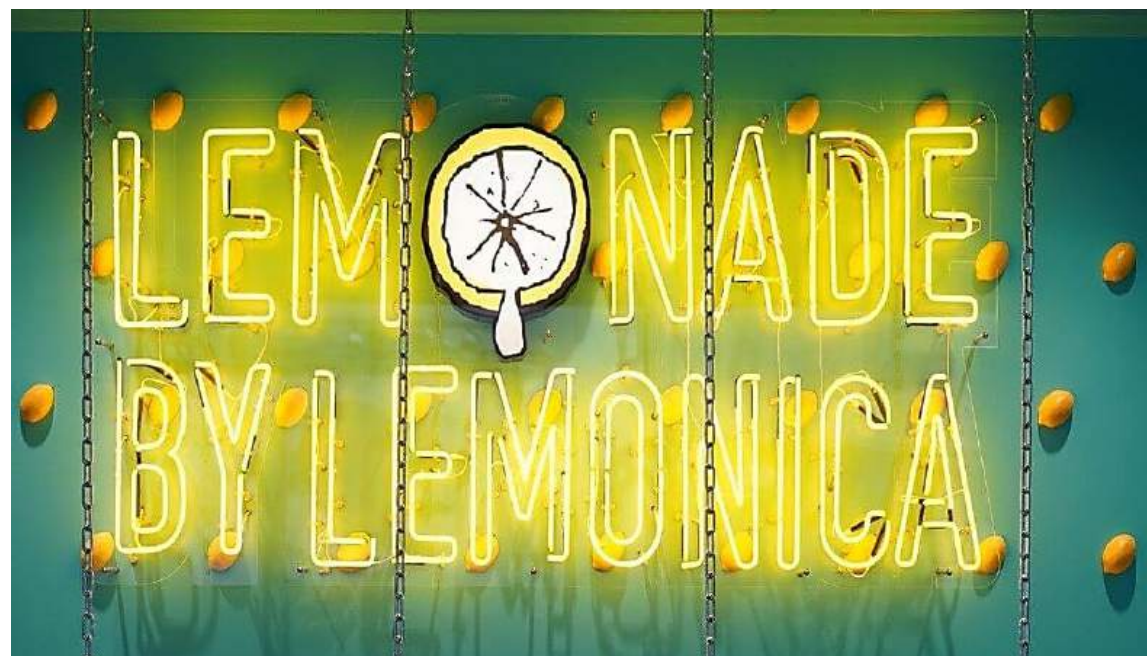


OLLYWOOD

EXISTING LOCATIONS

PROJECT : LEMONICA KIOSK DETAIL

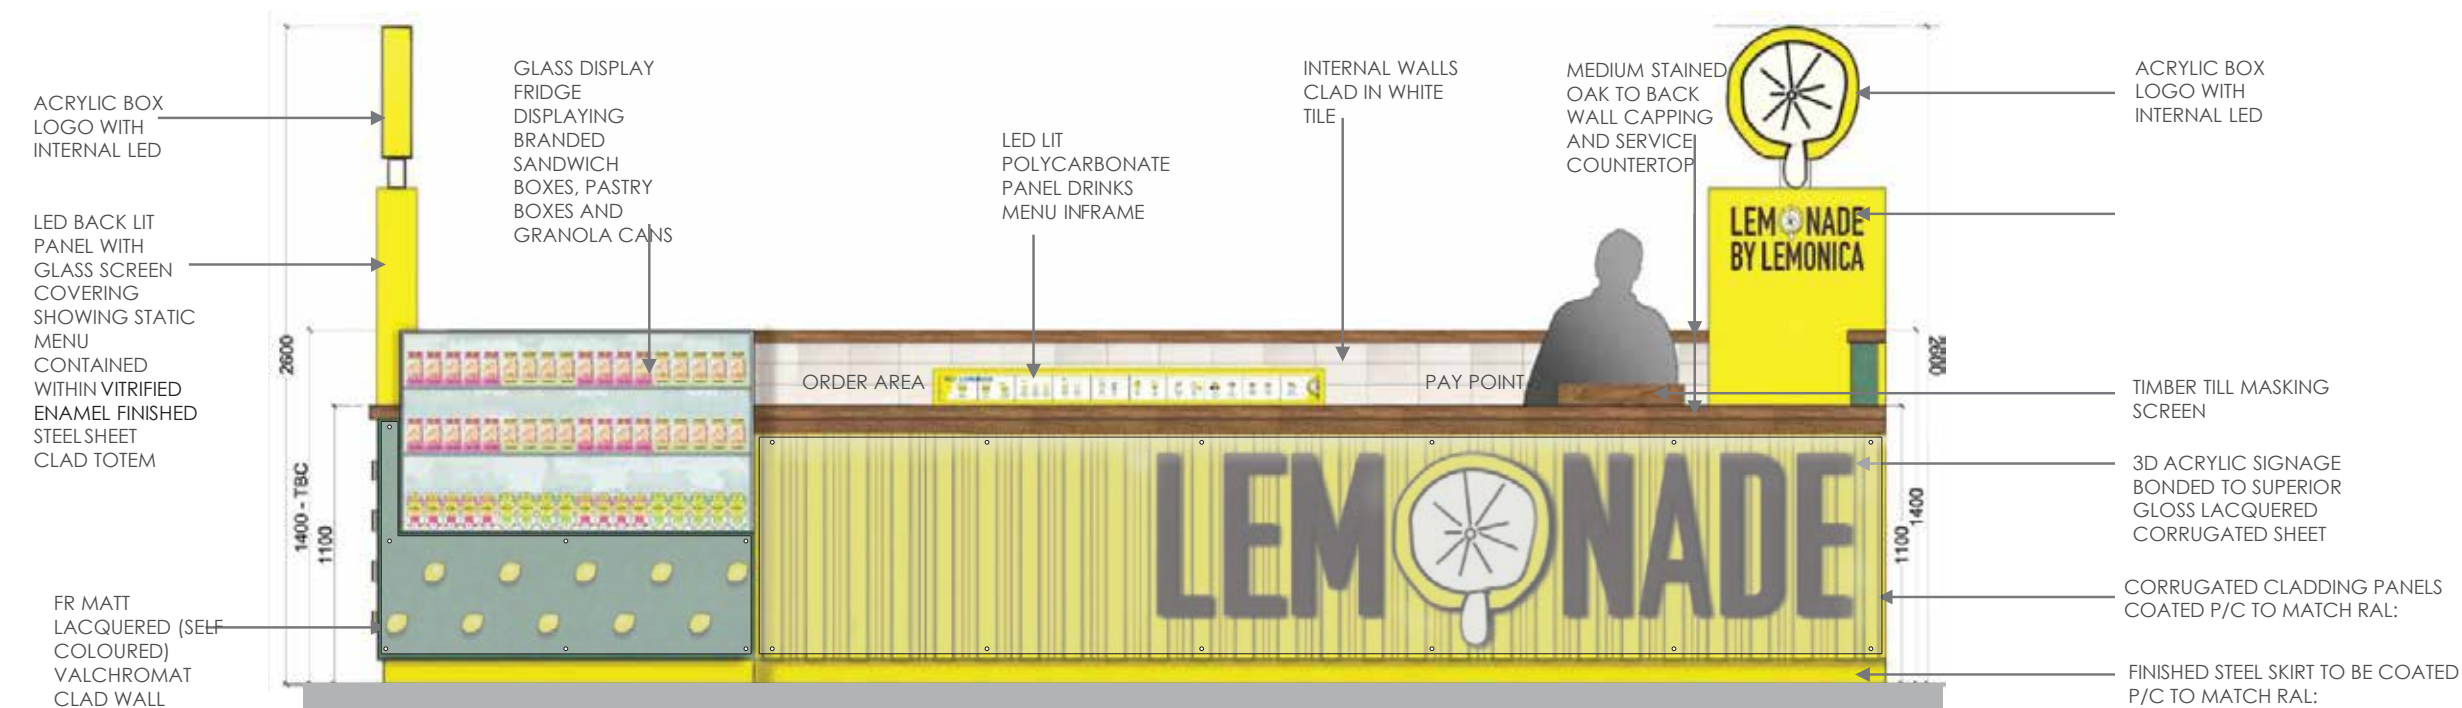

ELEVATION AA

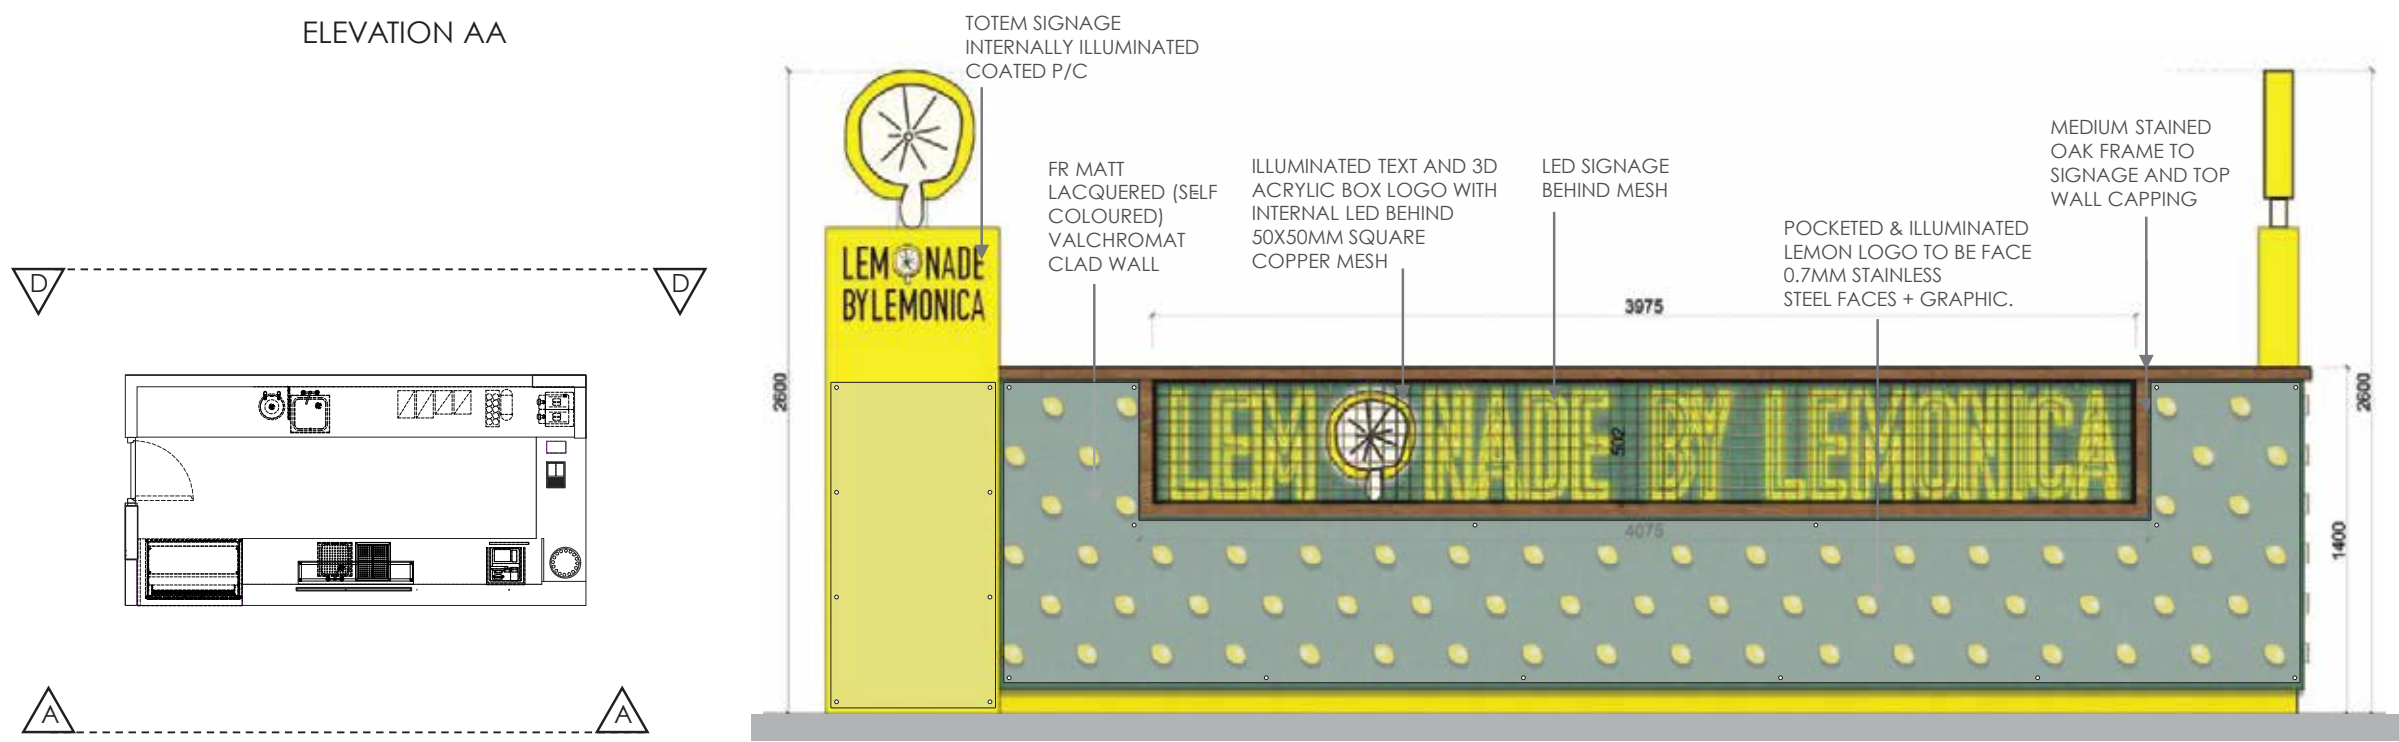

ELEVATION DD

OLLYWOOD

01633 547 979 | info@ollywoodservices.co.uk
Unit 19B Springvale Industrial Estate, Cwmbran, South Wales NP44 5BA

NOTES:

- 1 UNLESS OTHERWISE SPECIFIED DIMENSIONS ARE IN MILLIMETERS.
- 2 ALL INSIDE BEND RADII TO BE MINIMUM.
- 3 REMOVE ALL BURS AND SHARP EDGES.
- 4 PART TO BE MANUFACTURED FROM SEPARATE SUPPLIED CAD FILE.
- 5 DRAWING IS FOR REFERENCE ONLY, ACTUAL DRAWINGS SUPPLIED FROM 3D ELECTRONIC DATABASE.
- 6 DO NOT SCALE DRAWING.

THIS DRAWING IS THE PROPERTY OF OLLYWOOD SERVICES AND IS PROTECTED.
IT MAY NOT BE DISTRIBUTED OR USED IN ANY FORM WITHOUT WRITTEN PERMISSION.

CLIENT : LEMONICA

PROJECT : LEMONICA WESTFIELD KIOSK DETAIL

JOB NO :	NAME	SIGNATURE	DATE
DRAWN BY :	JR		17/04/2024

CHECKED BY :

DRAWING TITLE :

SUMMARY :

DRAWING NO : REVISION A MATERIAL :


PROCESS : FINISH :





SCALE :

PAGE SIZE :

A3

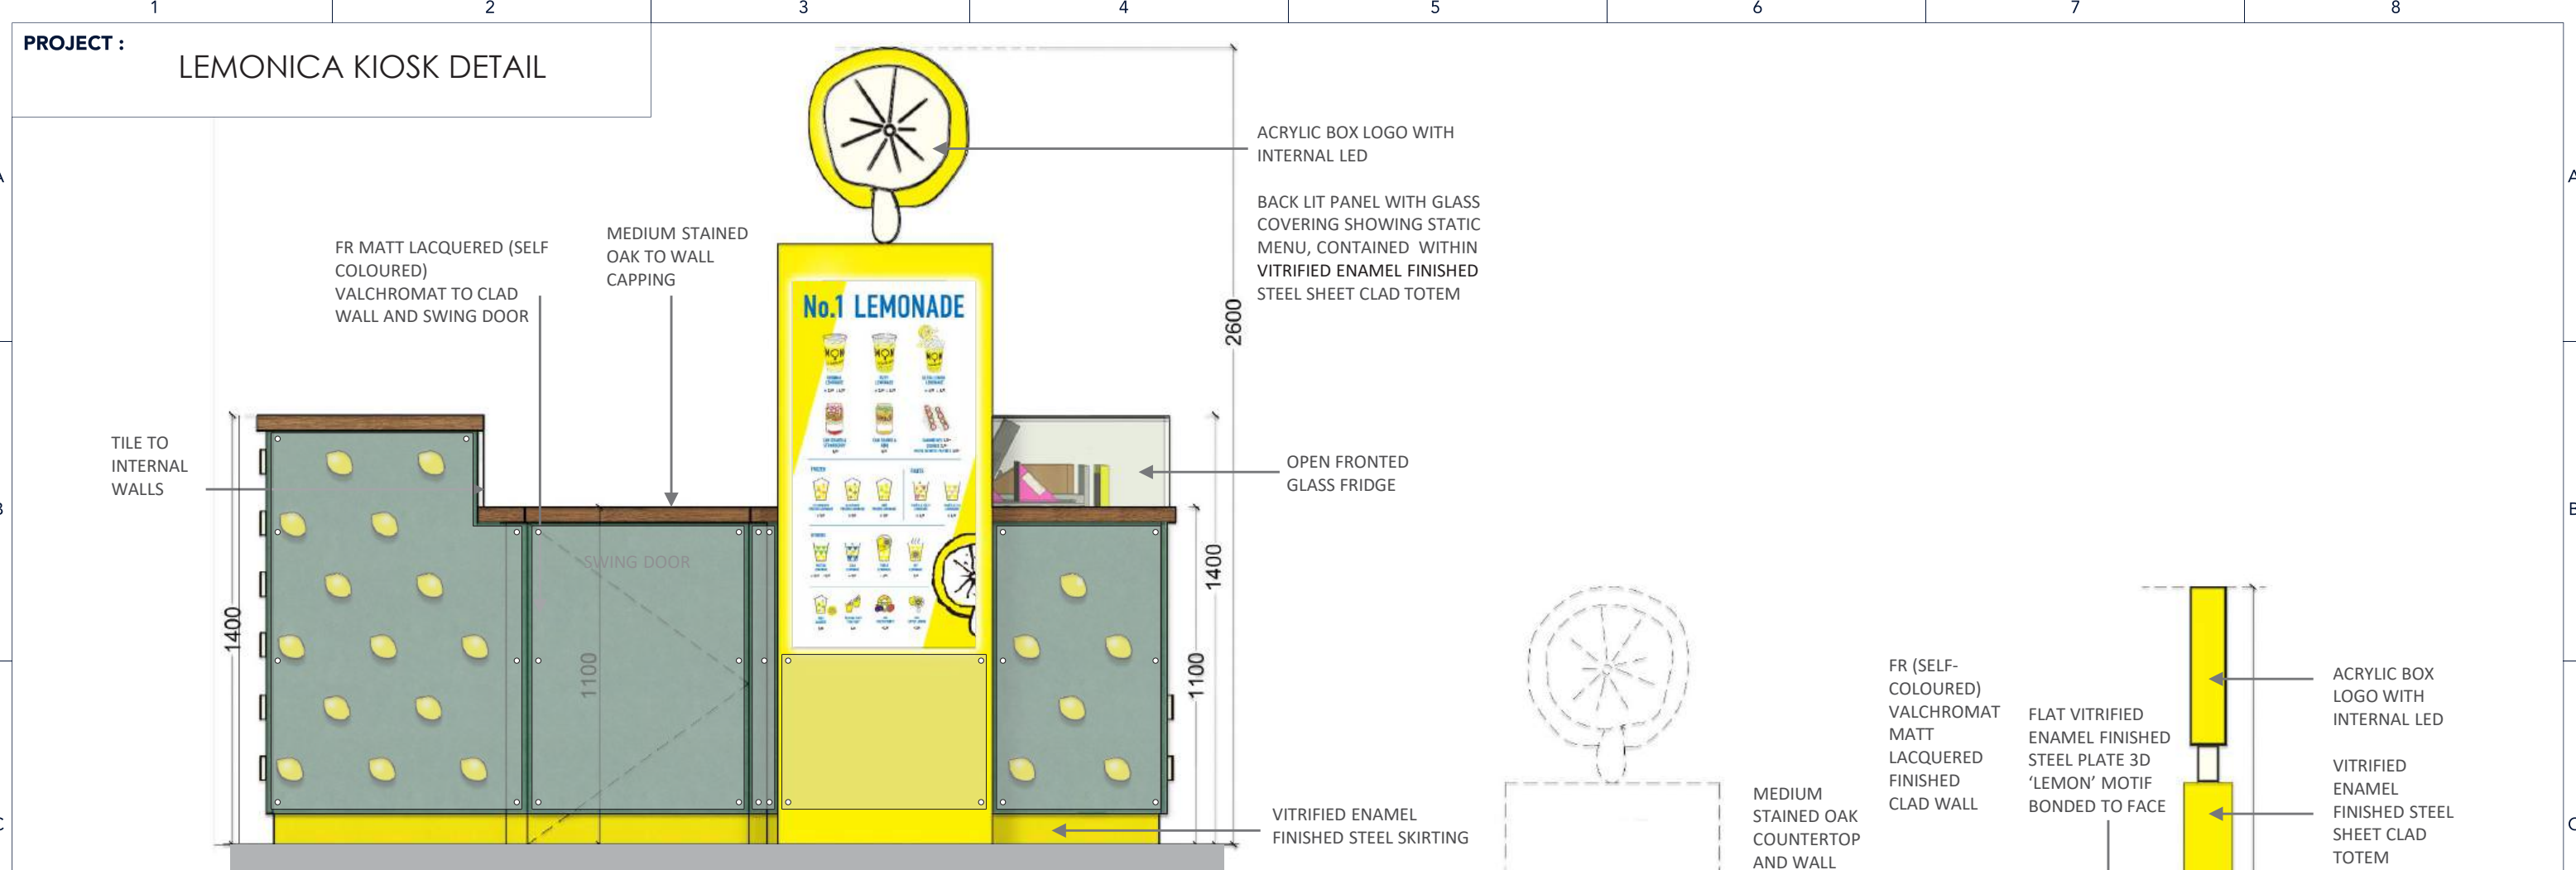

ELEVATION BB

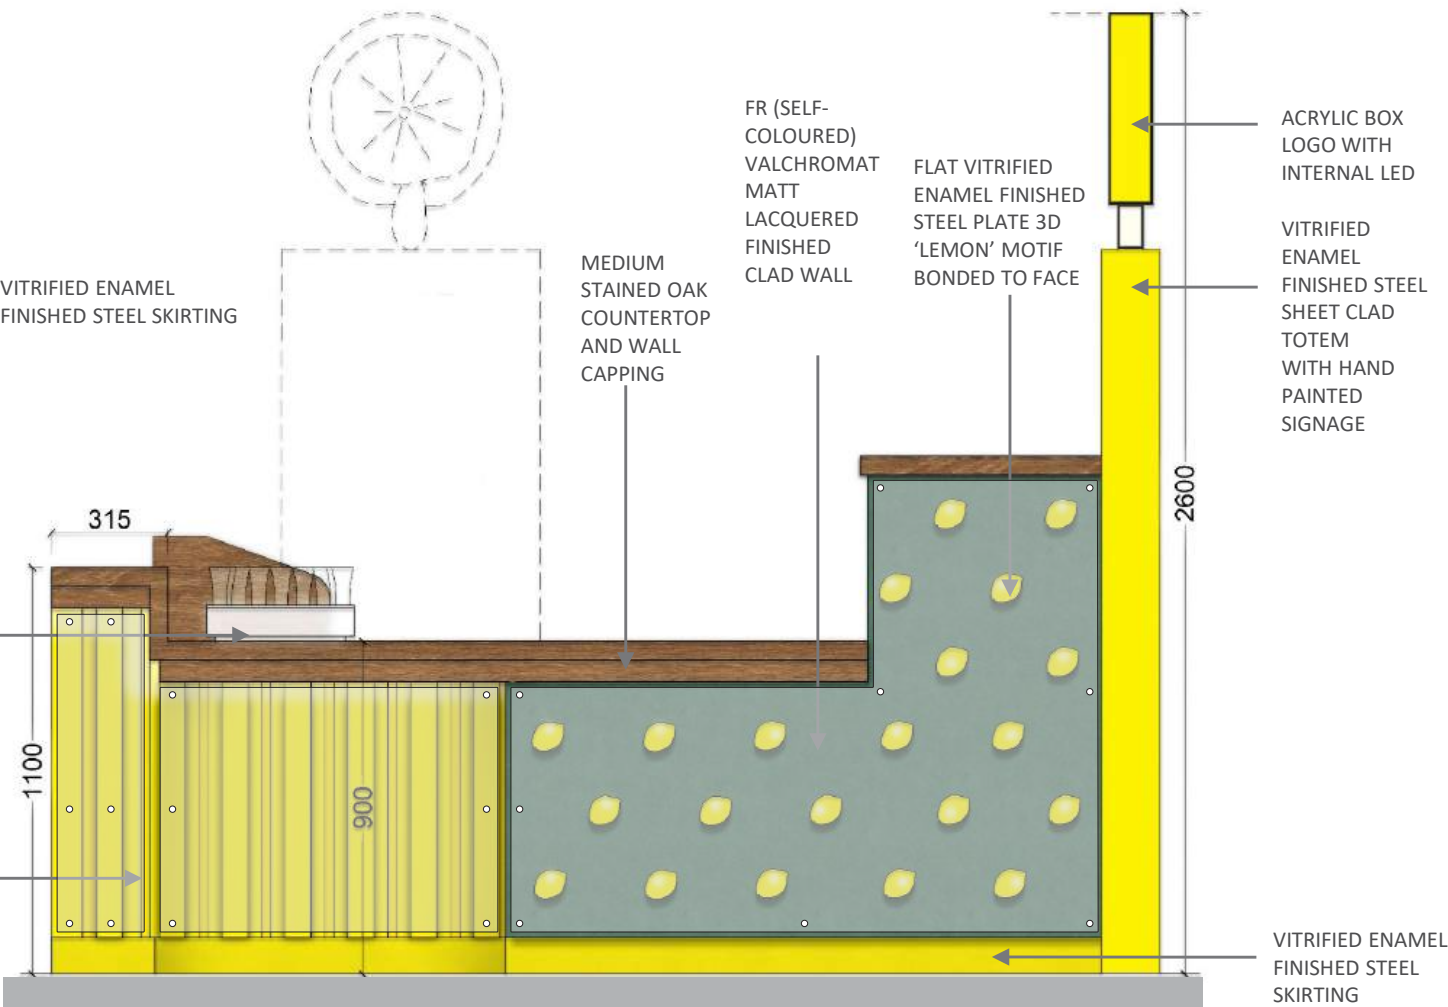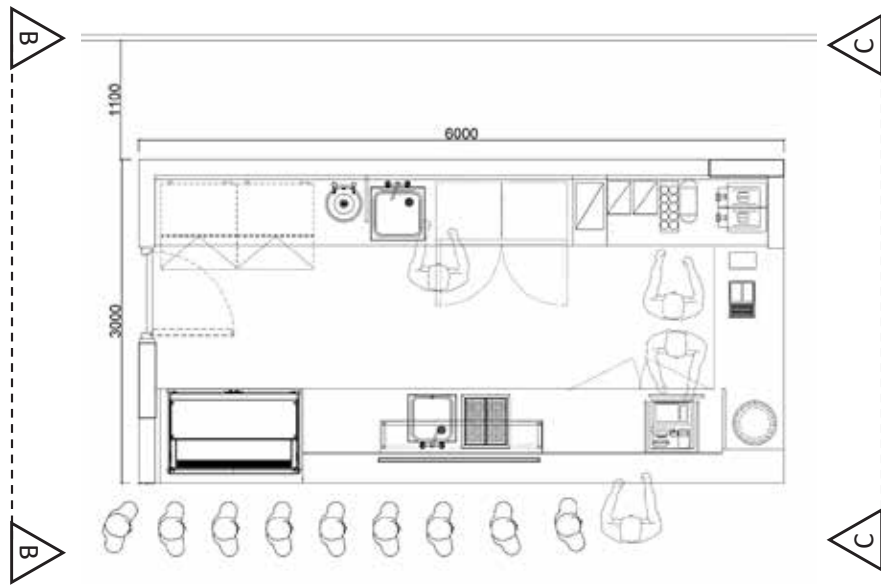

ELEVATION CC

NOTES:

- 1 UNLESS OTHERWISE SPECIFIED DIMENSIONS ARE IN MILLIMETERS.
- 2 ALL INSIDE BEND RADII TO BE MINIMUM.
- 3 REMOVE ALL BURS AND SHARP EDGES.
- 4 PART TO BE MANUFACTURED FROM SEPARATE SUPPLIED CAD FILE.
- 5 DRAWING IS FOR REFERENCE ONLY, ACTUAL DRAWINGS SUPPLIED FROM 3D ELECTRONIC DATABASE.
- 6 DO NOT SCALE DRAWING.

THIS DRAWING IS THE PROPERTY OF OLLYWOOD SERVICES AND IS PROTECTED. IT MAY NOT BE DISTRIBUTED OR USED IN ANY FORM WITHOUT WRITTEN PERMISSION.

CLIENT : LEMONICA				DRAWING TITLE :			
PROJECT : LEMONICA WESTFIELD KIOSK DETAIL				SUMMARY :			
JOB NO :	NAME	SIGNATURE	DATE	DRAWING NO :	REVISION A	MATERIAL :	
DRAWN BY :	JR		17/04/2024	PROCESS :		FINISH :	
CHECKED BY :				SCALE :		PAGE SIZE : A3	

OLLYWOOD

01633 547 979 | info@ollywoodservices.co.uk
Unit 19B Springvale Industrial Estate, Cwmbran, South Wales NP44 5BA

PROJECT : LEMONICA KIOSK DETAIL



ACRYLIC BOX LOGO WITH INTERNAL LED

MEDIUM OAK TO COUNTERTOP AND WALL CAPPING

LED BACK LIT PANEL WITH GLASS COVERING SHOWING STATIC MENU, CONTAINED WITHIN VITRIFIED ENAMEL FINISHED STEEL SHEET CLAD TOTEM

FLAT VITRIFIED ENAMEL FINISHED STEEL PLATE 3D 'LEMON' MOTIF BONDED TO FACE

VITRIFIED ENAMEL FINISHED STEEL SKIRTING

FR MATT LACQUERED (SELF COLOURED) VALCHROMAT TO CLAD WALL AND SWING DOOR

GLASS OPEN FRONTED FRIDGE DISPLAYING SANDWICH BOXES, PASTRY BOXES AND GRANOLA CANS

S/S BACK COUNTER TILE TO INTERNAL RETURNS ABOVE S/S COUNTERS

ACRYLIC BOX LOGO WITH INTERNAL LED ILLUMINATION

VITRIFIED ENAMEL FINISHED SHEET CLAD TOTEM WITH HAND PAINTED SIGNAGE

PAY POINT

MEDIUM OAK SCREEN TO MASK TILL

150MMH ILLUMINATED POLYCARBONATE PANEL DRINKS MENU

FINISHED BOX PROFILE CORRUGATED SHEET, ILLUMINATED FROM ABOVE AND BELOW BY CONCEALED LED STRIPS 3D ACRYLIC SIGNAGE FIXED TO FASCIA

NOTES:

- 1 UNLESS OTHERWISE SPECIFIED DIMENSIONS ARE IN MILLIMETERS.
- 2 ALL INSIDE BEND RADII TO BE MINIMUM.
- 3 REMOVE ALL BURS AND SHARP EDGES.
- 4 PART TO BE MANUFACTURED FROM SEPARATE SUPPLIED CAD FILE.
- 5 DRAWING IS FOR REFERENCE ONLY, ACTUAL DRAWINGS SUPPLIED FROM 3D ELECTRONIC DATABASE.
- 6 DO NOT SCALE DRAWING.

THIS DRAWING IS THE PROPERTY OF OLLYWOOD SERVICES AND IS PROTECTED. IT MAY NOT BE DISTRIBUTED OR USED IN ANY FORM WITHOUT WRITTEN PERMISSION.

CLIENT : LEMONICA

PROJECT : LEMONICA WESTFIELD KIOSK DETAIL

JOB NO :	NAME	SIGNATURE	DATE
DRAWN BY :	JR		17/04/2024

CHECKED BY :

DRAWING TITLE :

SUMMARY :

DRAWING NO : REVISION MATERIAL :

PROCESS : FINISH :




SCALE :

PAGE SIZE :


A3

OLLYWOOD

01633 547 979 | info@ollywoodservices.co.uk
Unit 19B Springvale Industrial Estate, Cwmbran, South Wales NP44 5BA

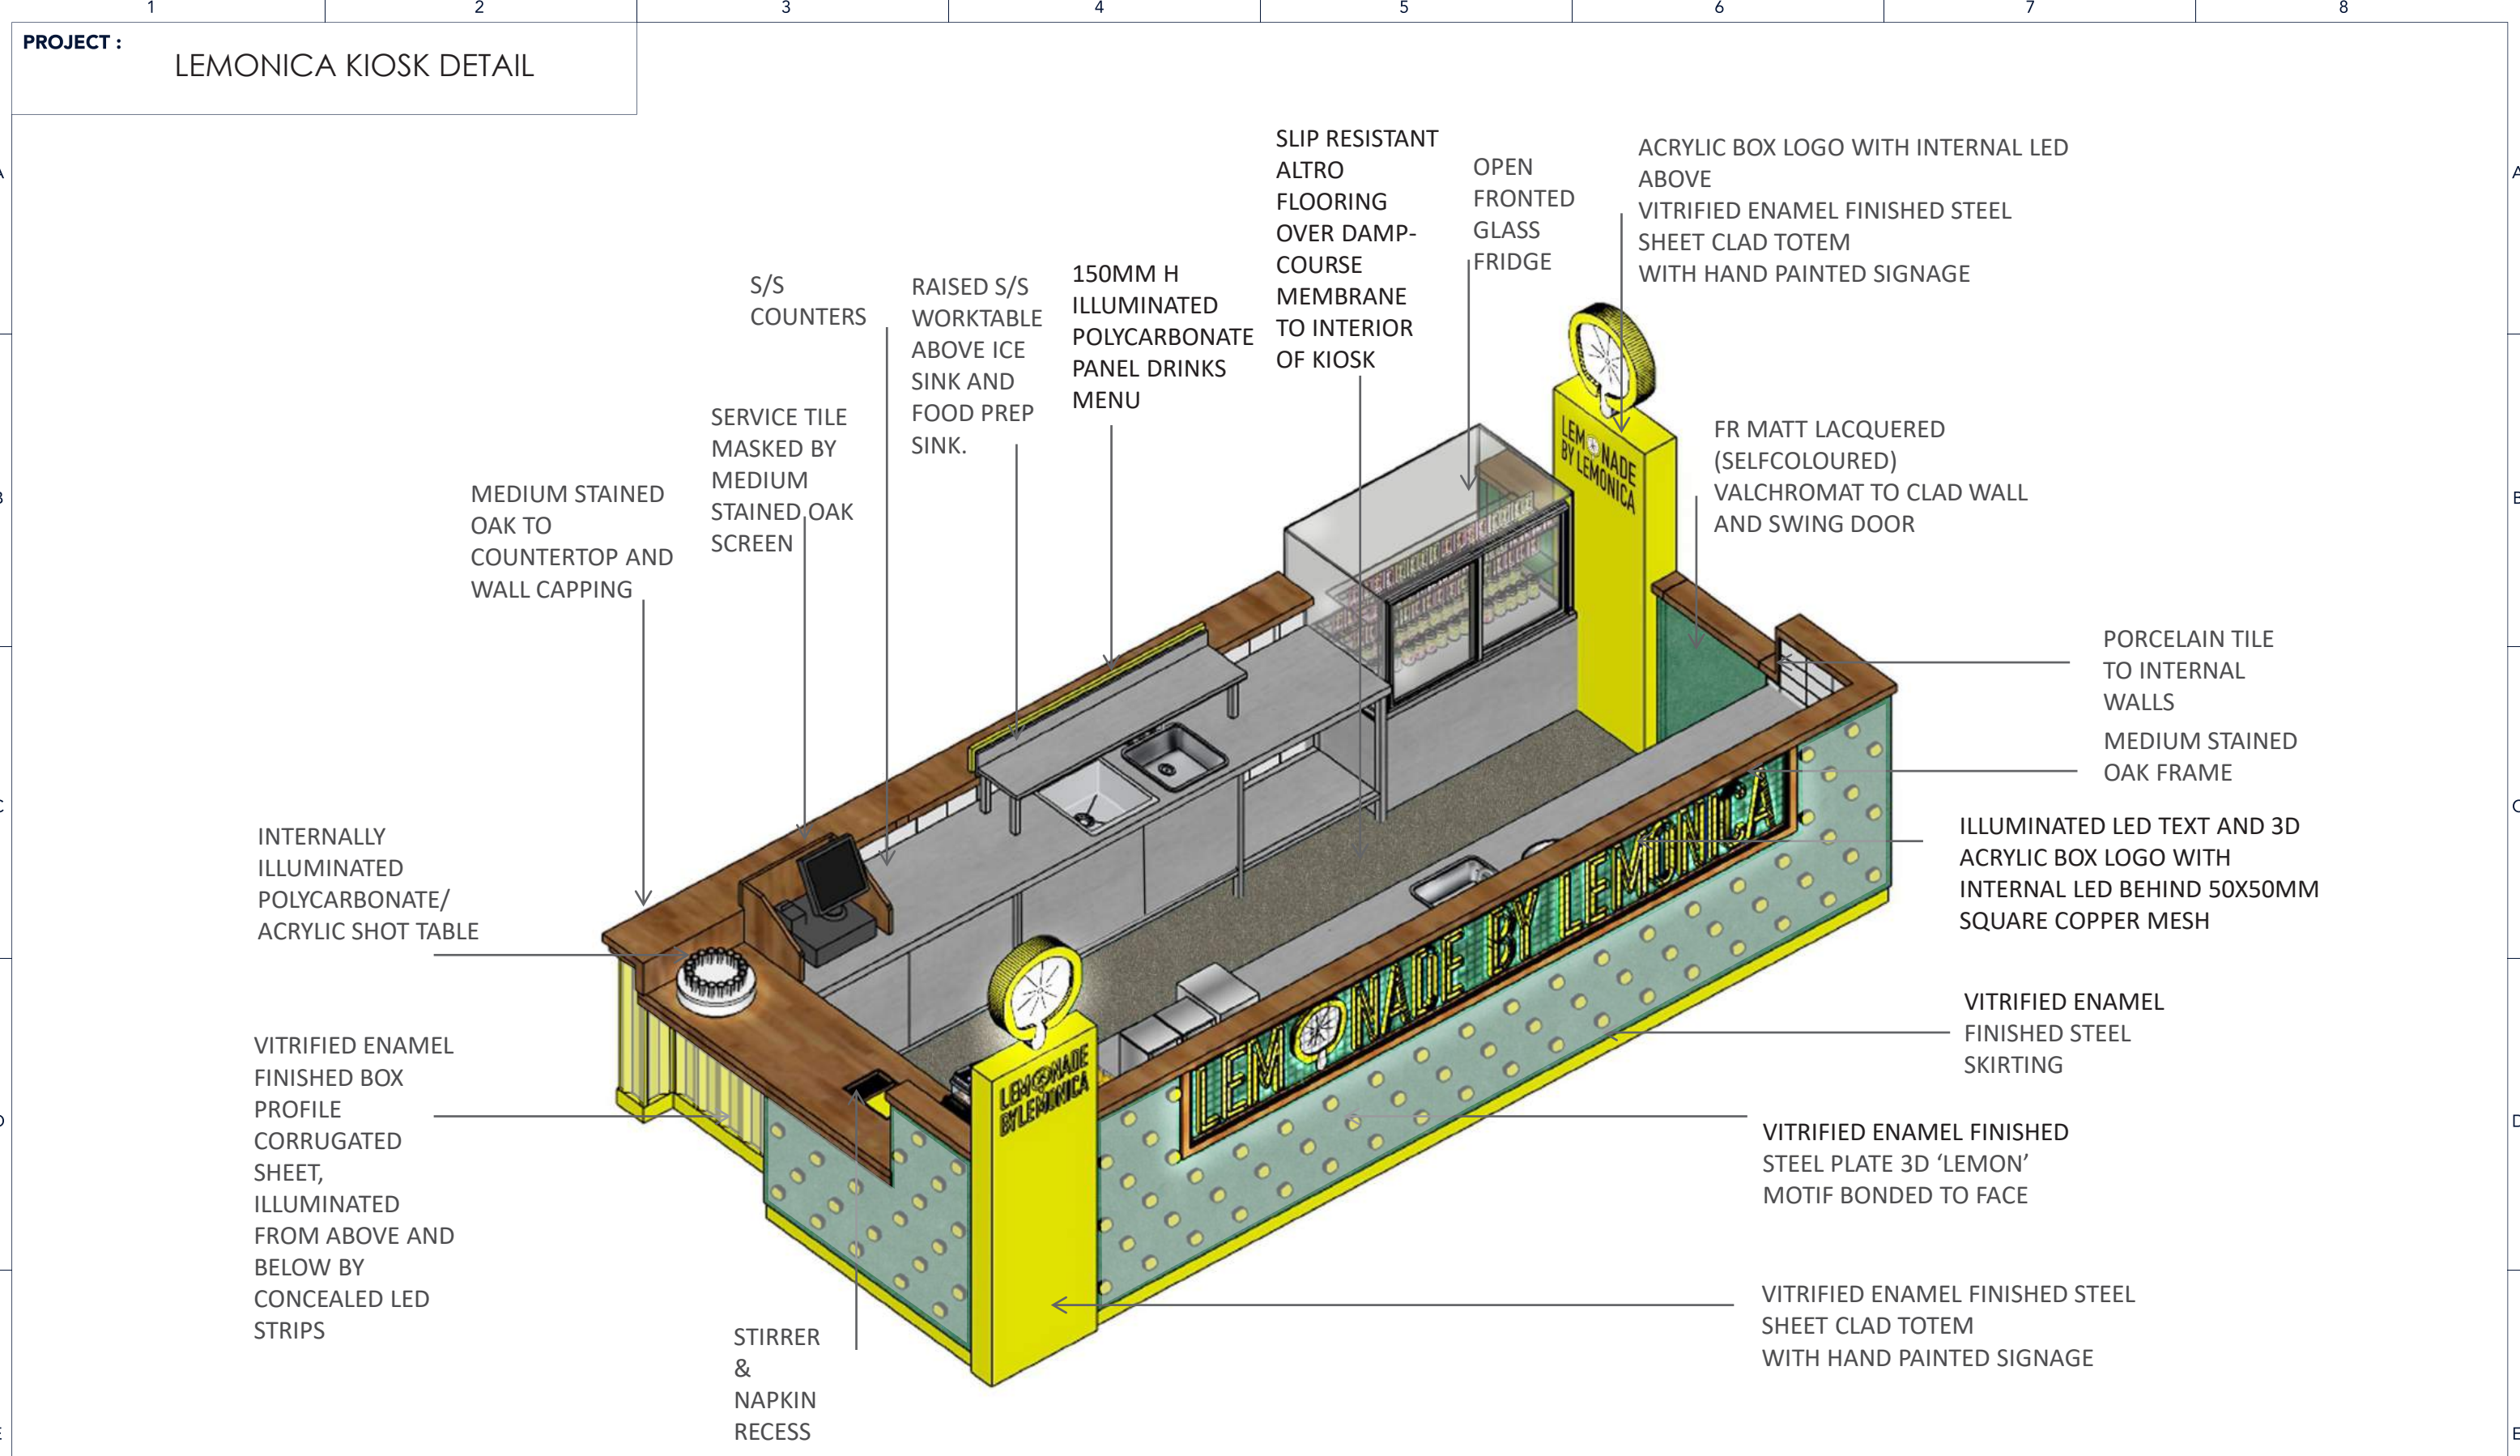

OLLYWOOD 01633 547 979 info@ollywoodservices.co.uk Unit 19B Springvale Industrial Estate, Cwmbran, South Wales NP44 5BA				NOTES: 1 UNLESS OTHERWISE SPECIFIED DIMENSIONS ARE IN MILLIMETERS. 2 ALL INSIDE BEND RADII TO BE MINIMUM. 3 REMOVE ALL BURS AND SHARP EDGES. 4 PART TO BE MANUFACTURED FROM SEPARATE SUPPLIED CAD FILE. 5 DRAWING IS FOR REFERENCE ONLY, ACTUAL DRAWINGS SUPPLIED FROM 3D ELECTRONIC DATABASE. 6 DO NOT SCALE DRAWING.				CLIENT : LEMONICA				DRAWING TITLE :					
								PROJECT : LEMONICA WESTFIELD KIOSK DETAIL				SUMMARY :					
				JOB NO :		NAME		SIGNATURE		DATE		DRAWING NO :		REVISION A	MATERIAL :		
				DRAWN BY :		JR				17/04/2024		PROCESS :			FINISH :		
				THIS DRAWING IS THE PROPERTY OF OLLYWOOD SERVICES AND IS PROTECTED. IT MAY NOT BE DISTRIBUTED OR USED IN ANY FORM WITHOUT WRITTEN PERMISSION.				CHECKED BY :							SCALE :		
1		2		3		4		5		6		7		8			

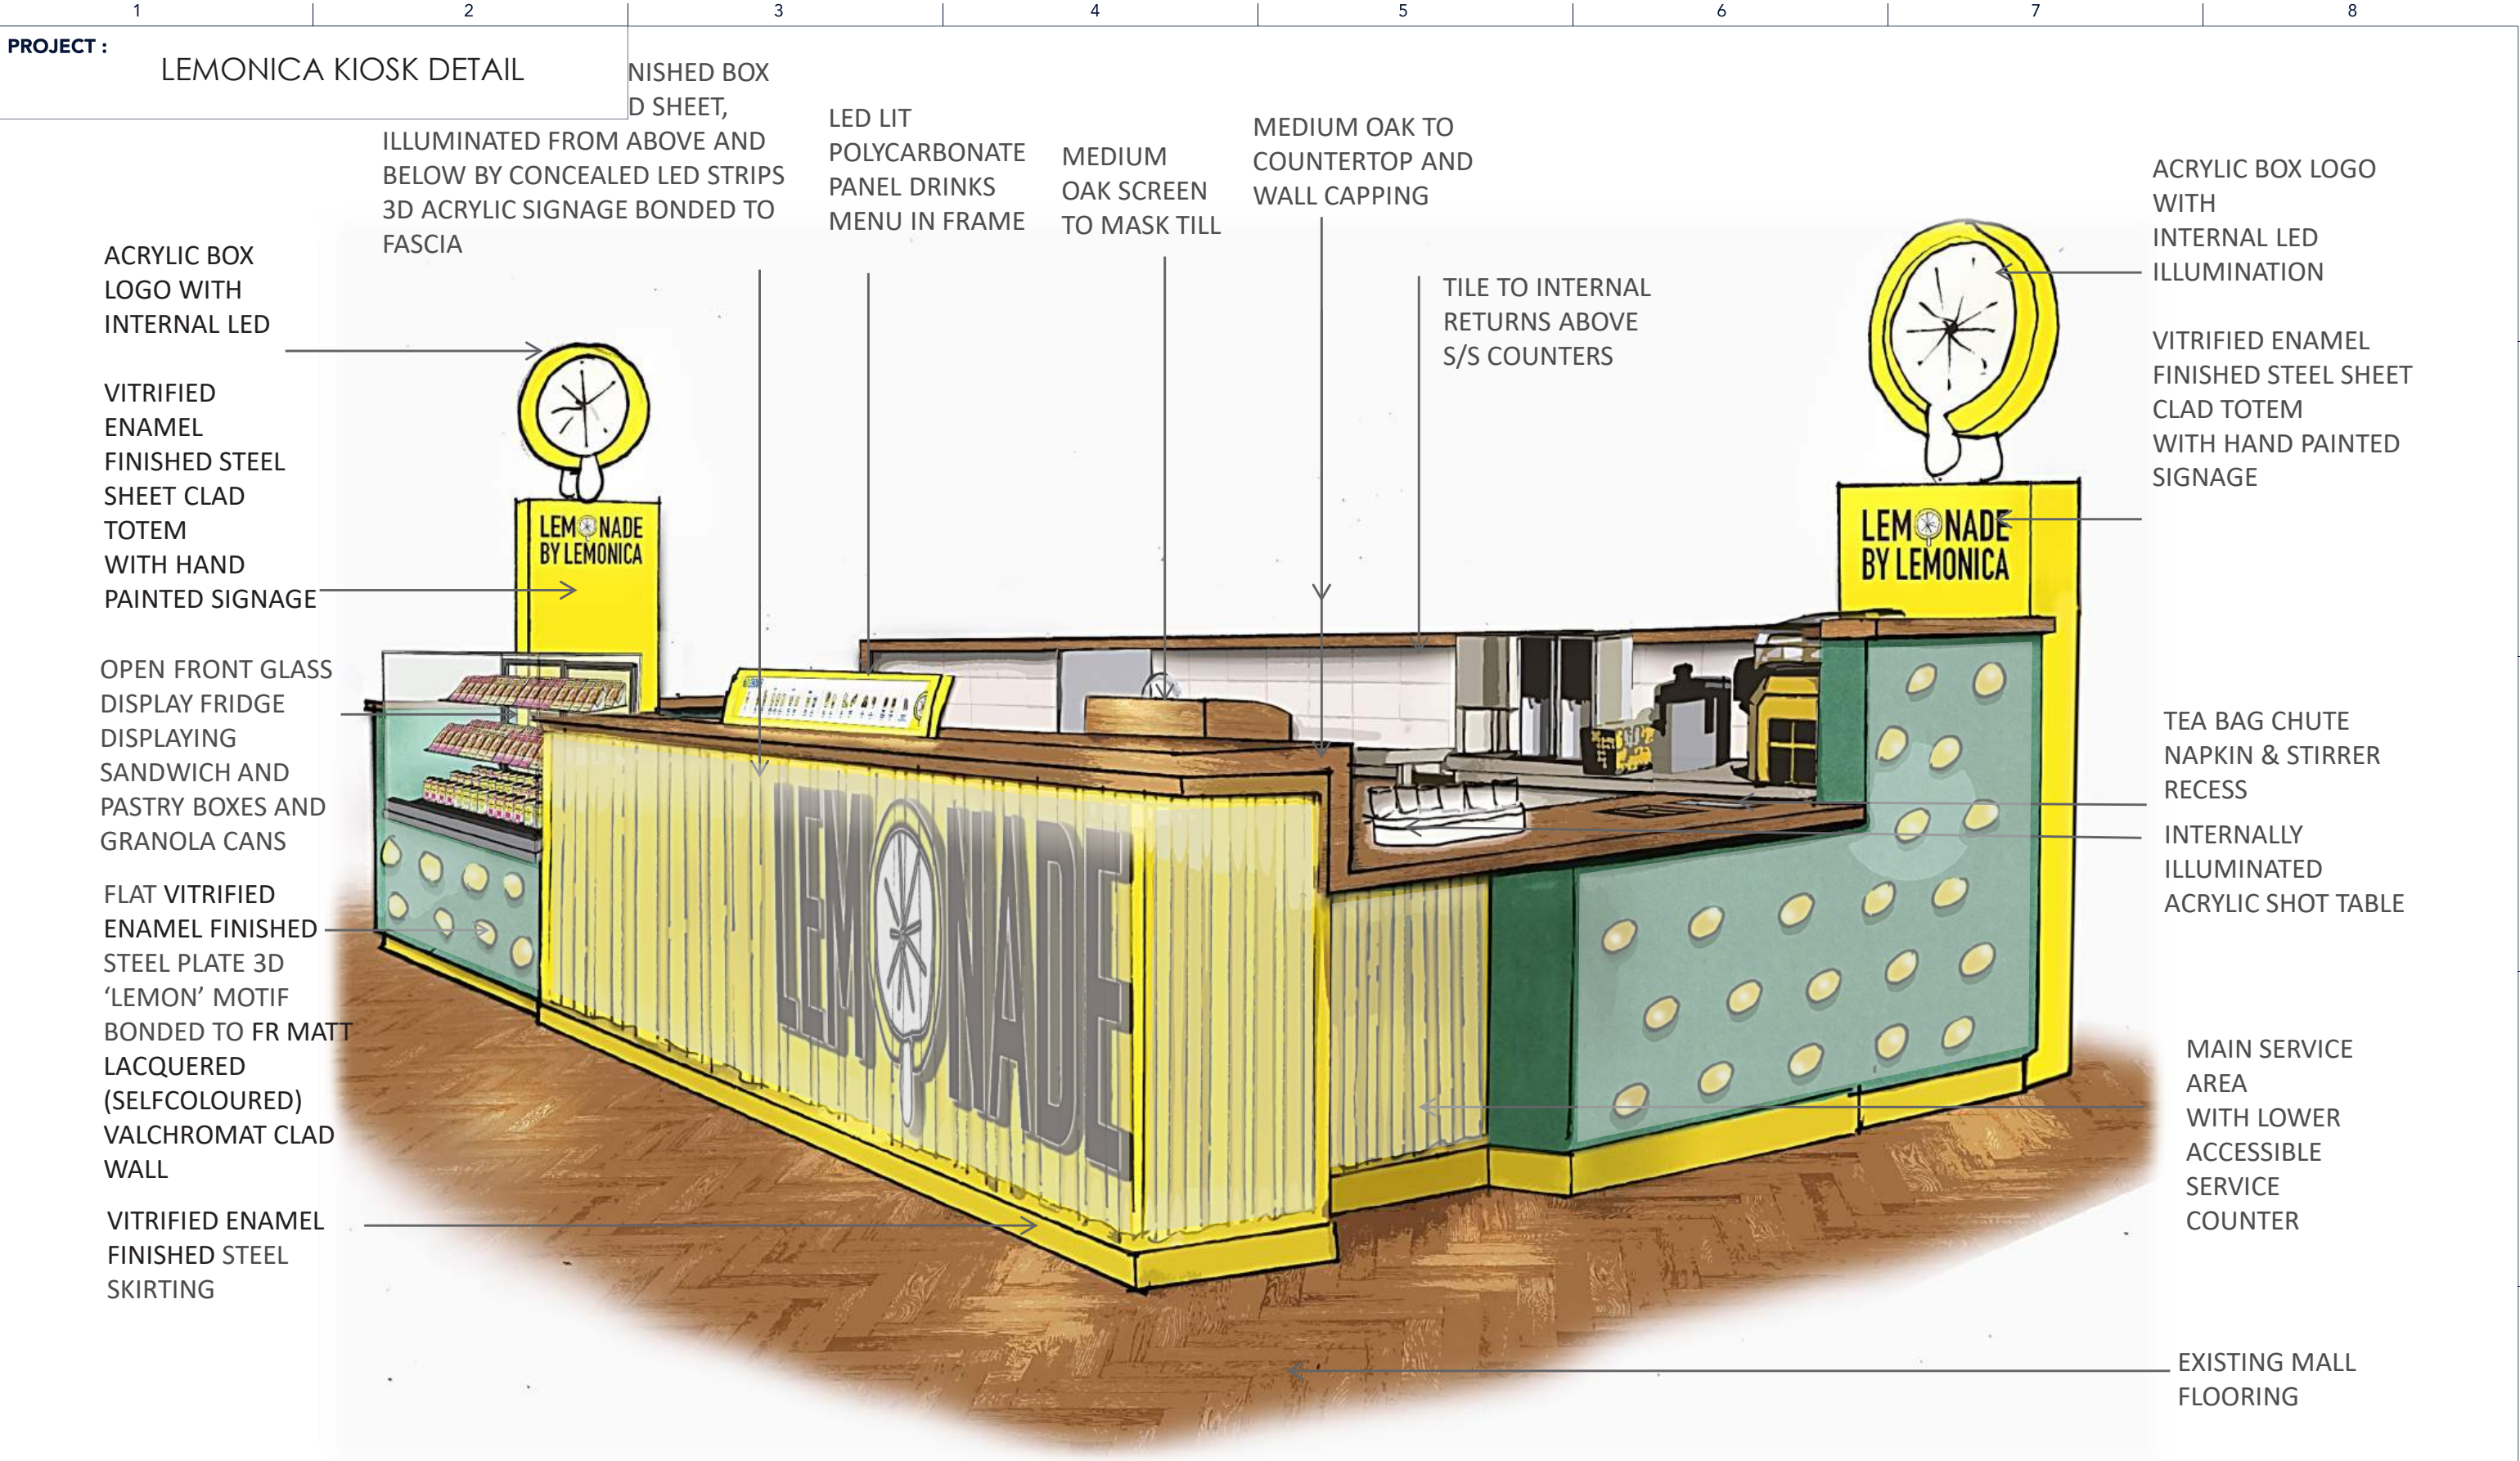

OLLYWOOD
01633 547 979 | info@ollywoodservices.co.uk
Unit 19B Springvale Industrial Estate, Cwmbran, South Wales NP44 5BA


NOTES:

- 1 UNLESS OTHERWISE SPECIFIED DIMENSIONS ARE IN MILLIMETERS.
- 2 ALL INSIDE BEND RADII TO BE MINIMUM.
- 3 REMOVE ALL BURS AND SHARP EDGES.
- 4 PART TO BE MANUFACTURED FROM SEPARATE SUPPLIED CAD FILE.
- 5 DRAWING IS FOR REFERENCE ONLY, ACTUAL DRAWINGS SUPPLIED FROM 3D ELECTRONIC DATABASE.
- 6 DO NOT SCALE DRAWING.

THIS DRAWING IS THE PROPERTY OF OLLYWOOD SERVICES AND IS PROTECTED. IT MAY NOT BE DISTRIBUTED OR USED IN ANY FORM WITHOUT WRITTEN PERMISSION.

CLIENT : LEMONICA				DRAWING TITLE :			
PROJECT : LEMONICA WESTFIELD KIOSK DETAIL				SUMMARY :			
JOB NO :	NAME	SIGNATURE	DATE	DRAWING NO :	REVISION A	MATERIAL :	
DRAWN BY :	JR		17/04/2024	PROCESS :		FINISH :	
CHECKED BY :				SCALE :		PAGE SIZE : A3	

PROJECT : LEMONICA KIOSK DETAIL

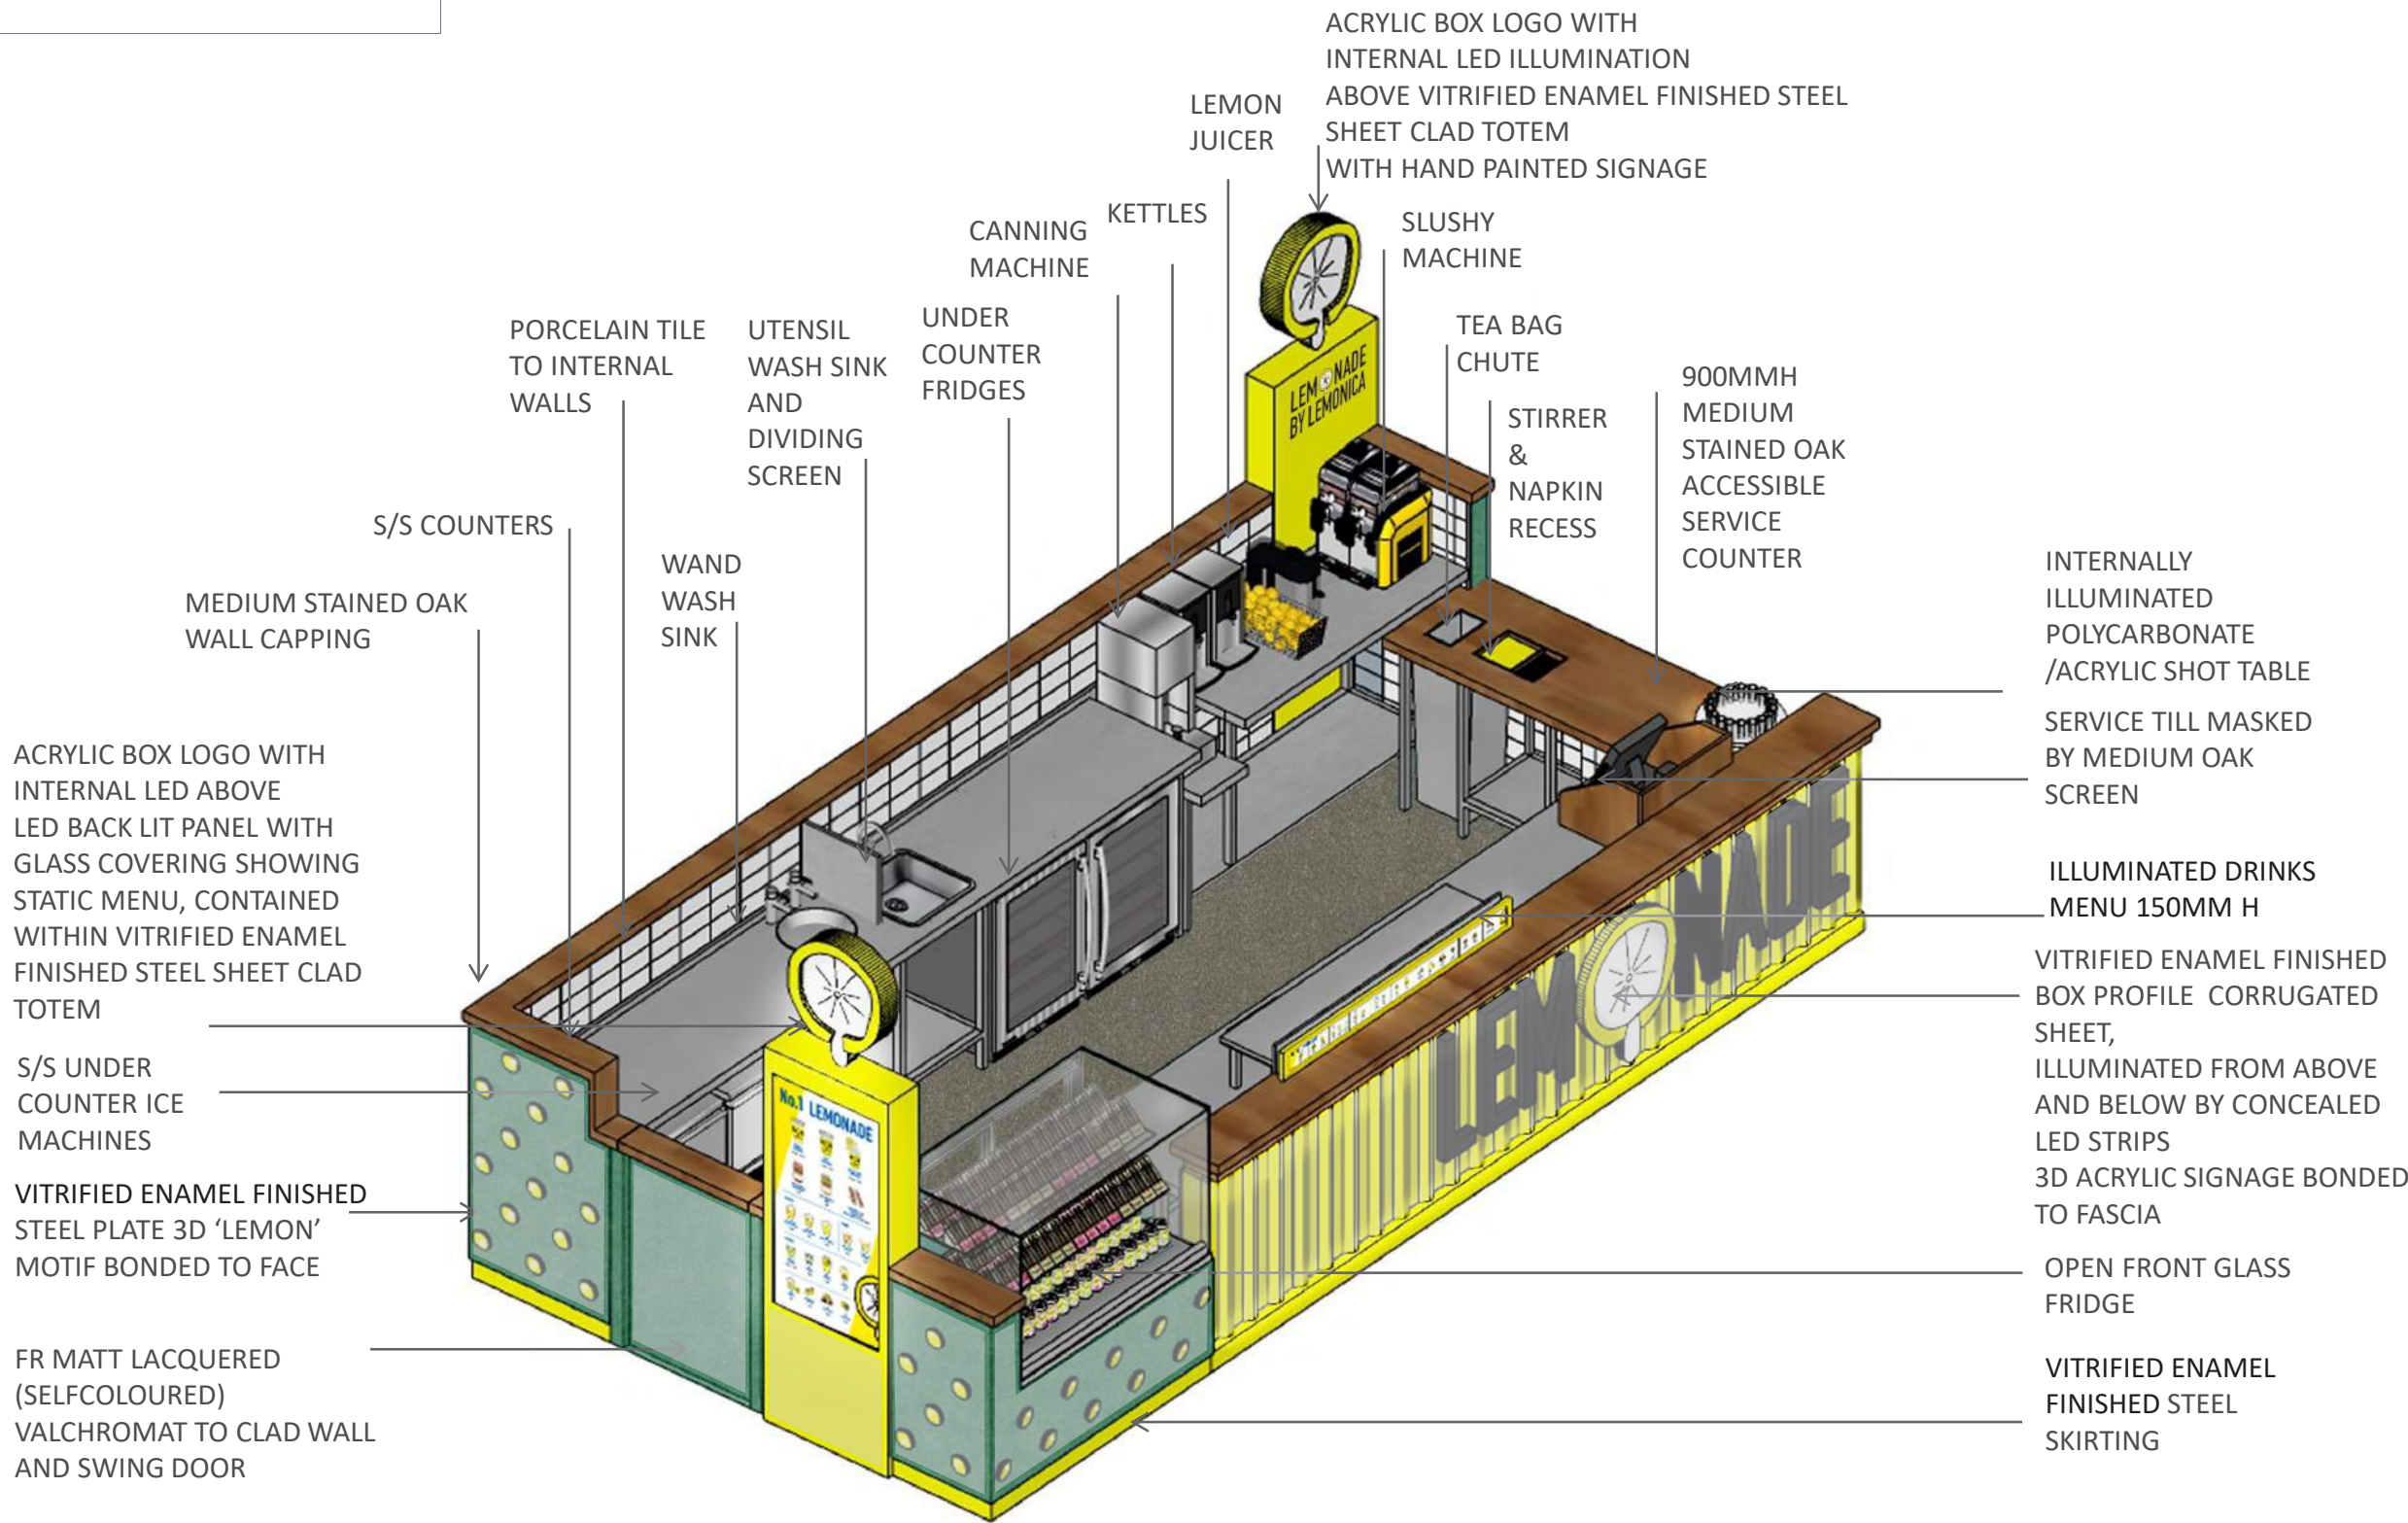

OLLYWOOD

01633 547 979 | info@ollywoodservices.co.uk
Unit 19B Springvale Industrial Estate, Cwmbran, South Wales NP44 5BA

NOTES:

- 1 UNLESS OTHERWISE SPECIFIED DIMENSIONS ARE IN MILLIMETERS.
- 2 ALL INSIDE BEND RADII TO BE MINIMUM.
- 3 REMOVE ALL BURS AND SHARP EDGES.
- 4 PART TO BE MANUFACTURED FROM SEPARATE SUPPLIED CAD FILE.
- 5 DRAWING IS FOR REFERENCE ONLY, ACTUAL DRAWINGS SUPPLIED FROM 3D ELECTRONIC DATABASE.
- 6 DO NOT SCALE DRAWING.

THIS DRAWING IS THE PROPERTY OF OLLYWOOD SERVICES AND IS PROTECTED.
IT MAY NOT BE DISTRIBUTED OR USED IN ANY FORM WITHOUT WRITTEN PERMISSION.

CLIENT : LEMONICA

PROJECT : LEMONICA WESTFIELD KIOSK DETAIL

JOB NO :

NAME

SIGNATURE

DATE

DRAWN BY :

JR

17/04/2024

CHECKED BY :

DRAWING TITLE :

SUMMARY :

DRAWING NO :

REVISION
A

MATERIAL :

PROCESS :

FINISH :



SCALE :

PAGE SIZE :

A3



MEDIUM STAIN OAK COUNTERTOP
AND WALL CAPPING



FR MATT LACQUERED (SELF COLOURED)
VALCHROMAT TO CLAD KIOSK WALLS




SLIP RESISTANT ALTRO FLOORING OVER DAMP
MEMBRANE TO INTERIOR OF KIOSK



STAINLESS STEEL TO INTERNAL
COUNTER TOPS AND DETAILS



2.5MM ALUMINIUM SHEET
COATED TO MATCH RAL: TBC

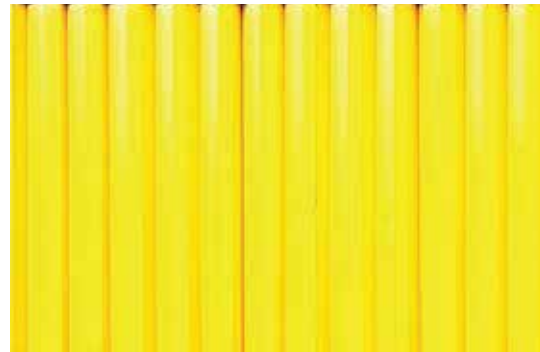

CORRUGATED STEEL SHEET
COATED TO MATCH RAL:



TILE TO INTERNAL KIOSK WALL



50X50MM WELDED COPPER MESH

No.1 LEMONADE



ORIGINAL
LEMONADE
M 3.40 | L 4.20



FIZZY
LEMONADE
M 3.40 | L 4.20



ULTRA LEMON
LEMONADE
M 4.30 | L 4.90

FROZEN



STRAWBERRY
FROZEN LEMONADE
M 5.80



BLUEBERRY
FROZEN LEMONADE
M 5.80



KIWI
FROZEN LEMONADE
M 5.80

FRUITS



FRUITS & FIZZY
LEMONADE
L 6.20



FRUITS & TEA
LEMONADE
L 6.40

OTHERS



MATCHA
LEMONADE
M 5.20 | L 5.90



COLA
LEMONADE
M 5.00



TRIPLE
LEMONADE
L 6.00



HOT
LEMONADE
2.60



KIDS
SLURPEE
2.00



VITAMIN SHOT
"FOR TWO"
6.20



ADD
FRESH FRUITS
+ 2.00



ADD
EXTRA LEMON
+ 1.00



CAN GRANOLA
STRAWBERRY
6.40



CAN GRANOLA
KIWI
6.20



SANDWICHES 3.20-
COOKIES 2.20-
MOCHI JAPANESE PASTRIES 3.00-



OLLYWOOD

ILLUMINATED ORDER POINT DRAFT ARTWORK

No.1 LEMONADE



ORIGINAL
LEMONADE

M 3.60 L 4.20



FIZZY
LEMONADE

M 3.60 L 4.20



ULTRA LEMON
LEMONADE

M 4.50 L 4.90



CAN GRANOLA
STRAWBERRY

6.40



CAN GRANOLA
KIWI

6.20



SANDWICHES 3.20~
COOKIES 2.20~
MOCHI JAPANESE PASTRIES 3.00~

FROZEN



STRAWBERRY
FROZEN LEMONADE

M 5.80



BLUEBERRY
FROZEN LEMONADE

M 5.80



KIWI
FROZEN LEMONADE

M 5.80

FRUITS



FRUITS & FIZZY
LEMONADE

L 6.20



FRUITS & TEA
LEMONADE

L 6.40

OTHERS



MATCHA
LEMONADE

M 5.20 L 5.90



COLA
LEMONADE

M 5.00



TRIPLE
LEMONADE

L 6.80



HOT
LEMONADE

3.40



KIDS
SLURPEE

2.00



VITAMIN SHOT
"FOR TWO"

6.20



ADD
FRESH FRUITS

+2.00



ADD
EXTRA LEMON

+1.00

OLLYWOOD

TOTEM ARTWORK DRAFT



C



E





C




E

PAGE SIZE : A3

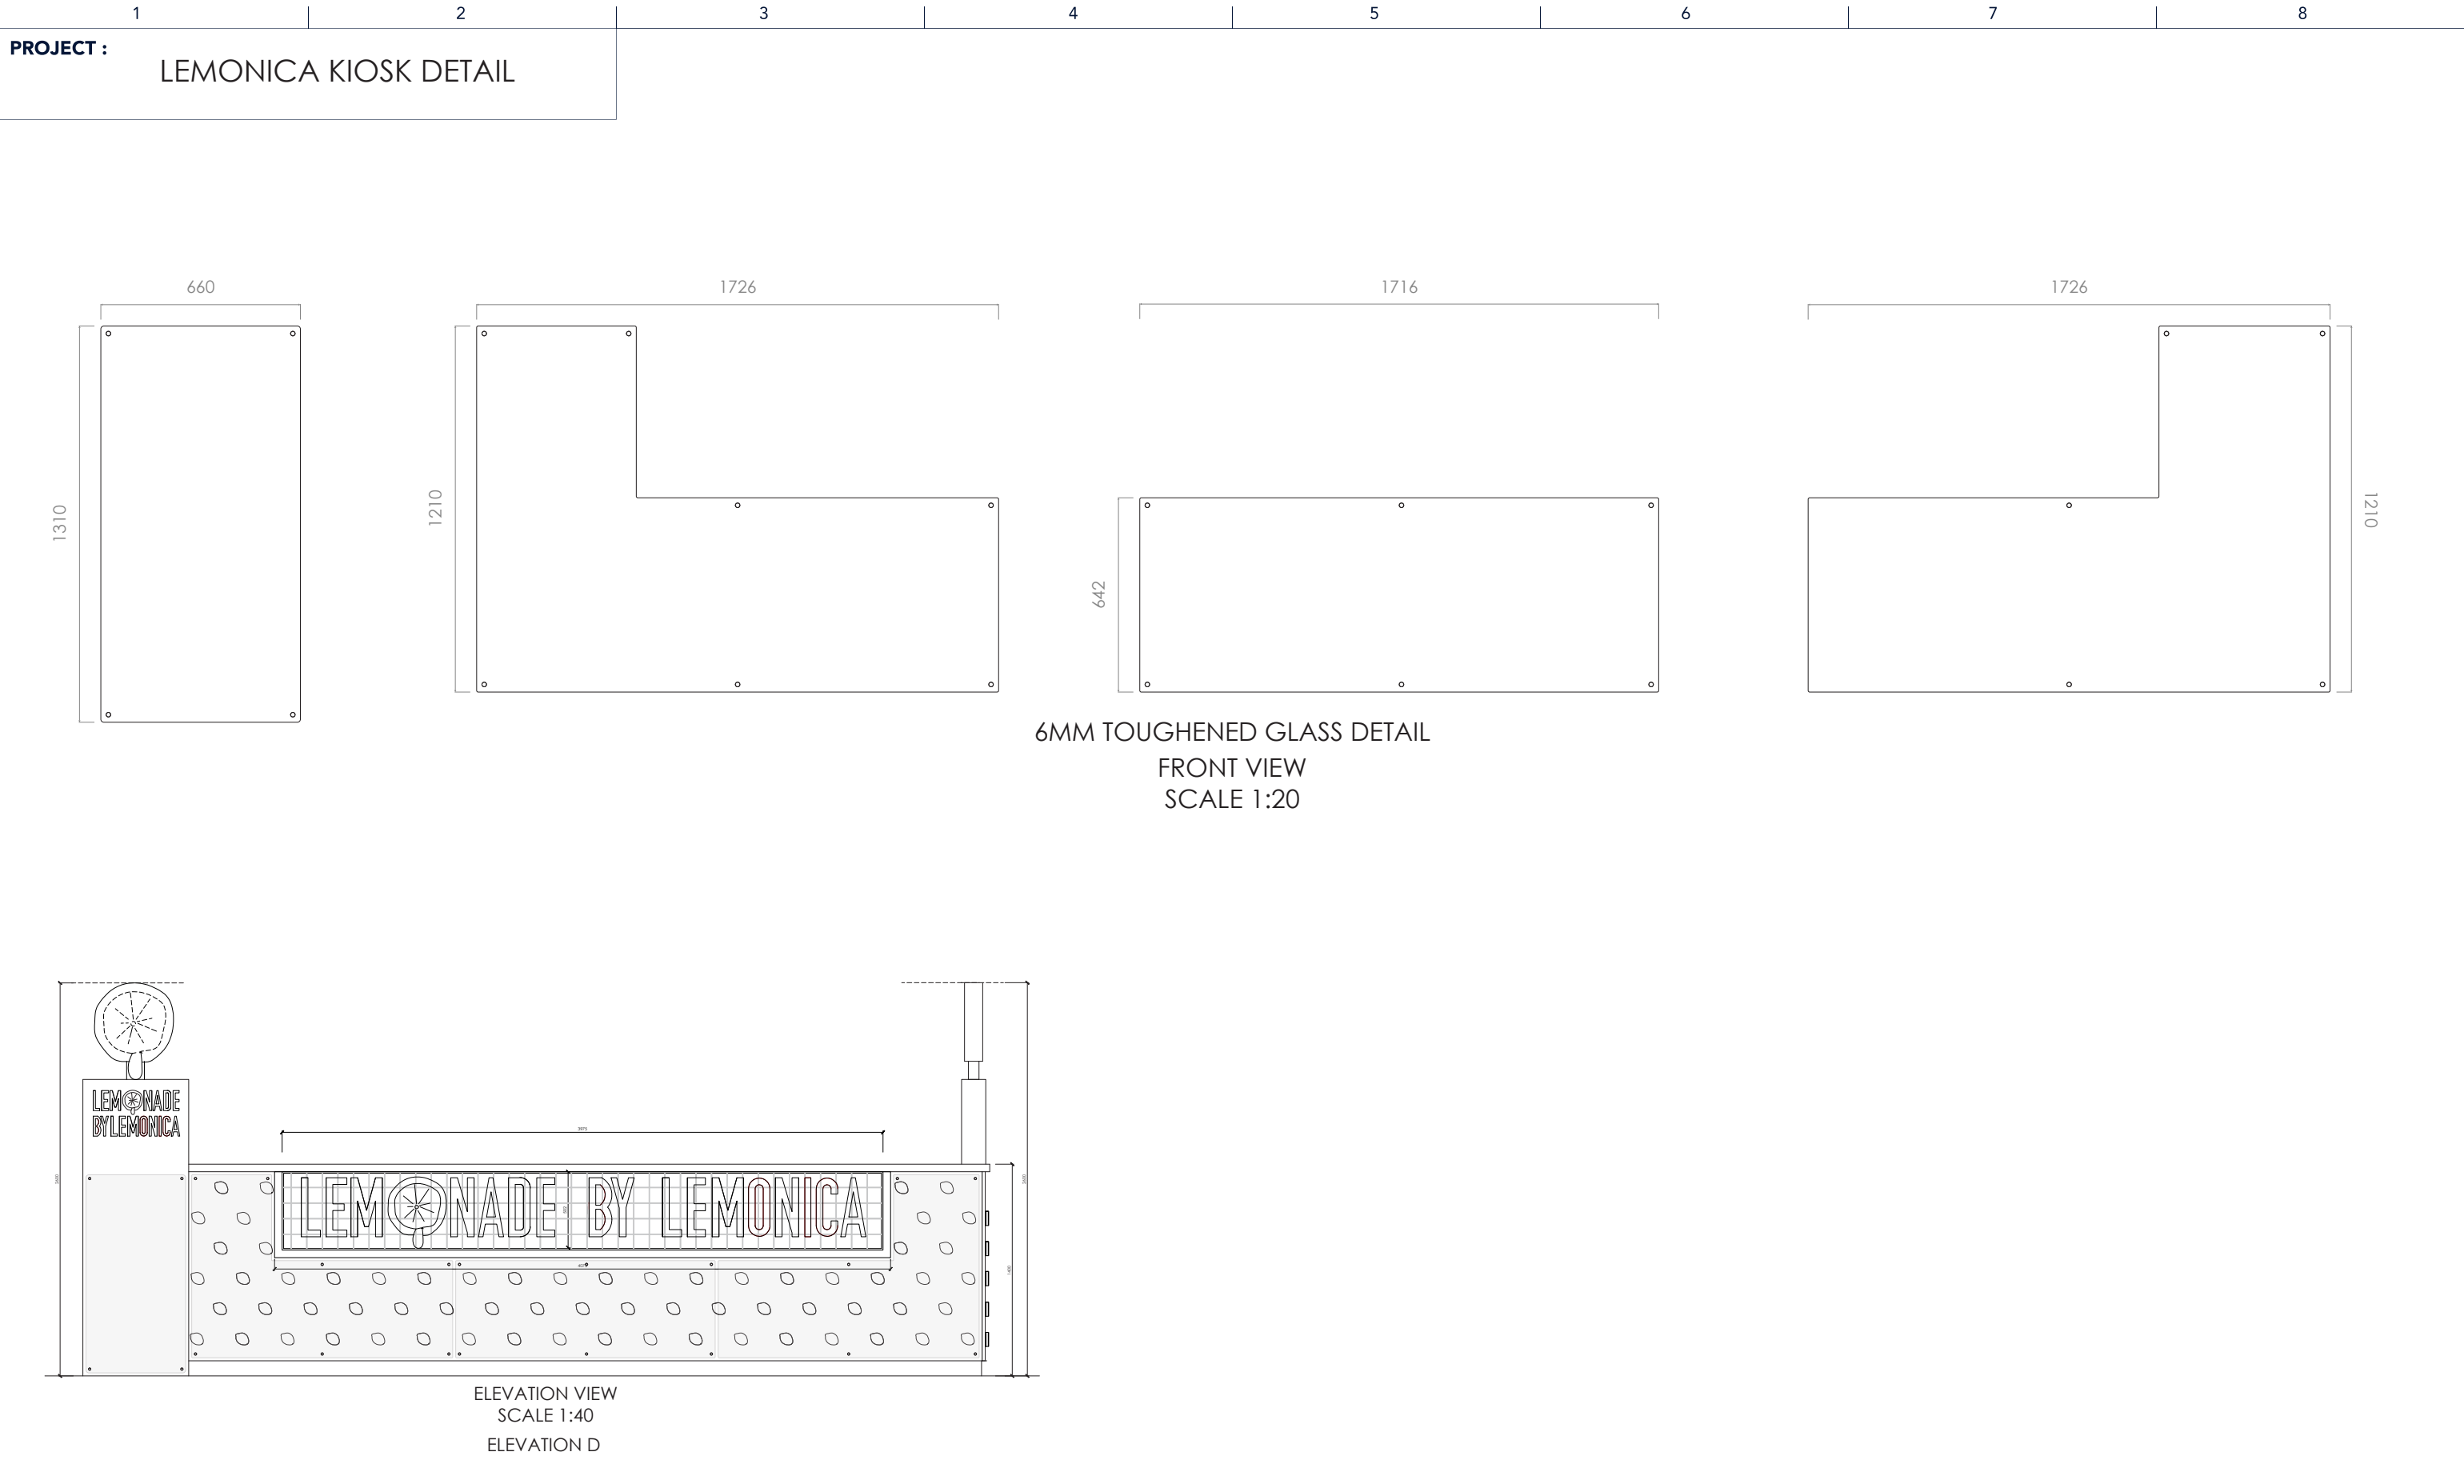

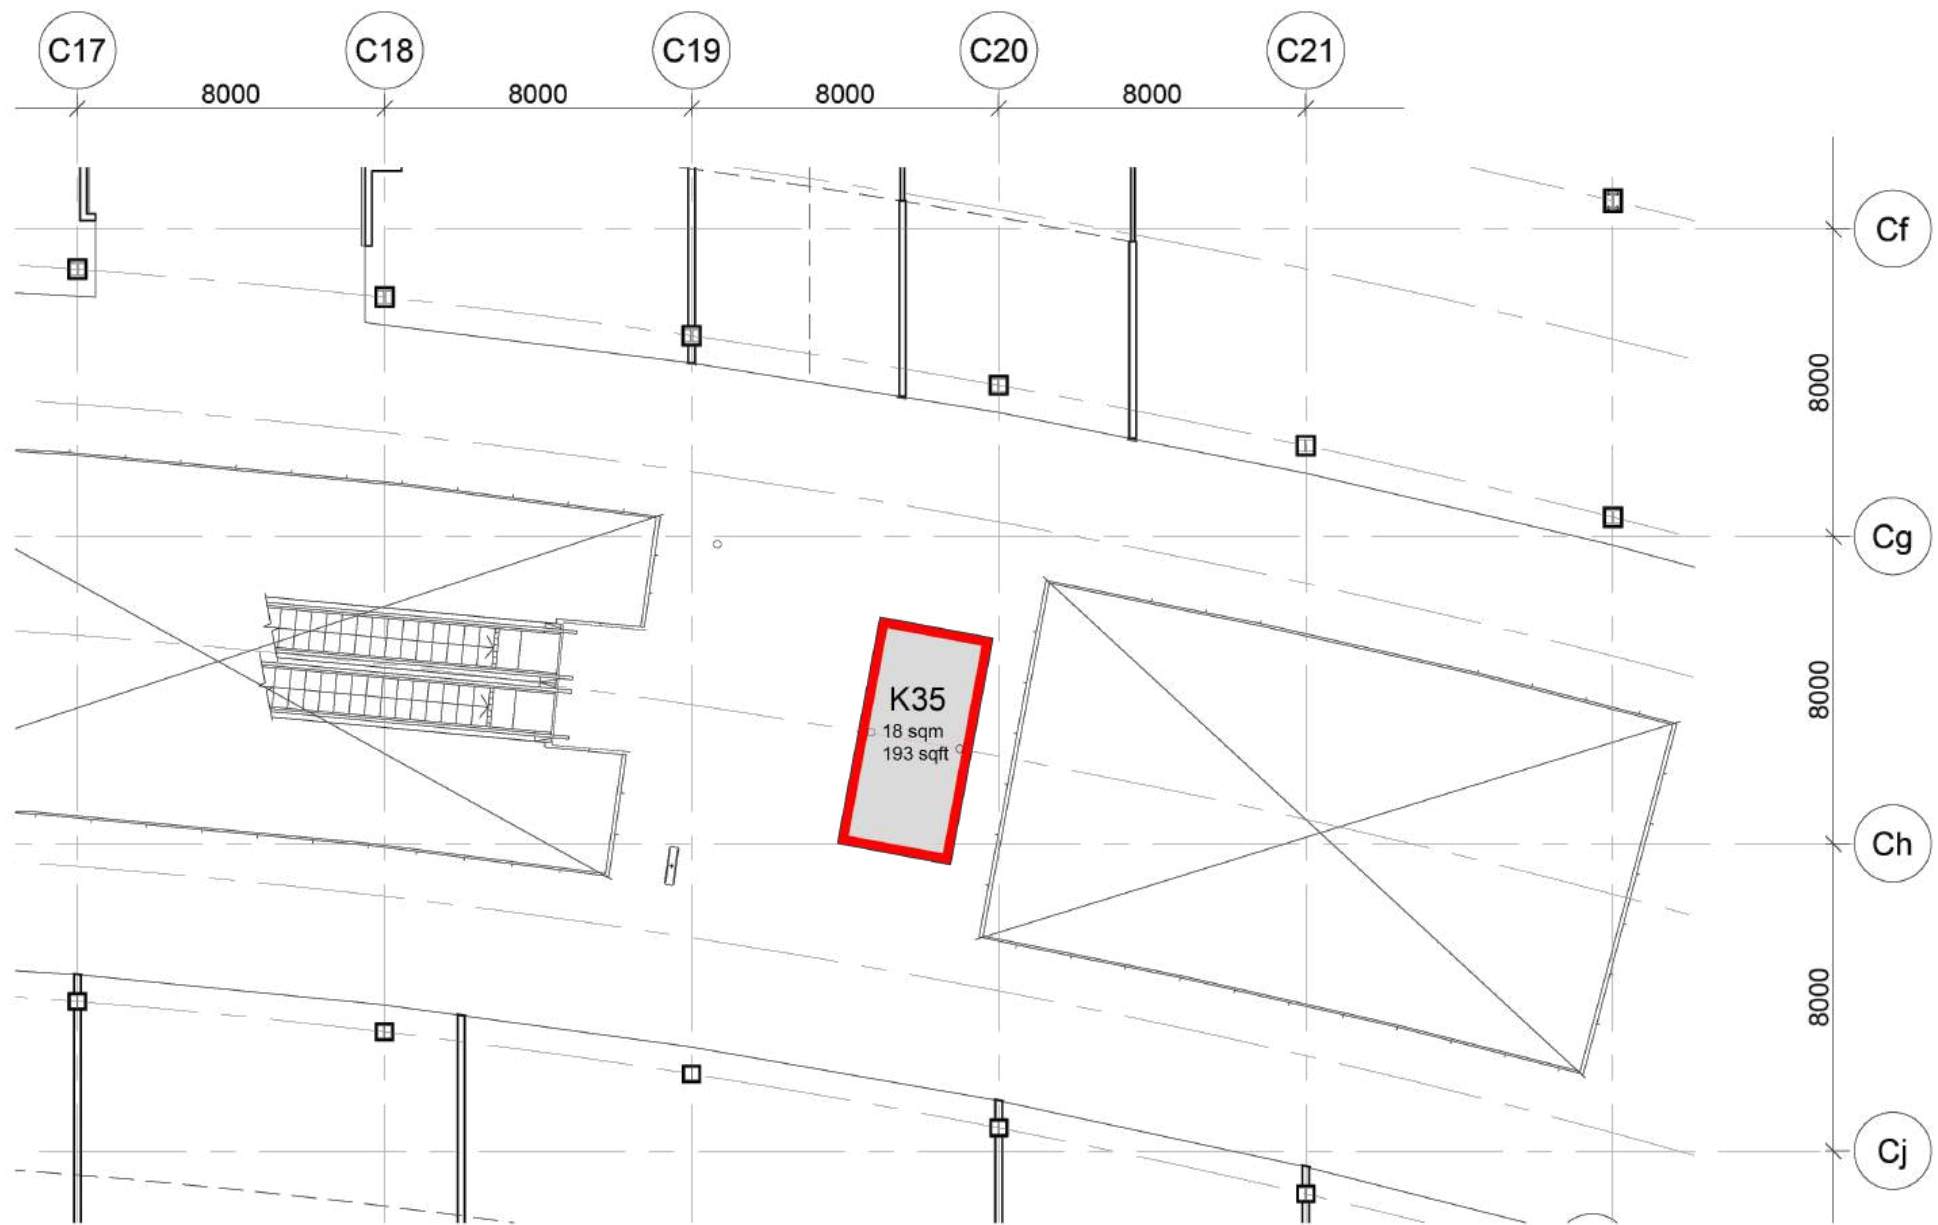

PROJECT : LEMONICA KIOSK DETAIL

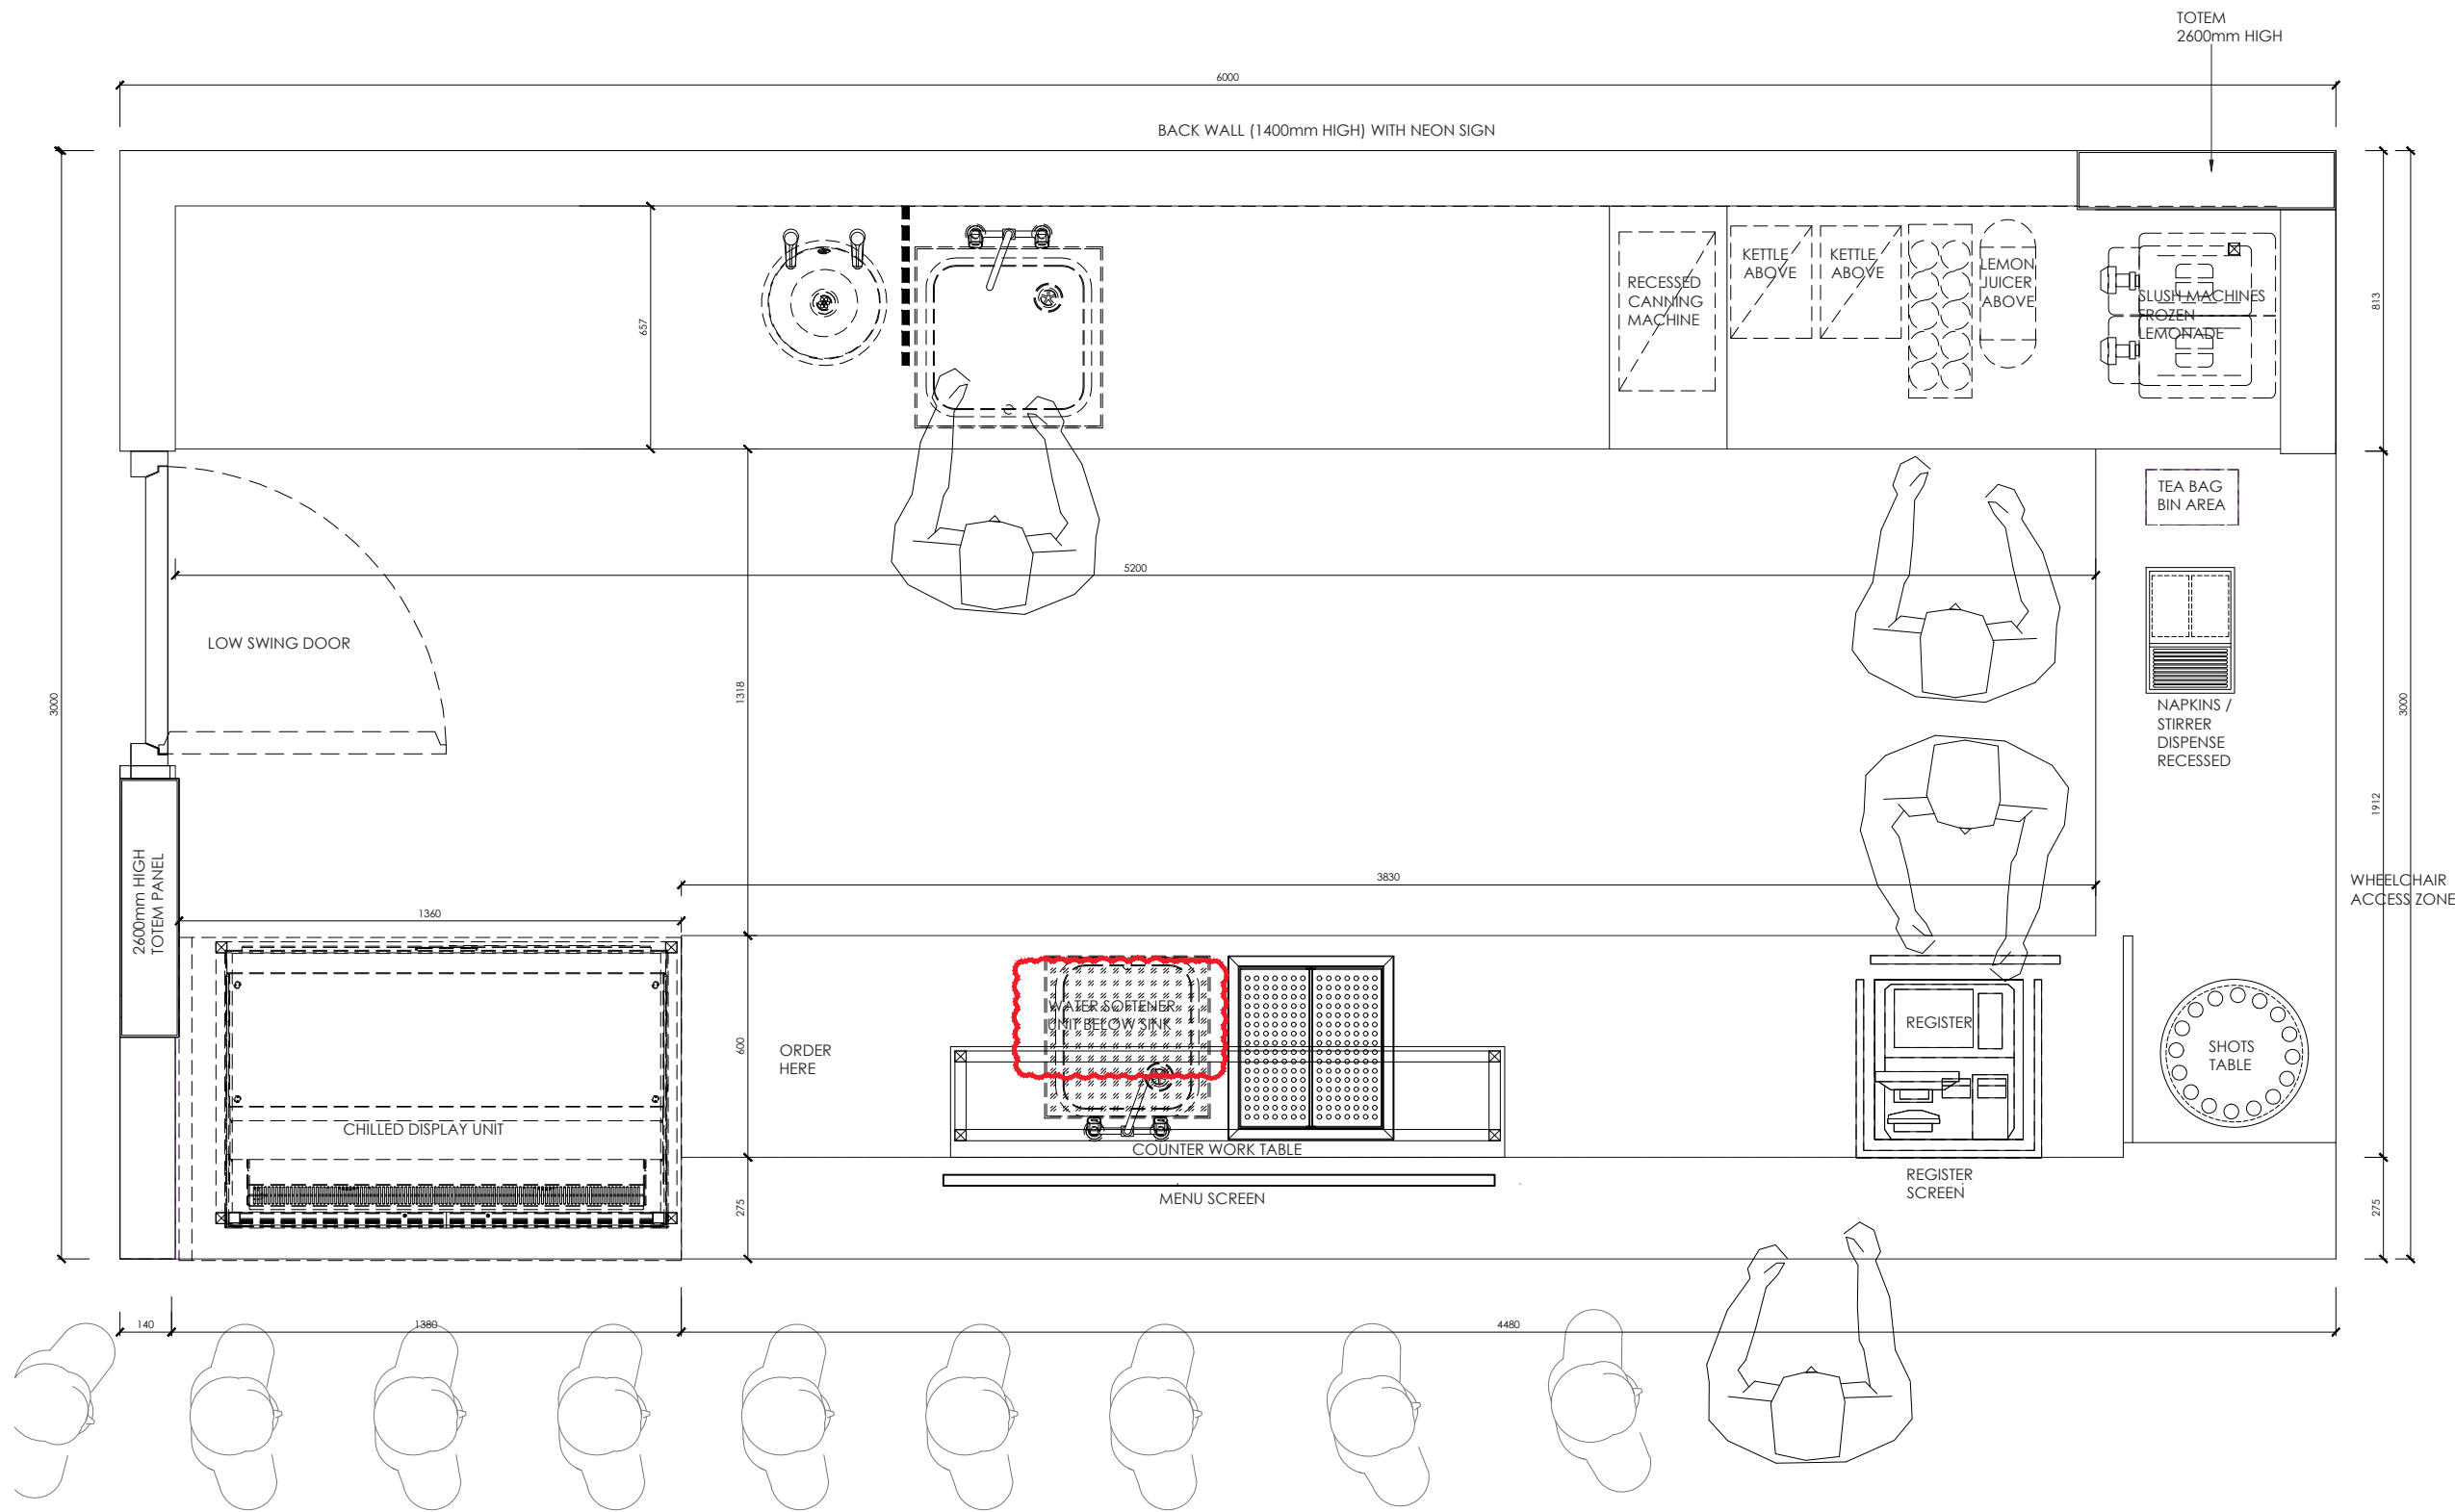

NOTES:

- 1 UNLESS OTHERWISE SPECIFIED DIMENSIONS ARE IN MILLIMETERS.
- 2 ALL INSIDE BEND RADII TO BE MINIMUM.
- 3 REMOVE ALL BURS AND SHARP EDGES.
- 4 PART TO BE MANUFACTURED FROM SEPARATE SUPPLIED CAD FILE.
- 5 DRAWING IS FOR REFERENCE ONLY, ACTUAL DRAWINGS SUPPLIED FROM 3D ELECTRONIC DATABASE.
- 6 DO NOT SCALE DRAWING.

THIS DRAWING IS THE PROPERTY OF OLLYWOOD SERVICES AND IS PROTECTED. IT MAY NOT BE DISTRIBUTED OR USED IN ANY FORM WITHOUT WRITTEN PERMISSION.

CLIENT : LEMONICA

PROJECT : LEMONICA WESTFIELD KIOSK DETAIL

JOB NO :

NAME

SIGNATURE

DATE

DRAWN BY :

JR

17/04/2024

CHECKED BY :

DRAWING TITLE :

SUMMARY :


DRAWING NO :

REVISION
A

MATERIAL :

PROCESS :

FINISH :

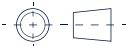


SCALE :

PAGE SIZE :


A3

OLLYWOOD


01633 547 979 | info@ollywoodservices.co.uk
Unit 19B Springvale Industrial Estate, Cwmbran, South Wales NP44 5BA

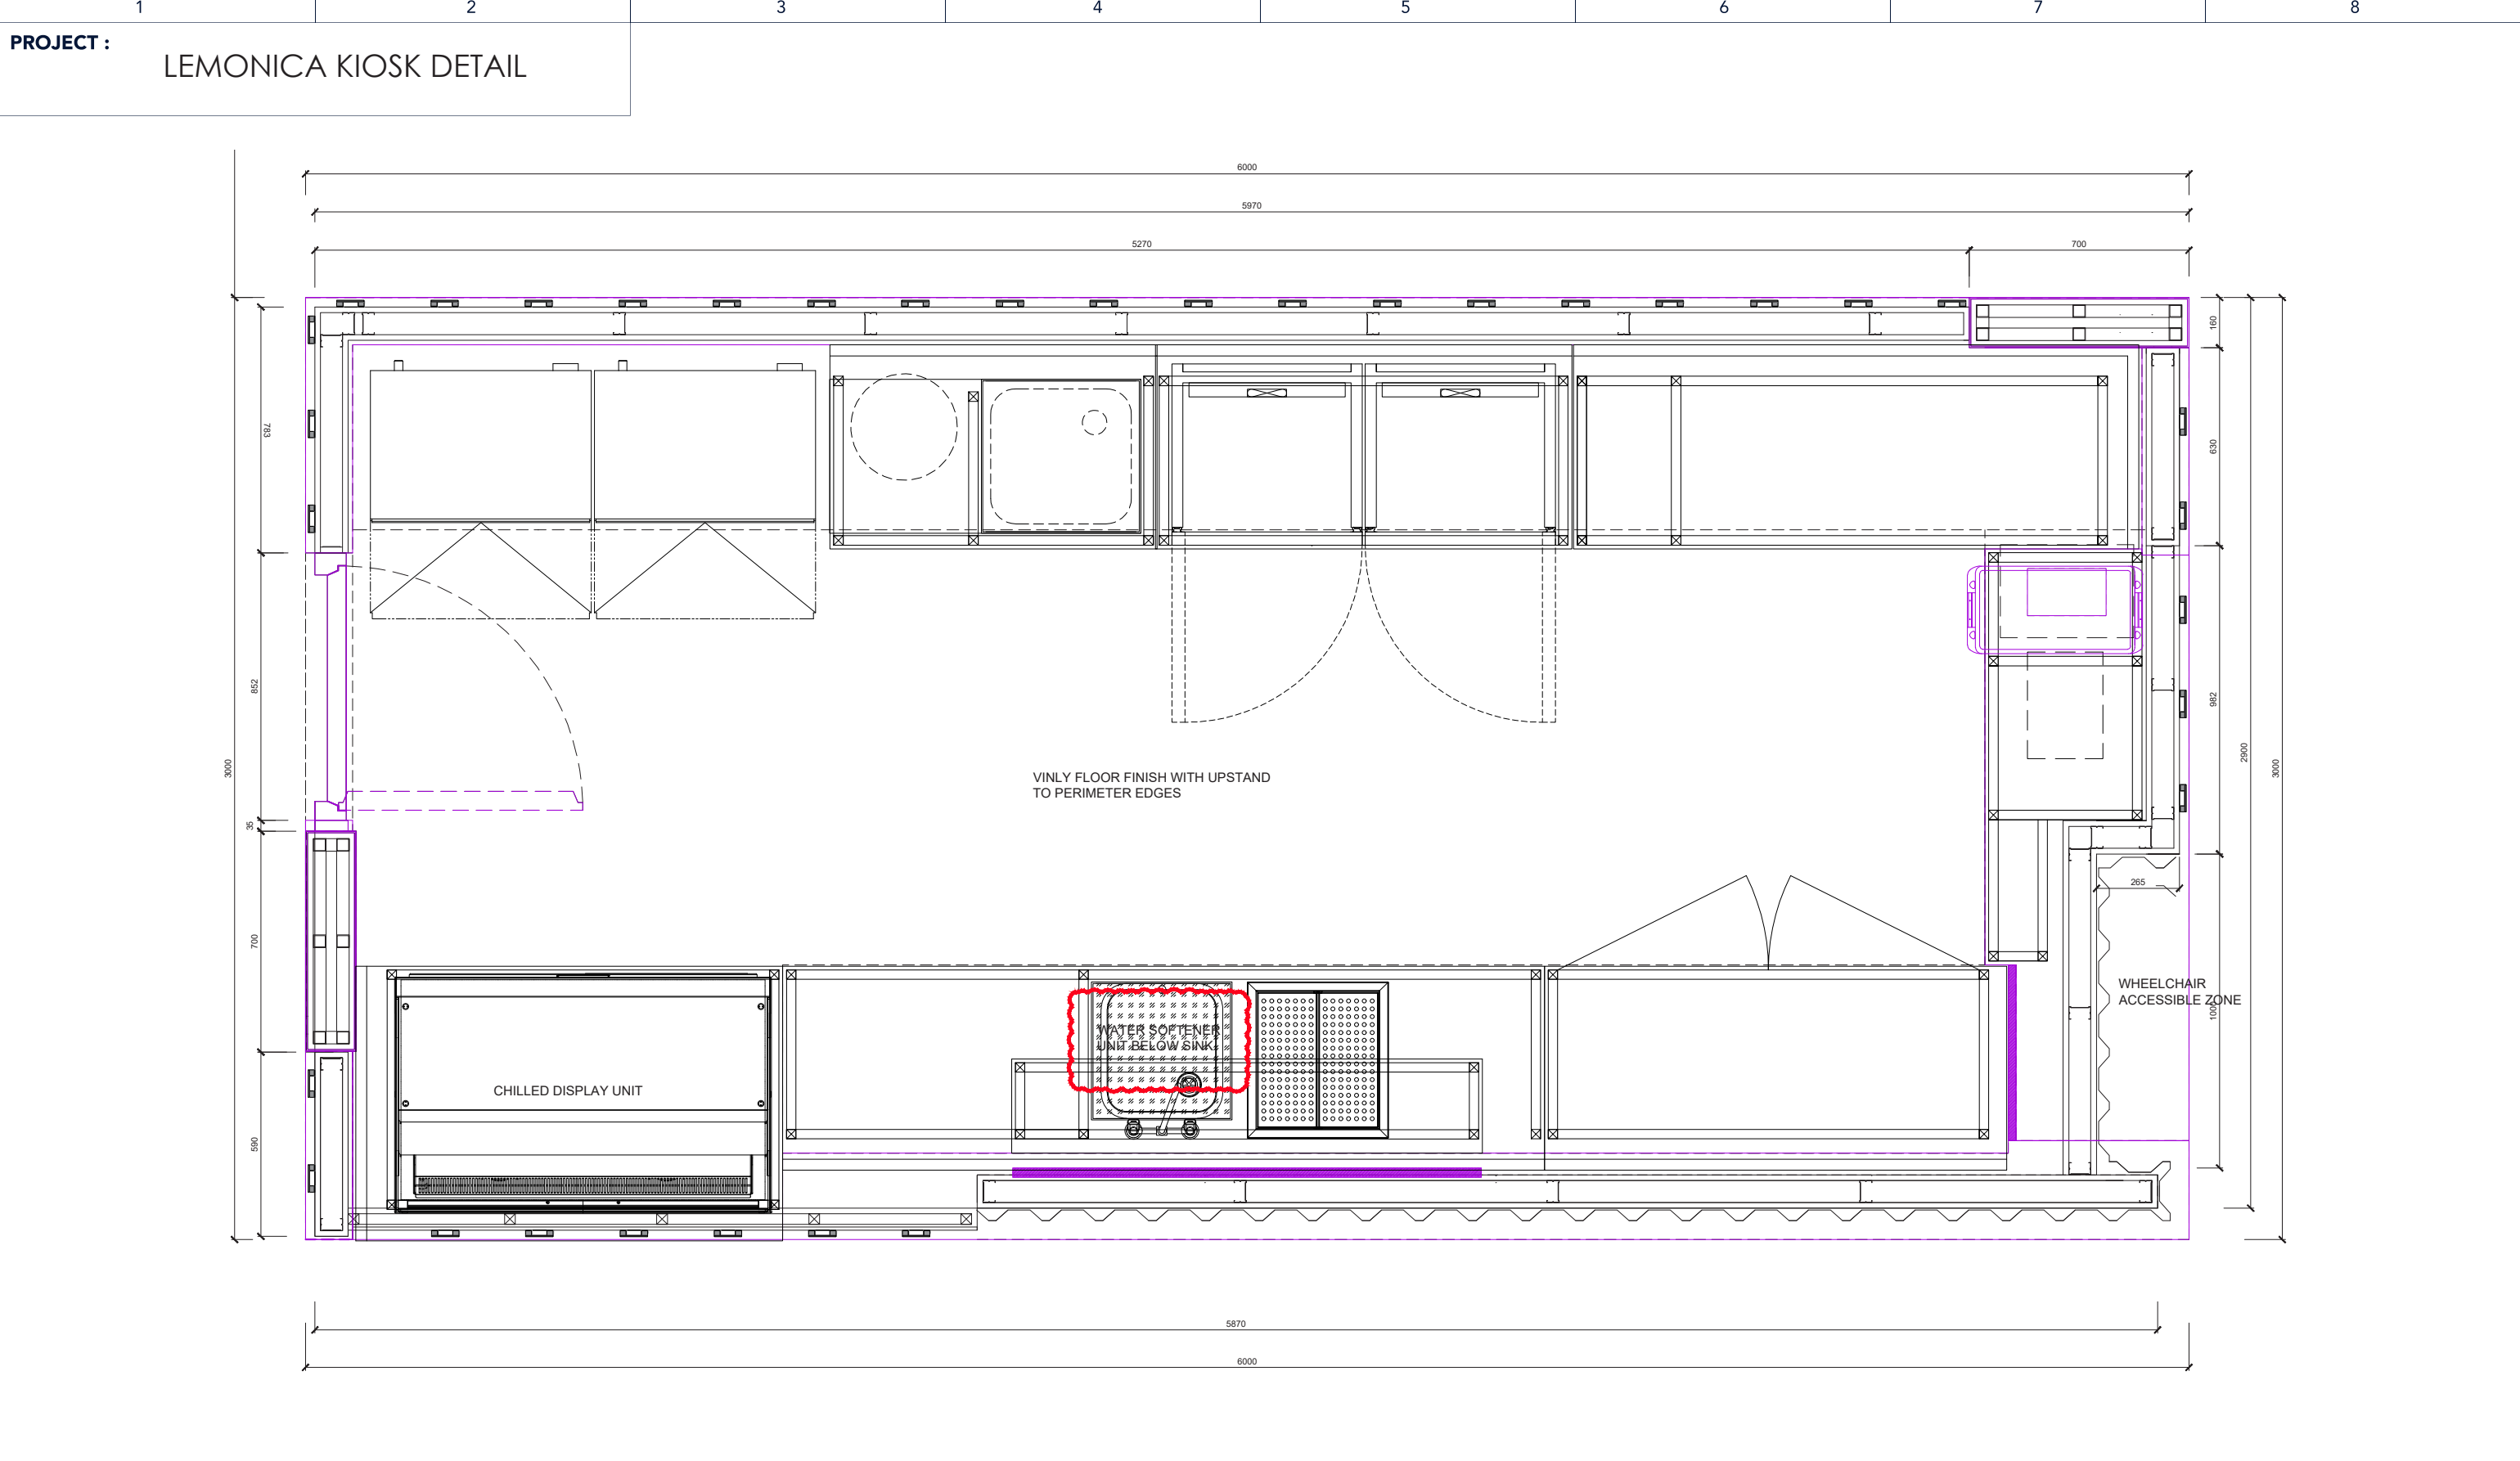

OLLYWOOD 01633 547 979 info@ollywoodservices.co.uk Unit 19B Springvale Industrial Estate, Cwmbran, South Wales NP44 5BA		NOTES: 1 UNLESS OTHERWISE SPECIFIED DIMENSIONS ARE IN MILLIMETERS. 2 ALL INSIDE BEND RADII TO BE MINIMUM. 3 REMOVE ALL BURS AND SHARP EDGES. 4 PART TO BE MANUFACTURED FROM SEPARATE SUPPLIED CAD FILE. 5 DRAWING IS FOR REFERENCE ONLY, ACTUAL DRAWINGS SUPPLIED FROM 3D ELECTRONIC DATABASE. 6 DO NOT SCALE DRAWING.		CLIENT : LEMONICA		DRAWING TITLE :	
				PROJECT : LEMONICA WESTFIELD KIOSK DETAIL		SUMMARY :	
				JOB NO :	NAME	SIGNATURE	DATE
				DRAWN BY :	JR		17/04/2024
				CHECKED BY :			
THIS DRAWING IS THE PROPERTY OF OLLYWOOD SERVICES AND IS PROTECTED. IT MAY NOT BE DISTRIBUTED OR USED IN ANY FORM WITHOUT WRITTEN PERMISSION.				DRAWING NO :		REVISION	MATERIAL :
				PROCESS :		A	FINISH :
				SCALE :		PAGE SIZE : A3	

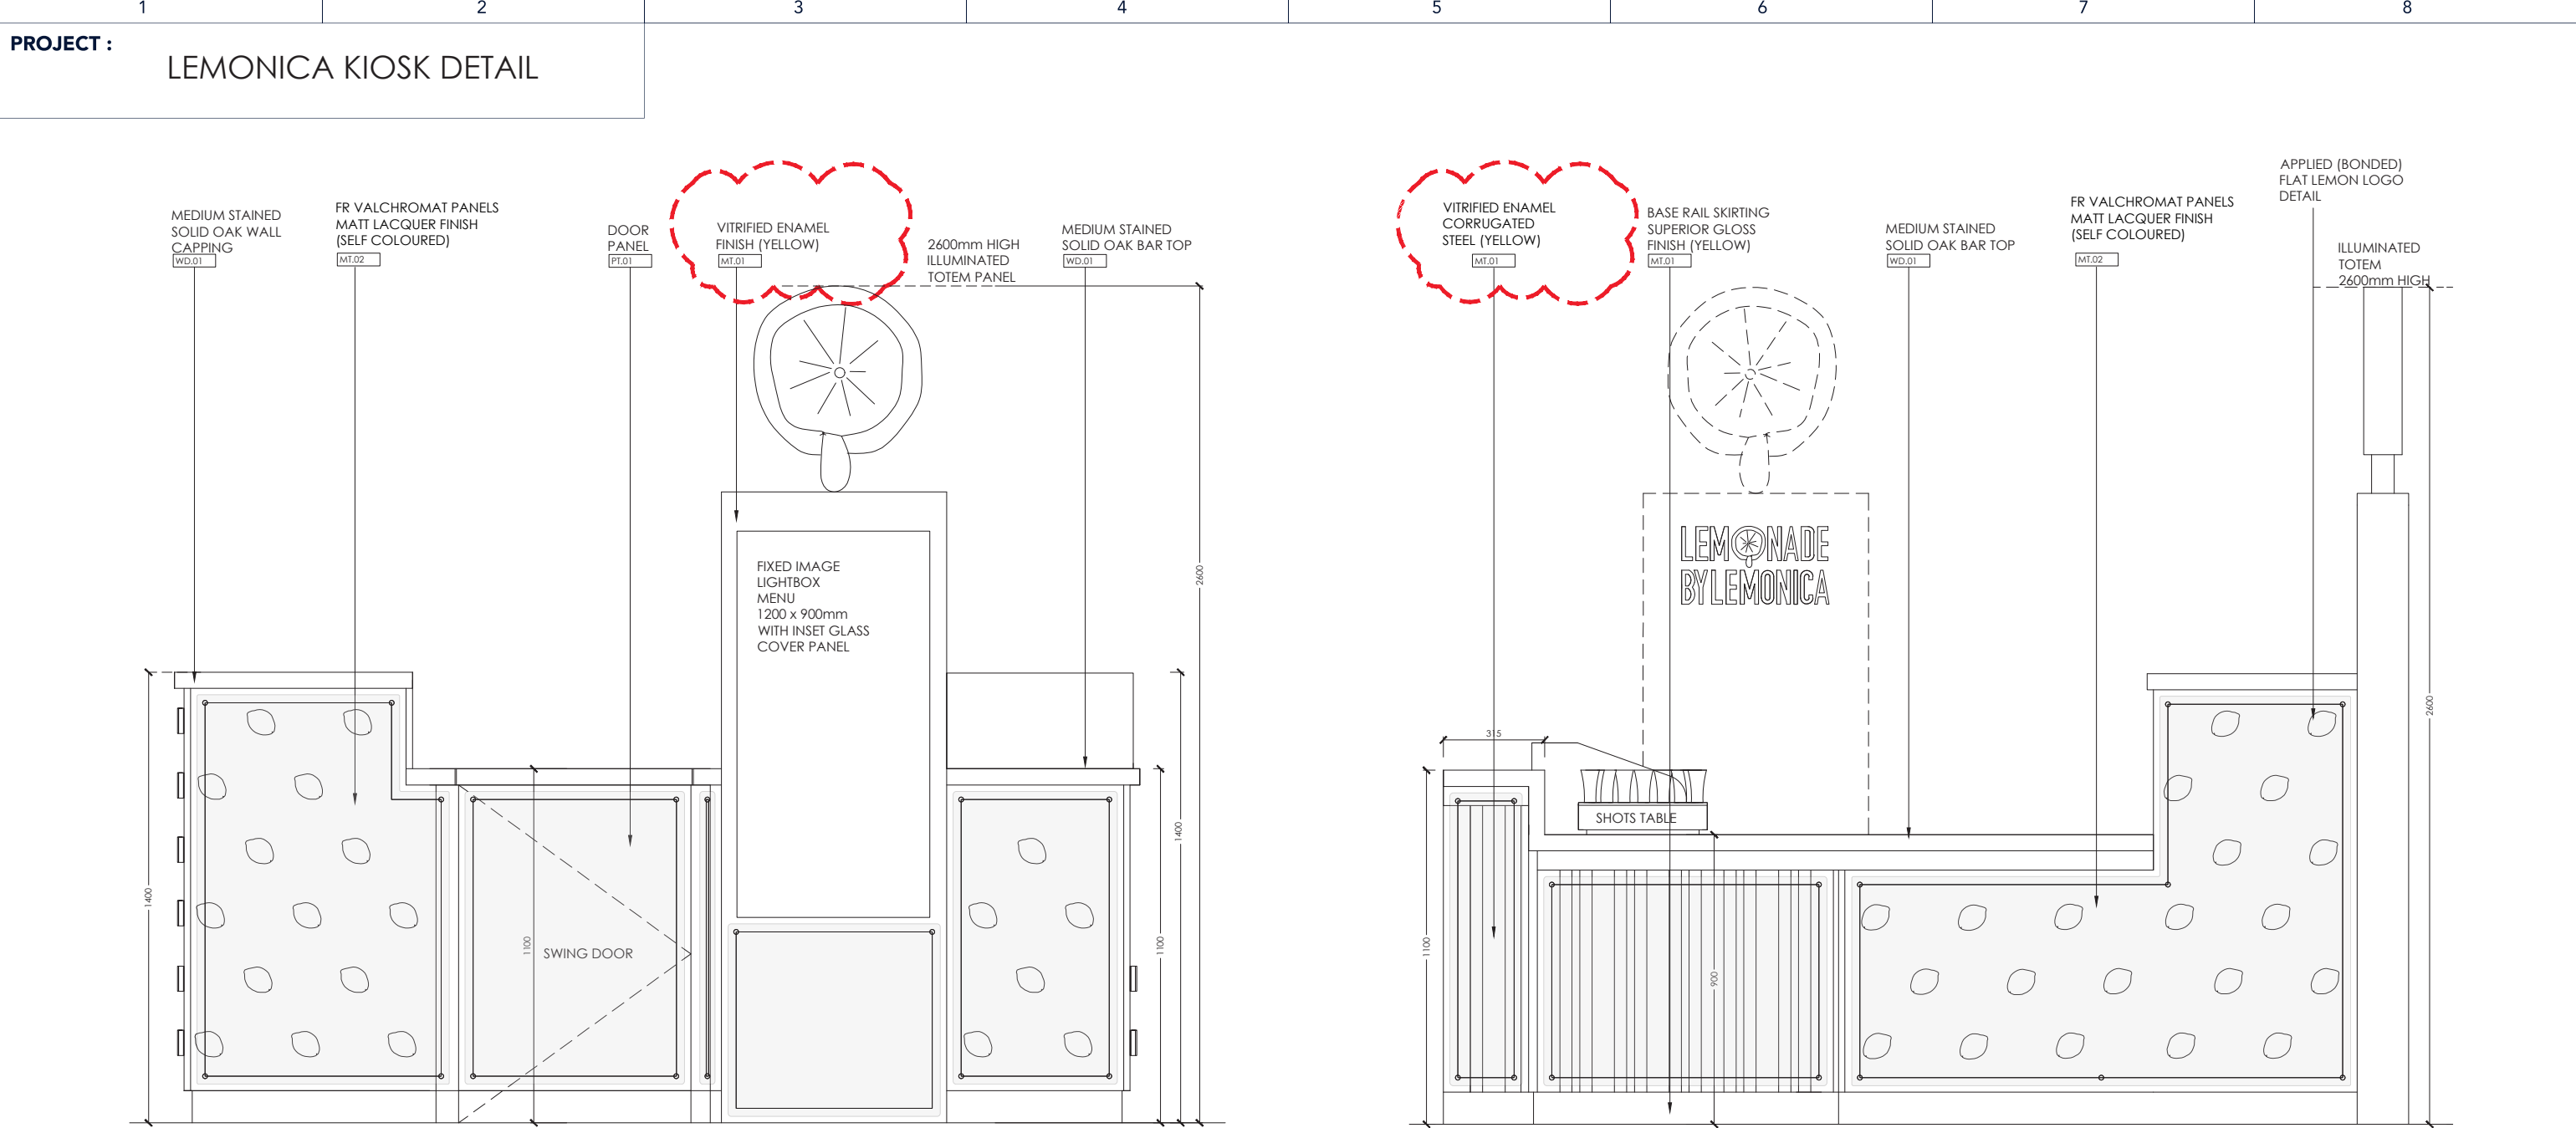

ELEVATION C

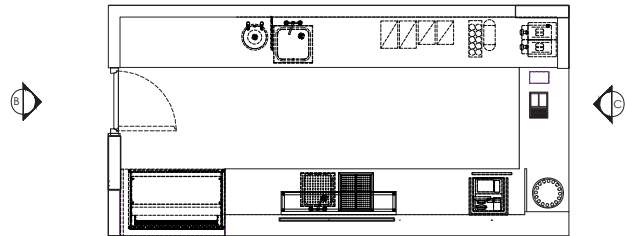

NOTES:


- 1 UNLESS OTHERWISE SPECIFIED DIMENSIONS ARE IN MILLIMETERS.
- 2 ALL INSIDE BEND RADII TO BE MINIMUM.
- 3 REMOVE ALL BURS AND SHARP EDGES.
- 4 PART TO BE MANUFACTURED FROM SEPARATE SUPPLIED CAD FILE.
- 5 DRAWING IS FOR REFERENCE ONLY, ACTUAL DRAWINGS SUPPLIED FROM 3D ELECTRONIC DATABASE.
- 6 DO NOT SCALE DRAWING.

THIS DRAWING IS THE PROPERTY OF OLLYWOOD SERVICES AND IS PROTECTED. IT MAY NOT BE DISTRIBUTED OR USED IN ANY FORM WITHOUT WRITTEN PERMISSION.

CLIENT : LEMONICA				DRAWING TITLE :			
PROJECT : LEMONICA WESTFIELD KIOSK DETAIL				SUMMARY :			
JOB NO :	NAME	SIGNATURE	DATE	DRAWING NO :	REVISION A	MATERIAL :	
DRAWN BY :	JR		17/04/2024	PROCESS :		FINISH :	
CHECKED BY :				SCALE :			PAGE SIZE : A3

OLLYWOOD

01633 547 979 | info@ollywoodservices.co.uk
Unit 19B Springvale Industrial Estate, Cwmbran, South Wales NP44 5BA

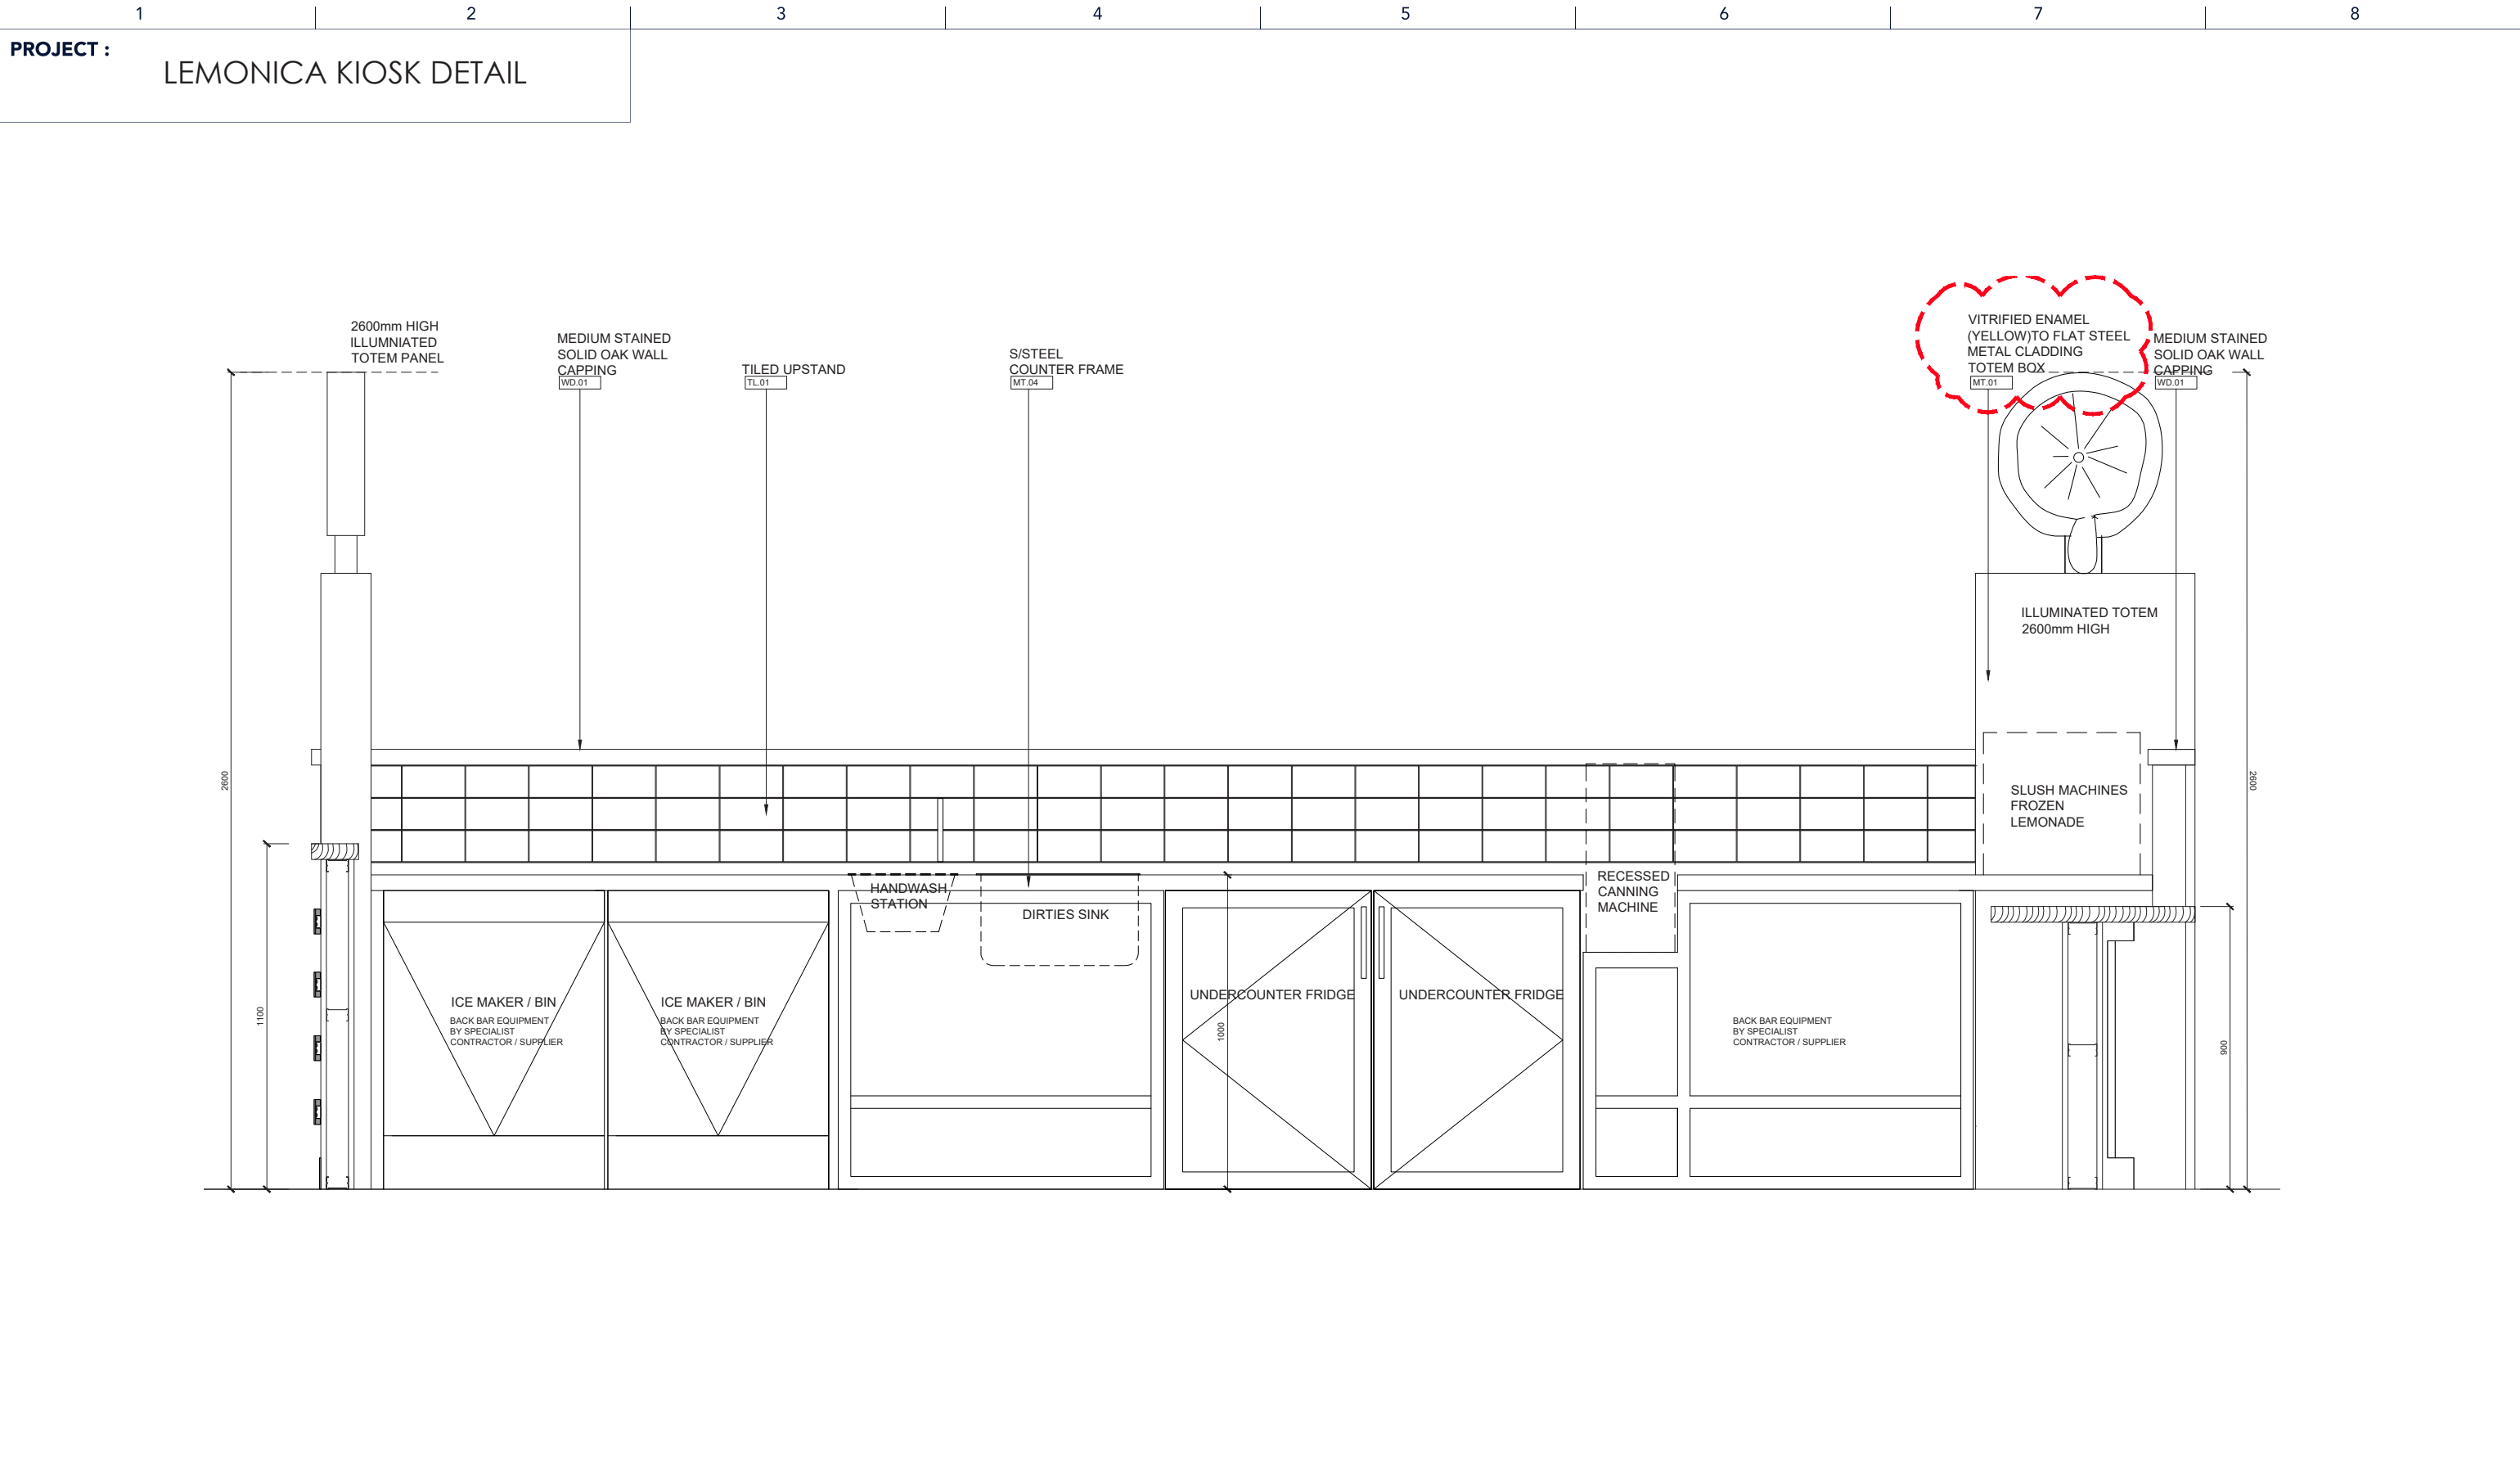

OLLYWOOD


01633 547 979 | info@ollywoodservices.co.uk
Unit 19B Springvale Industrial Estate, Cwmbran, South Wales NP44 5BA

NOTES:


- 1 UNLESS OTHERWISE SPECIFIED DIMENSIONS ARE IN MILLIMETERS.
- 2 ALL INSIDE BEND RADII TO BE MINIMUM.
- 3 REMOVE ALL BURS AND SHARP EDGES.
- 4 PART TO BE MANUFACTURED FROM SEPARATE SUPPLIED CAD FILE.
- 5 DRAWING IS FOR REFERENCE ONLY, ACTUAL DRAWINGS SUPPLIED FROM 3D ELECTRONIC DATABASE.
- 6 DO NOT SCALE DRAWING.

THIS DRAWING IS THE PROPERTY OF OLLYWOOD SERVICES AND IS PROTECTED.
IT MAY NOT BE DISTRIBUTED OR USED IN ANY FORM WITHOUT WRITTEN PERMISSION.

CLIENT : LEMONICA				DRAWING TITLE :			
PROJECT : LEMONICA WESTFIELD KIOSK DETAIL				SUMMARY :			
JOB NO :	NAME	SIGNATURE	DATE	DRAWING NO :	REVISION A	MATERIAL :	
DRAWN BY :	JR		17/04/2024	PROCESS :		FINISH :	
CHECKED BY :						SCALE :	PAGE SIZE : A3

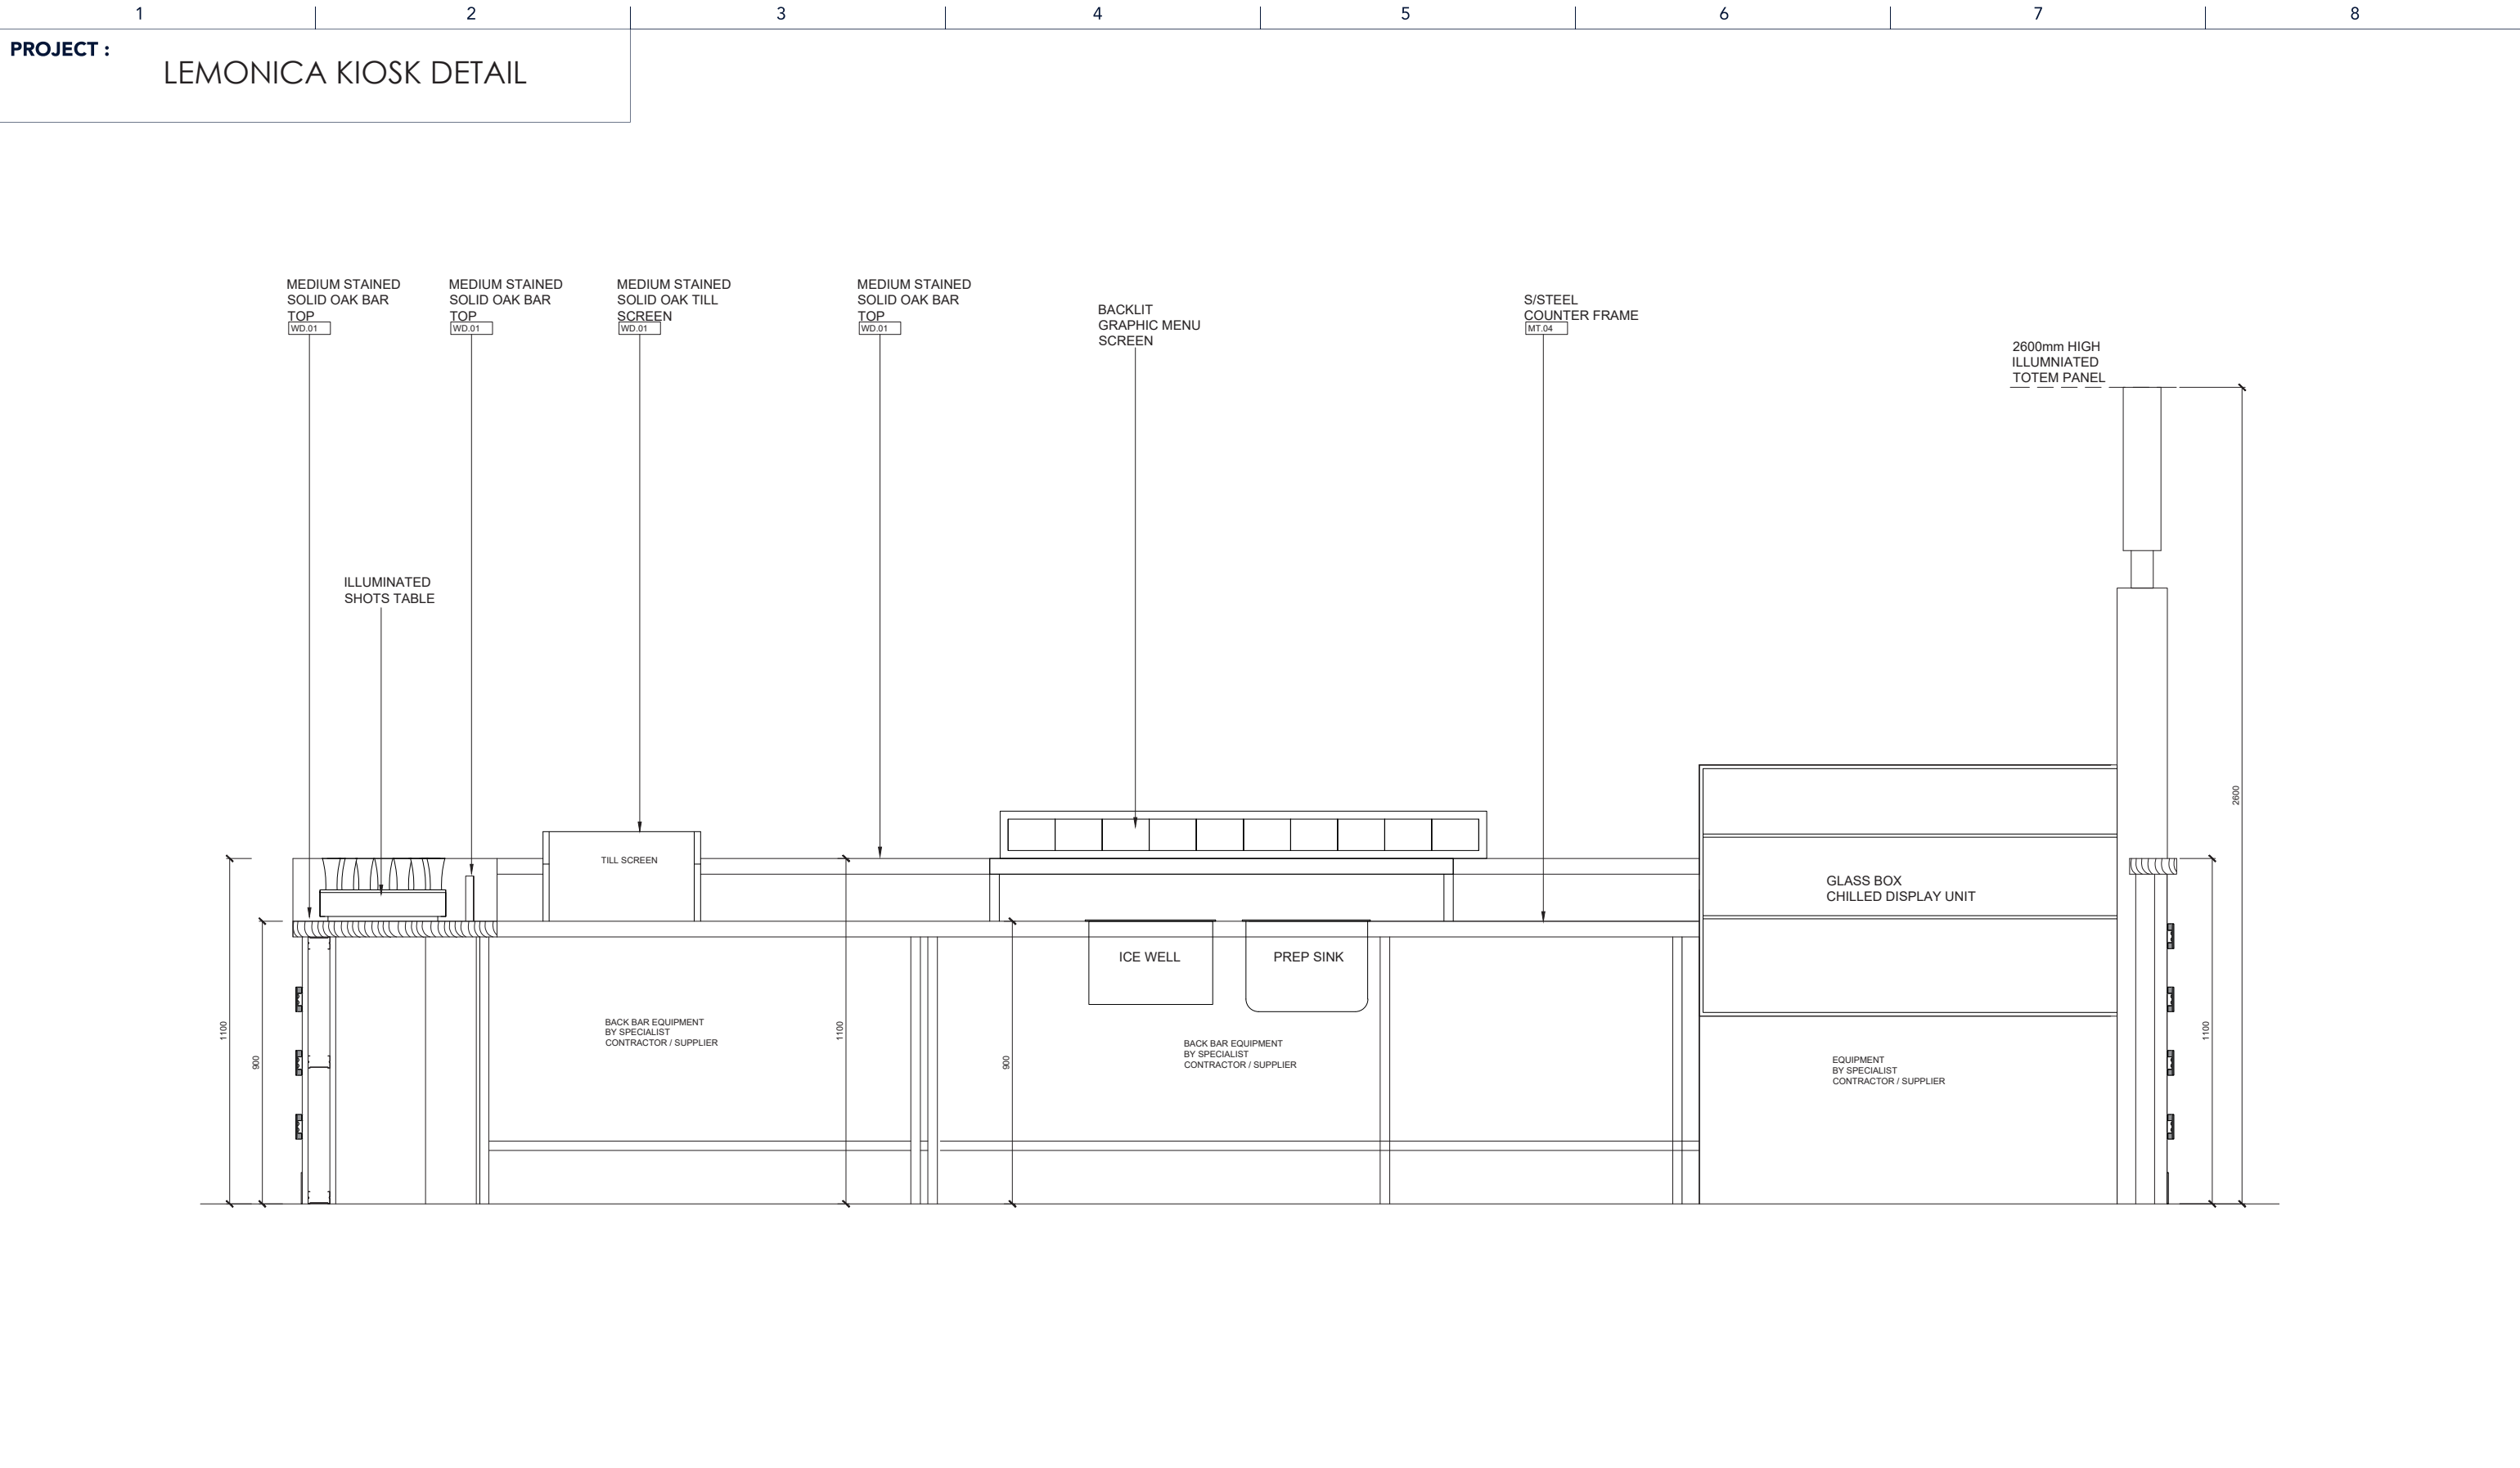

OLLYWOOD 01633 547 979 info@ollywoodservices.co.uk Unit 19B Springvale Industrial Estate, Cwmbran, South Wales NP44 5BA		NOTES: 1 UNLESS OTHERWISE SPECIFIED DIMENSIONS ARE IN MILLIMETERS. 2 ALL INSIDE BEND RADII TO BE MINIMUM. 3 REMOVE ALL BURS AND SHARP EDGES. 4 PART TO BE MANUFACTURED FROM SEPARATE SUPPLIED CAD FILE. 5 DRAWING IS FOR REFERENCE ONLY, ACTUAL DRAWINGS SUPPLIED FROM 3D ELECTRONIC DATABASE. 6 DO NOT SCALE DRAWING.		CLIENT : LEMONICA		DRAWING TITLE :		
				PROJECT : LEMONICA WESTFIELD KIOSK DETAIL		SUMMARY :		
				JOB NO :	NAME	SIGNATURE	DATE	DRAWING NO : REVISIONA MATERIAL :
				DRAWN BY :	JR		17/04/2024	PROCESS :FINISH :
				CHECKED BY :				SCALE :PAGE SIZE :A3

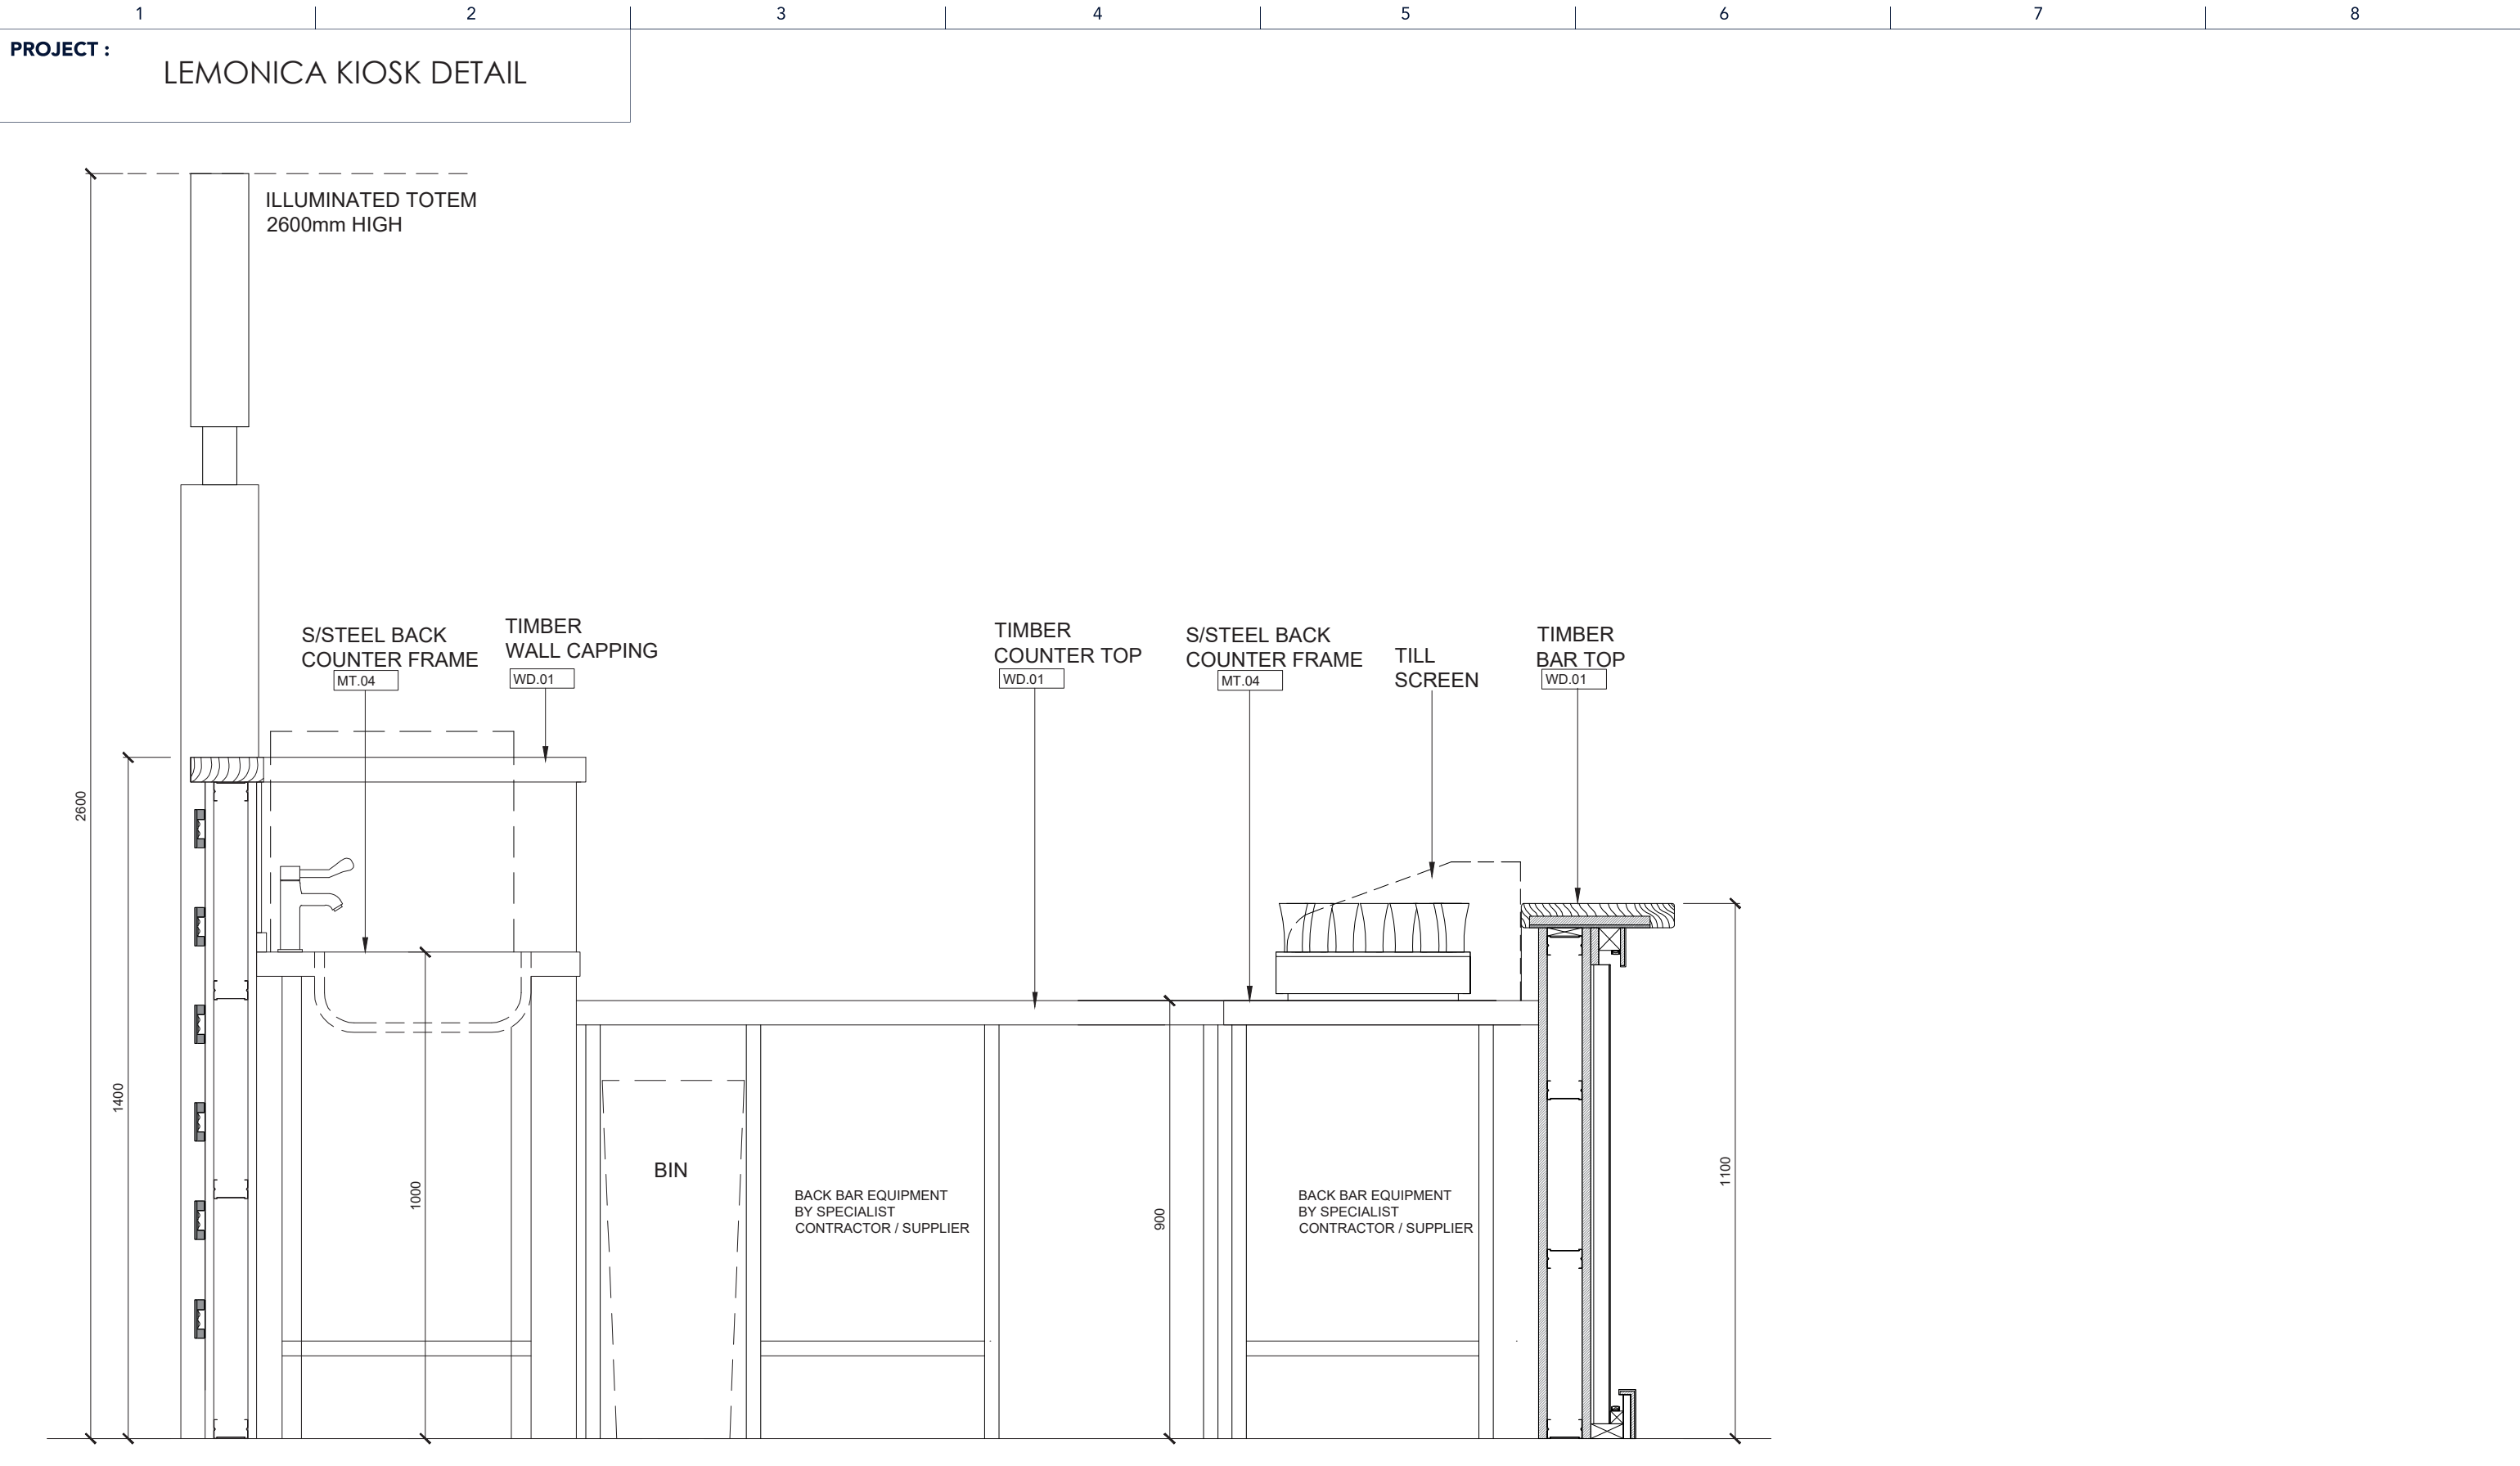

OLLYWOOD

01633 547 979 | info@ollywoodservices.co.uk

Unit 19B Springvale Industrial Estate, Cwmbran, South Wales NP44 5BA

NOTES:

1 UNLESS OTHERWISE SPECIFIED DIMENSIONS ARE IN MILLIMETERS.

2 ALL INSIDE BEND RADII TO BE MINIMUM.

3 REMOVE ALL BURS AND SHARP EDGES.

4 PART TO BE MANUFACTURED FROM SEPARATE SUPPLIED CAD FILE.

5 DRAWING IS FOR REFERENCE ONLY, ACTUAL DRAWINGS SUPPLIED FROM 3D ELECTRONIC DATABASE.

6 DO NOT SCALE DRAWING.

THIS DRAWING IS THE PROPERTY OF OLLYWOOD SERVICES AND IS PROTECTED.

IT MAY NOT BE DISTRIBUTED OR USED IN ANY FORM WITHOUT WRITTEN PERMISSION.

CLIENT : LEMONICA

PROJECT : LEMONICA WESTFIELD KIOSK DETAIL

JOB NO :

NAME

SIGNATURE

DATE

DRAWN BY :

JR

17/04/2024

CHECKED BY :

DRAWING TITLE :

SUMMARY :

DRAWING NO :

REVISION

MATERIAL :

PROCESS :


FINISH :

SCALE :

PAGE SIZE :


A3

PROJECT : LEMONICA KIOSK DETAIL

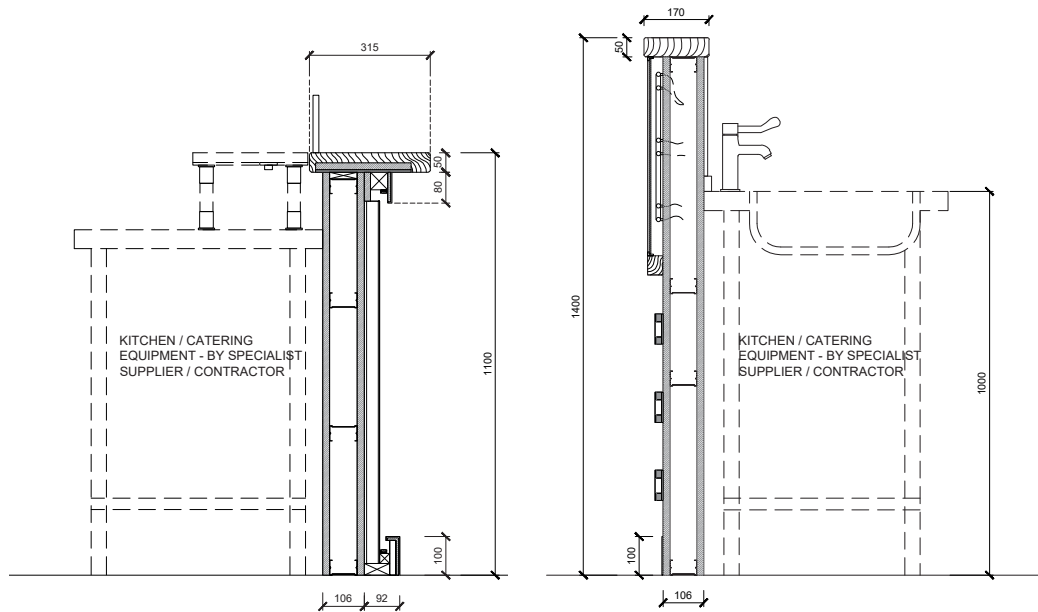


SECTION A
SCALE 1:20


SECTION B
SCALE 1:20

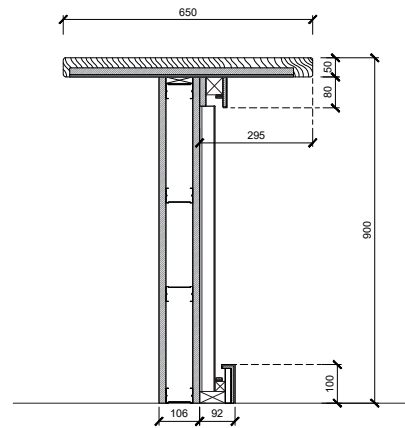


SECTION C
SCALE 1:20

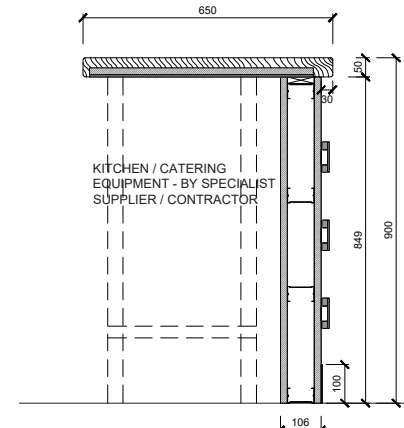

SECTION D
SCALE 1:20

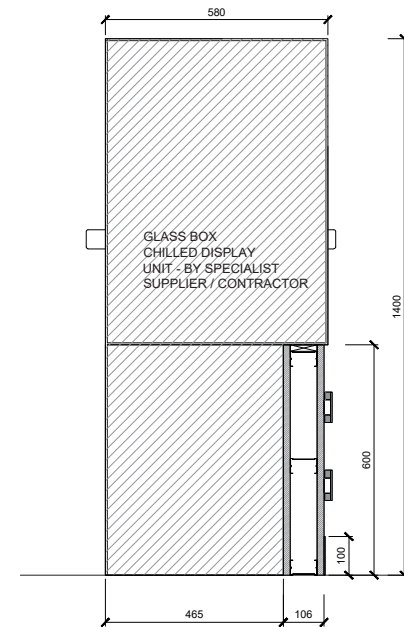

SECTION E
SCALE 1:20

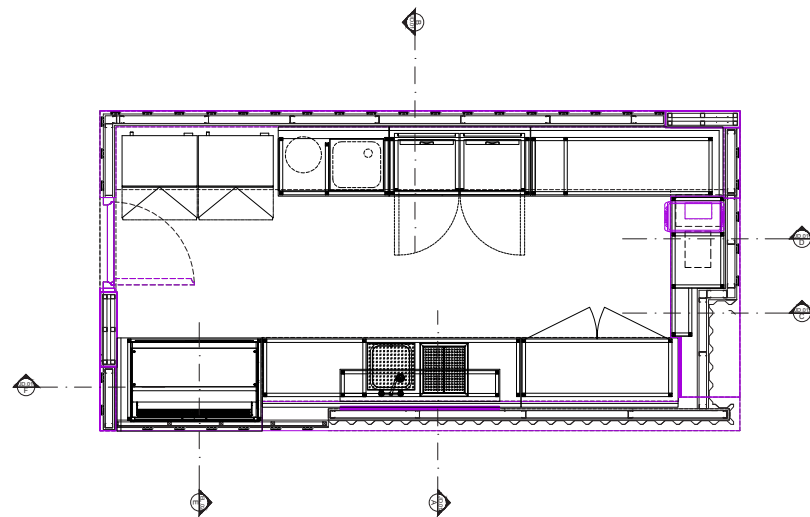

OLLYWOOD

01633 547 979 | info@ollywoodservices.co.uk
Unit 19B Springvale Industrial Estate, Cwmbran, South Wales NP44 5BA

NOTES:

- 1 UNLESS OTHERWISE SPECIFIED DIMENSIONS ARE IN MILLIMETERS.
- 2 ALL INSIDE BEND RADII TO BE MINIMUM.
- 3 REMOVE ALL BURS AND SHARP EDGES.
- 4 PART TO BE MANUFACTURED FROM SEPARATE SUPPLIED CAD FILE.
- 5 DRAWING IS FOR REFERENCE ONLY, ACTUAL DRAWINGS SUPPLIED FROM 3D ELECTRONIC DATABASE.
- 6 DO NOT SCALE DRAWING.

THIS DRAWING IS THE PROPERTY OF OLLYWOOD SERVICES AND IS PROTECTED.
IT MAY NOT BE DISTRIBUTED OR USED IN ANY FORM WITHOUT WRITTEN PERMISSION.

CLIENT : LEMONICA

PROJECT : LEMONICA WESTFIELD KIOSK DETAIL

JOB NO :

NAME

SIGNATURE

DATE

DRAWN BY :

JR

17/04/2024

CHECKED BY :

DRAWING TITLE :

SUMMARY :

DRAWING NO :

REVISION
A

MATERIAL :


PROCESS :

FINISH :



SCALE :



PAGE SIZE :
A3

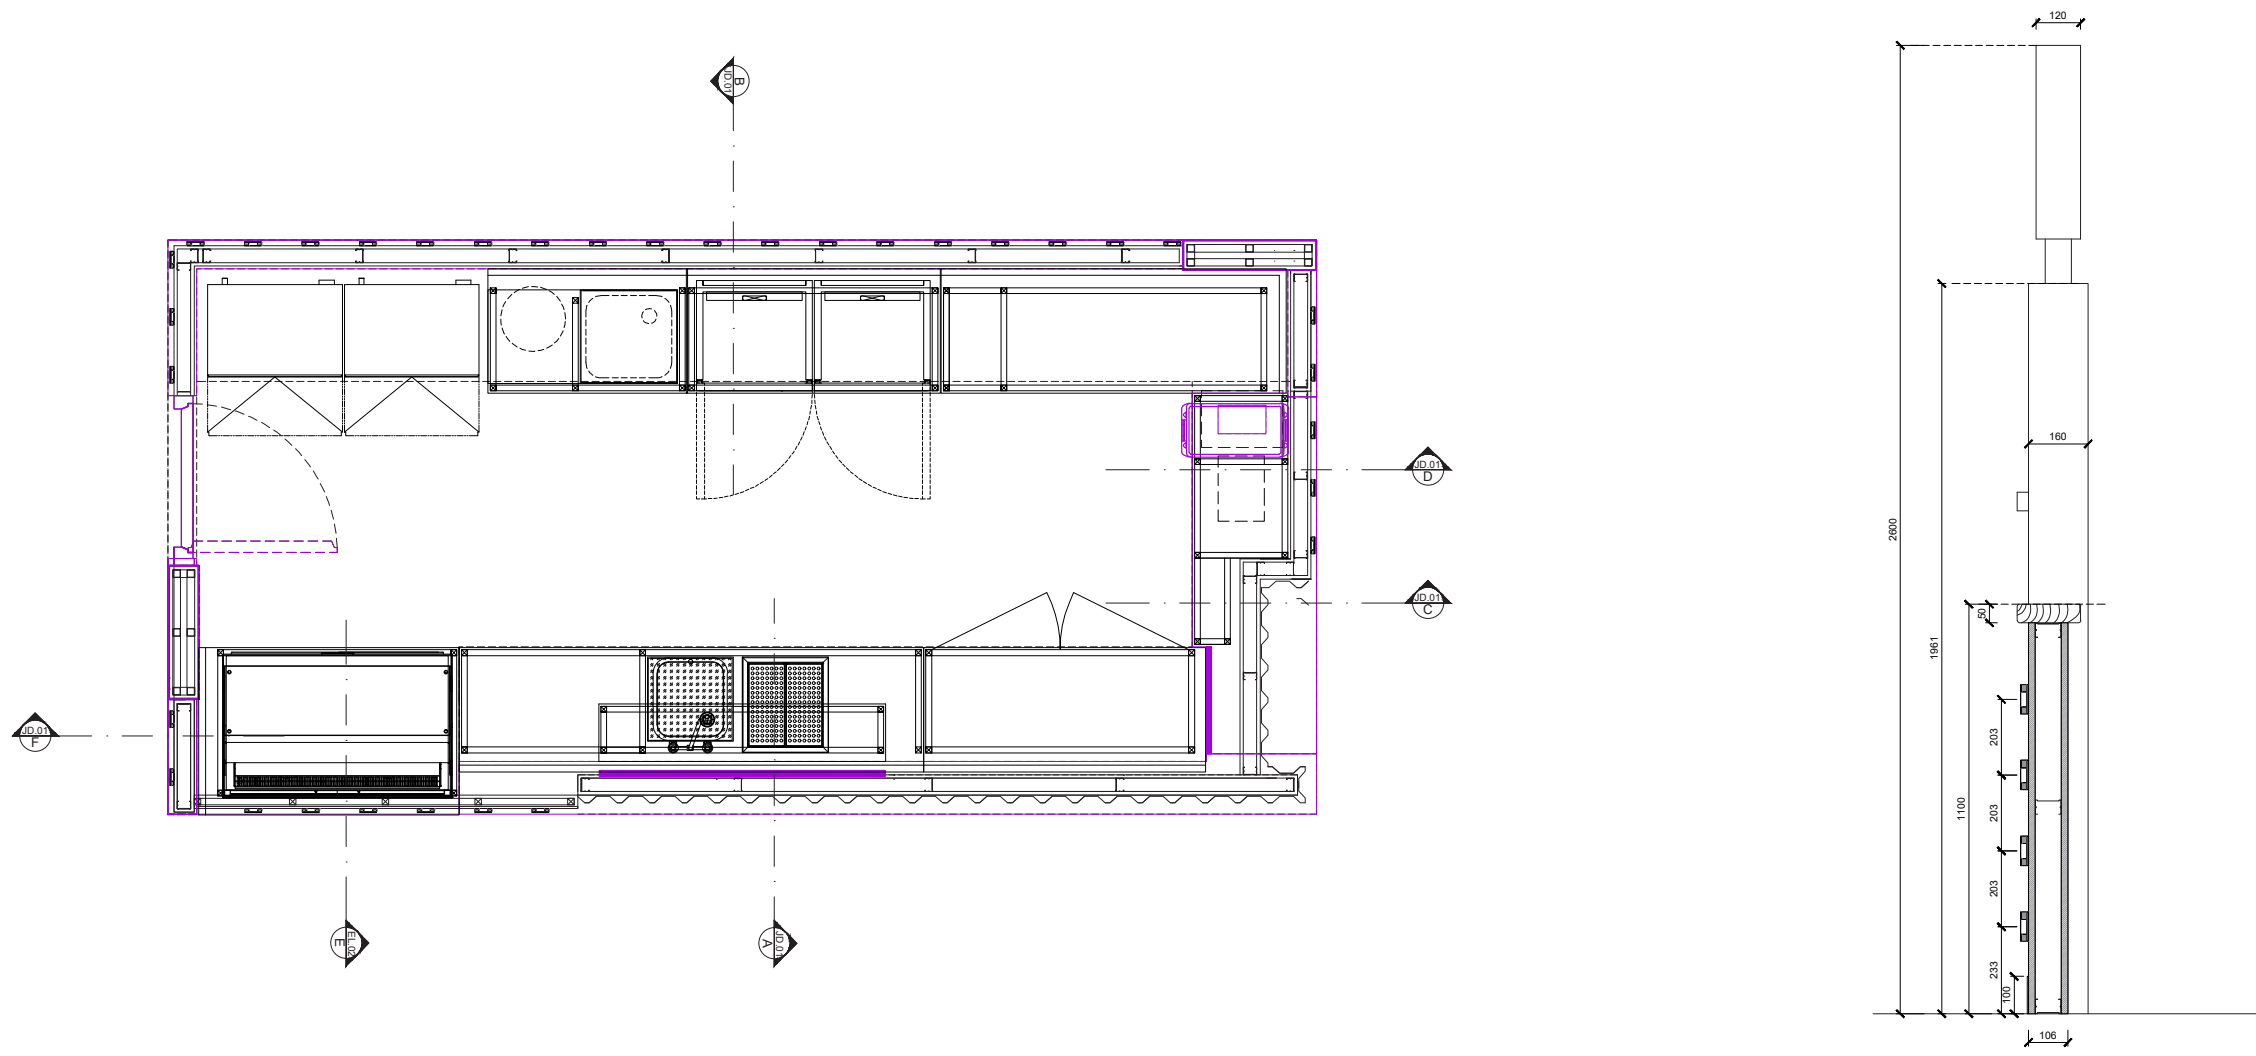

SECTION F
SCALE 1:20

OLLYWOOD 01633 547 979 info@ollywoodservices.co.uk Unit 19B Springvale Industrial Estate, Cwmbran, South Wales NP44 5BA		NOTES: 1 UNLESS OTHERWISE SPECIFIED DIMENSIONS ARE IN MILLIMETERS. 2 ALL INSIDE BEND RADII TO BE MINIMUM. 3 REMOVE ALL BURS AND SHARP EDGES. 4 PART TO BE MANUFACTURED FROM SEPARATE SUPPLIED CAD FILE. 5 DRAWING IS FOR REFERENCE ONLY, ACTUAL DRAWINGS SUPPLIED FROM 3D ELECTRONIC DATABASE. 6 DO NOT SCALE DRAWING.		CLIENT : LEMONICA		DRAWING TITLE :		
				PROJECT : LEMONICA WESTFIELD KIOSK DETAIL		SUMMARY :		
				JOB NO :	NAME	SIGNATURE	DATE	DRAWING NO : REVISIONA MATERIAL :
				DRAWN BY :	JR		17/04/2024	PROCESS : FINISH :
				CHECKED BY :				SCALE : PAGE SIZE :A3

PROJECT : LEMONICA KIOSK DETAIL

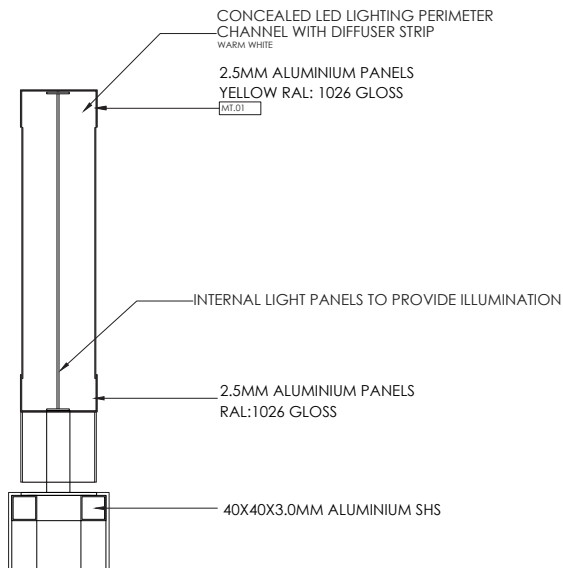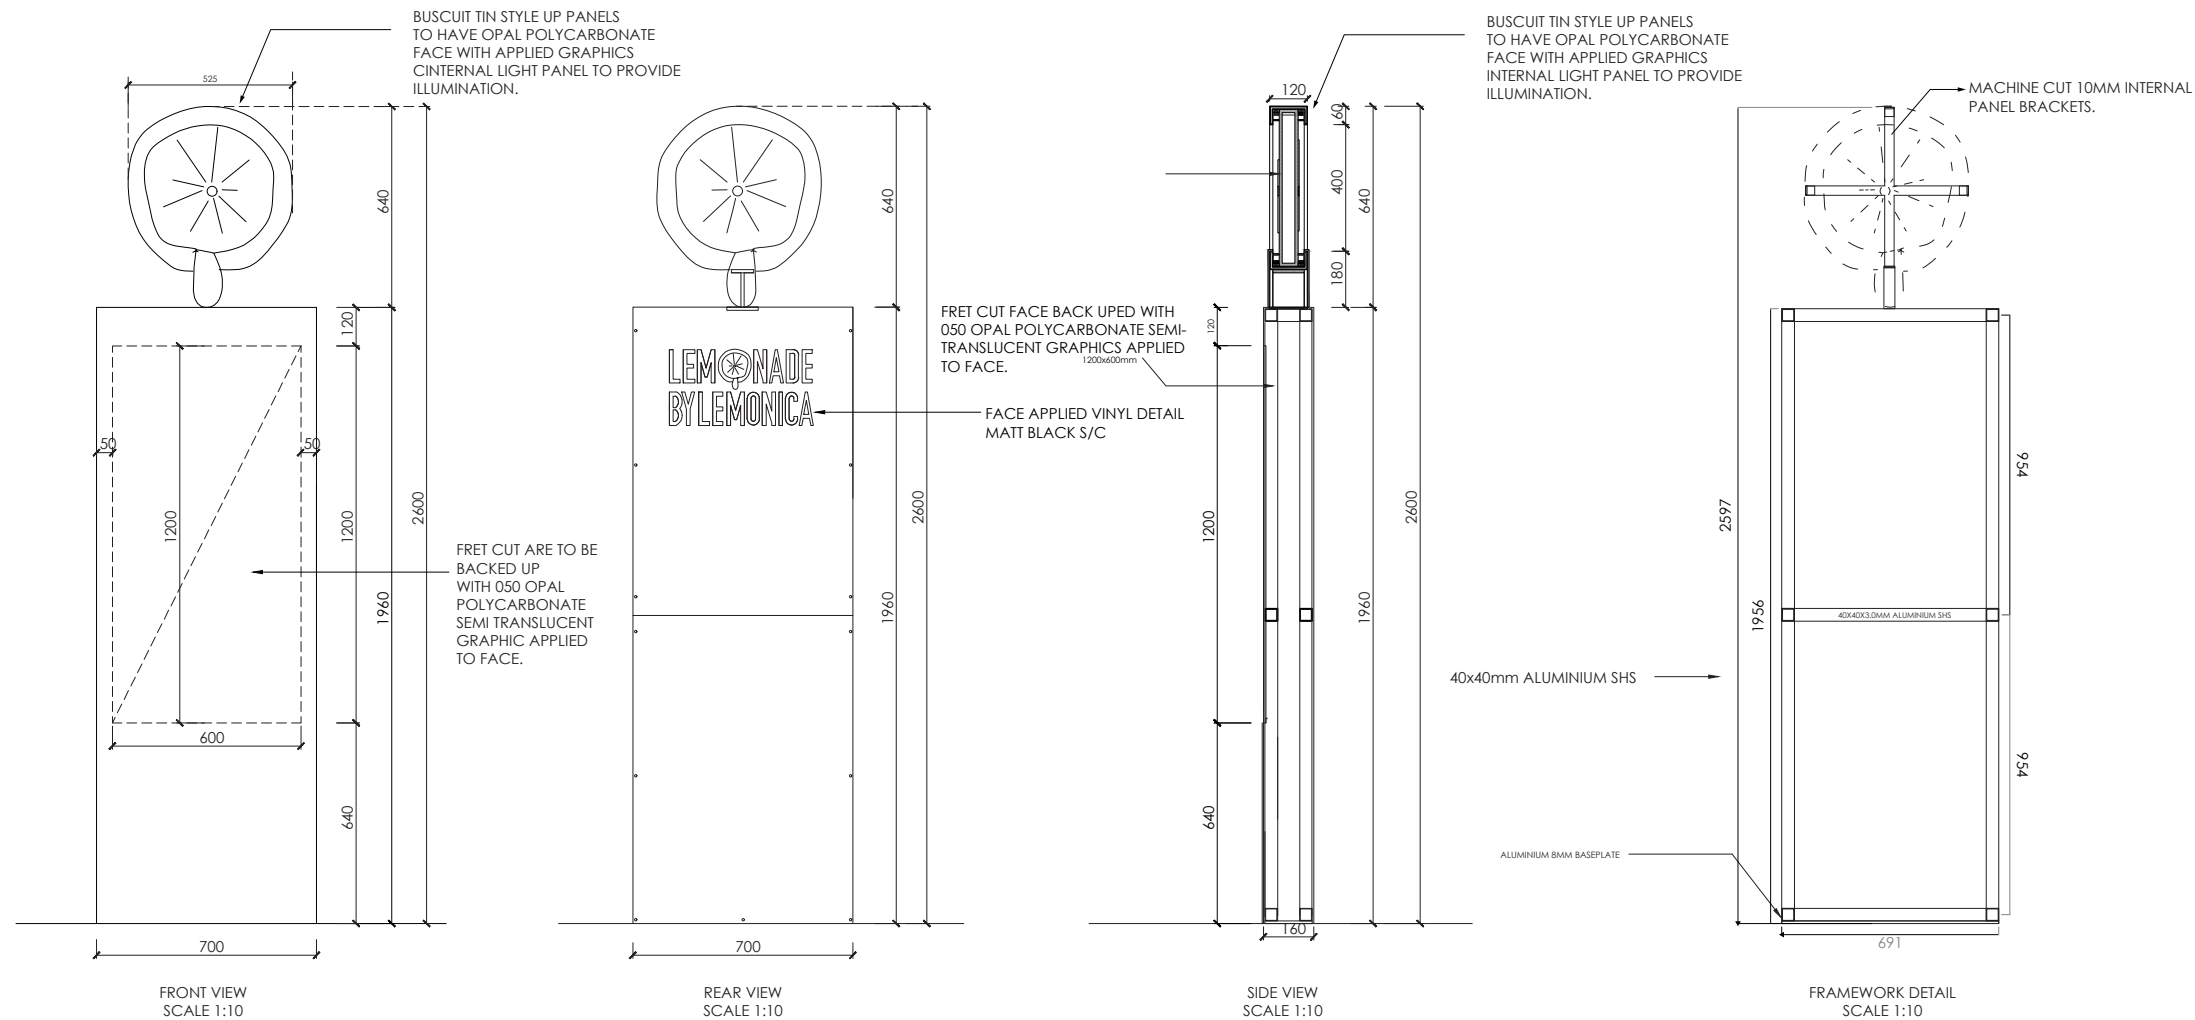

OLLYWOOD

01633 547 979 | info@ollywoodservices.co.uk
Unit 19B Springvale Industrial Estate, Cwmbran, South Wales NP44 5BA



NOTES:

- UNLESS OTHERWISE SPECIFIED DIMENSIONS ARE IN MILLIMETERS.
- ALL INSIDE BEND RADII TO BE MINIMUM.
- REMOVE ALL BURS AND SHARP EDGES.
- PART TO BE MANUFACTURED FROM SEPARATE SUPPLIED CAD FILE.
- DRAWING IS FOR REFERENCE ONLY, ACTUAL DRAWINGS SUPPLIED FROM 3D ELECTRONIC DATABASE.
- DO NOT SCALE DRAWING.

THIS DRAWING IS THE PROPERTY OF OLLYWOOD SERVICES AND IS PROTECTED.
IT MAY NOT BE DISTRIBUTED OR USED IN ANY FORM WITHOUT WRITTEN PERMISSION.

CLIENT : LEMONICA				DRAWING TITLE :			
PROJECT : LEMONICA WESTFIELD KIOSK DETAIL				SUMMARY :			
JOB NO :	NAME	SIGNATURE	DATE	DRAWING NO :	REVISION A	MATERIAL :	
DRAWN BY :	JR		17/04/2024	PROCESS :		FINISH :	
CHECKED BY :				SCALE :		PAGE SIZE : A3	

PROJECT : LEMONICA KIOSK DETAIL

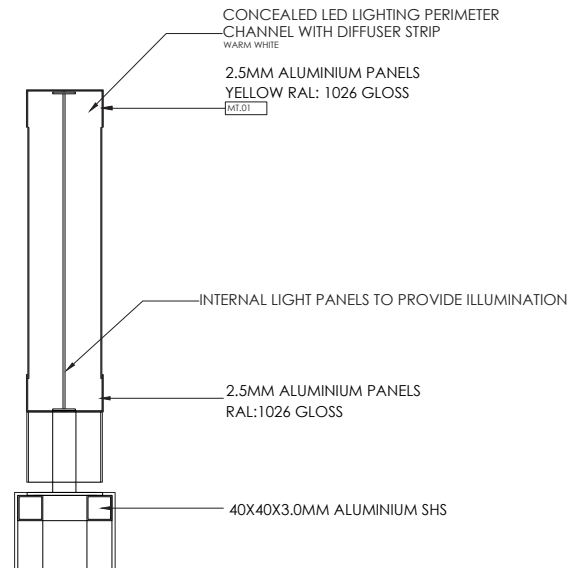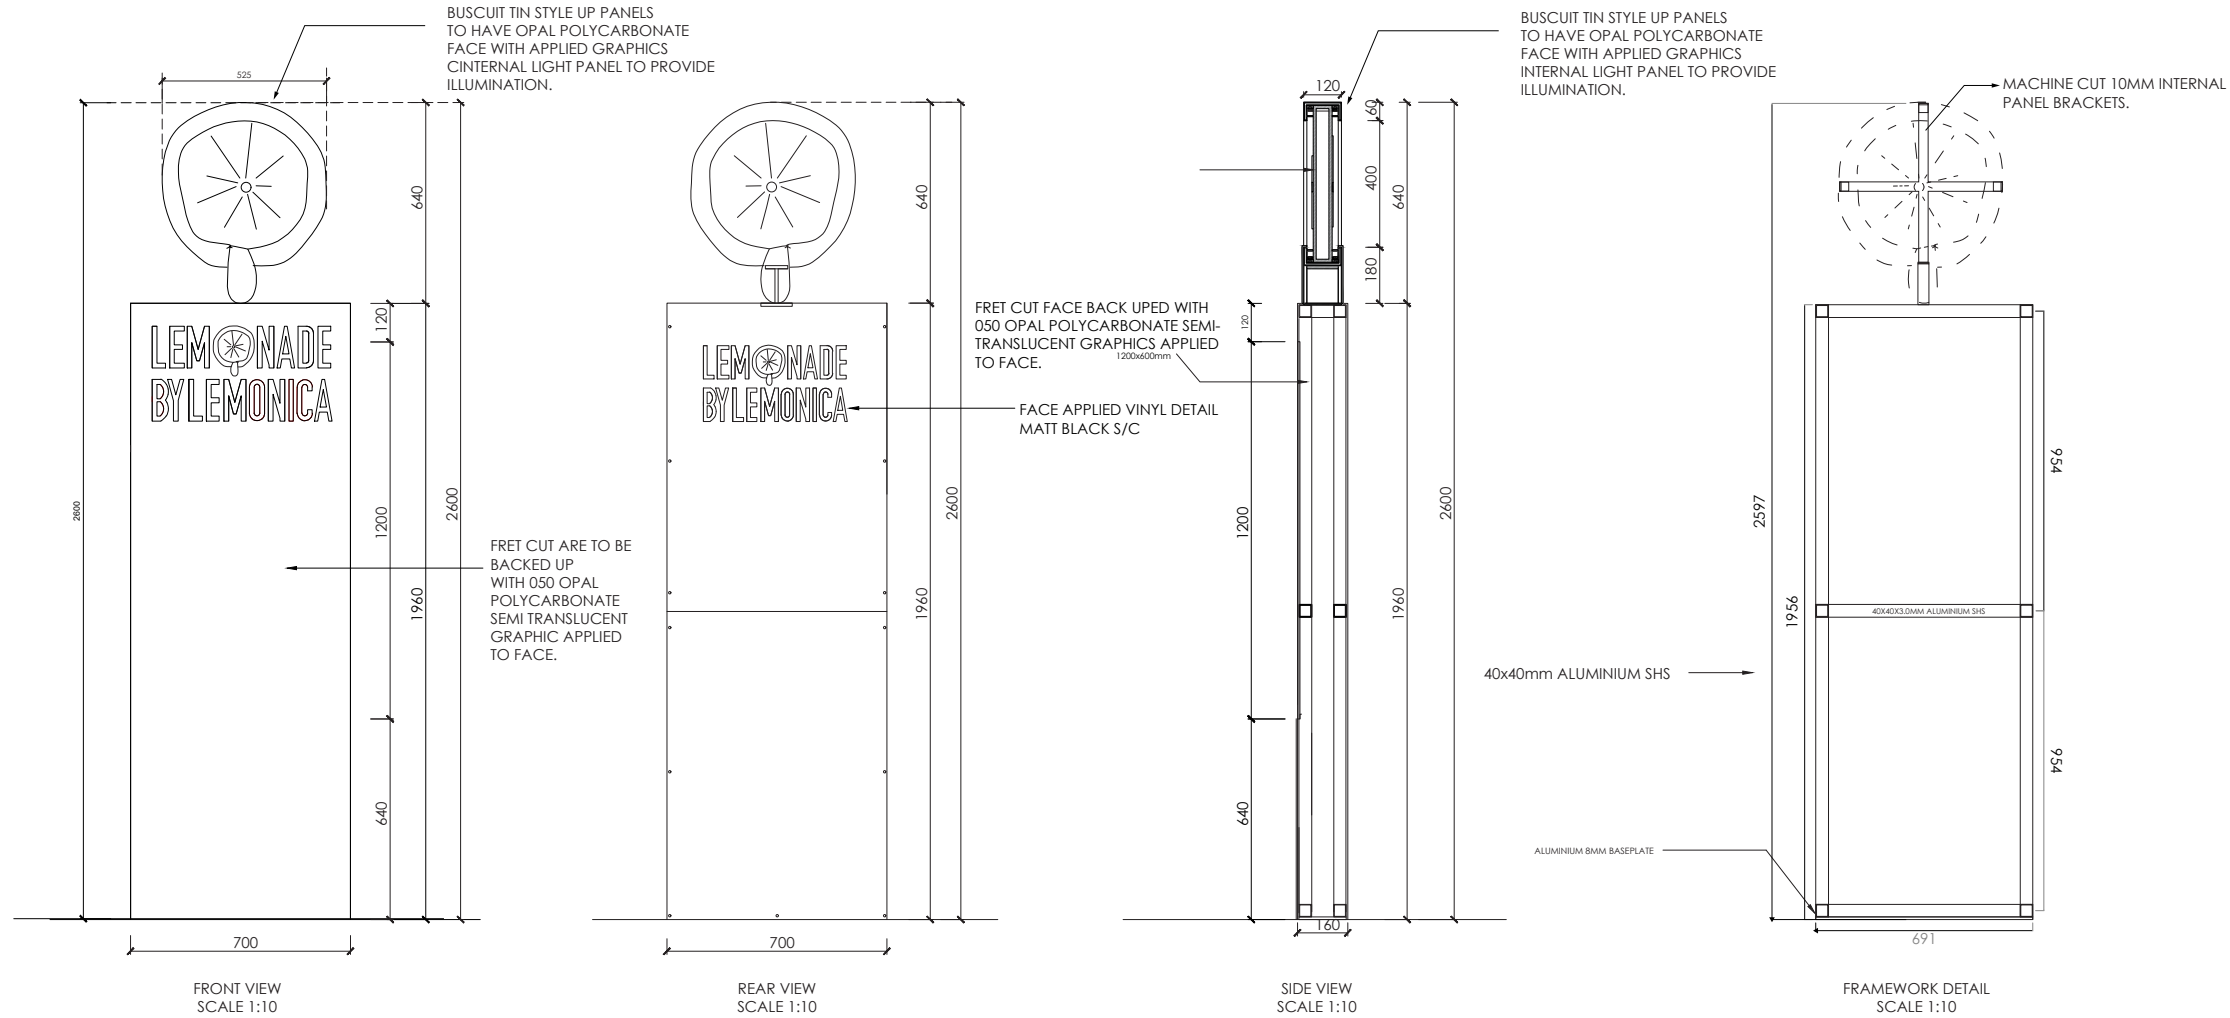

OLLYWOOD

01633 547 979 | info@ollywoodservices.co.uk
Unit 19B Springvale Industrial Estate, Cwmbran, South Wales NP44 5BA

NOTES:

- 1 UNLESS OTHERWISE SPECIFIED DIMENSIONS ARE IN MILLIMETERS.
- 2 ALL INSIDE BEND RADII TO BE MINIMUM.
- 3 REMOVE ALL BURS AND SHARP EDGES.
- 4 PART TO BE MANUFACTURED FROM SEPARATE SUPPLIED CAD FILE.
- 5 DRAWING IS FOR REFERENCE ONLY, ACTUAL DRAWINGS SUPPLIED FROM 3D ELECTRONIC DATABASE.
- 6 DO NOT SCALE DRAWING.

THIS DRAWING IS THE PROPERTY OF OLLYWOOD SERVICES AND IS PROTECTED.
IT MAY NOT BE DISTRIBUTED OR USED IN ANY FORM WITHOUT WRITTEN PERMISSION.

CLIENT : LEMONICA

PROJECT : LEMONICA WESTFIELD KIOSK DETAIL

JOB NO :

NAME

SIGNATURE

DATE

DRAWN BY :

JR

17/04/2024

CHECKED BY :

DRAWING TITLE :

SUMMARY :

DRAWING NO :

REVISION
A

MATERIAL :

PROCESS :


FINISH :




SCALE :

PAGE SIZE :
A3


PROJECT : LEMONICA KIOSK DETAIL

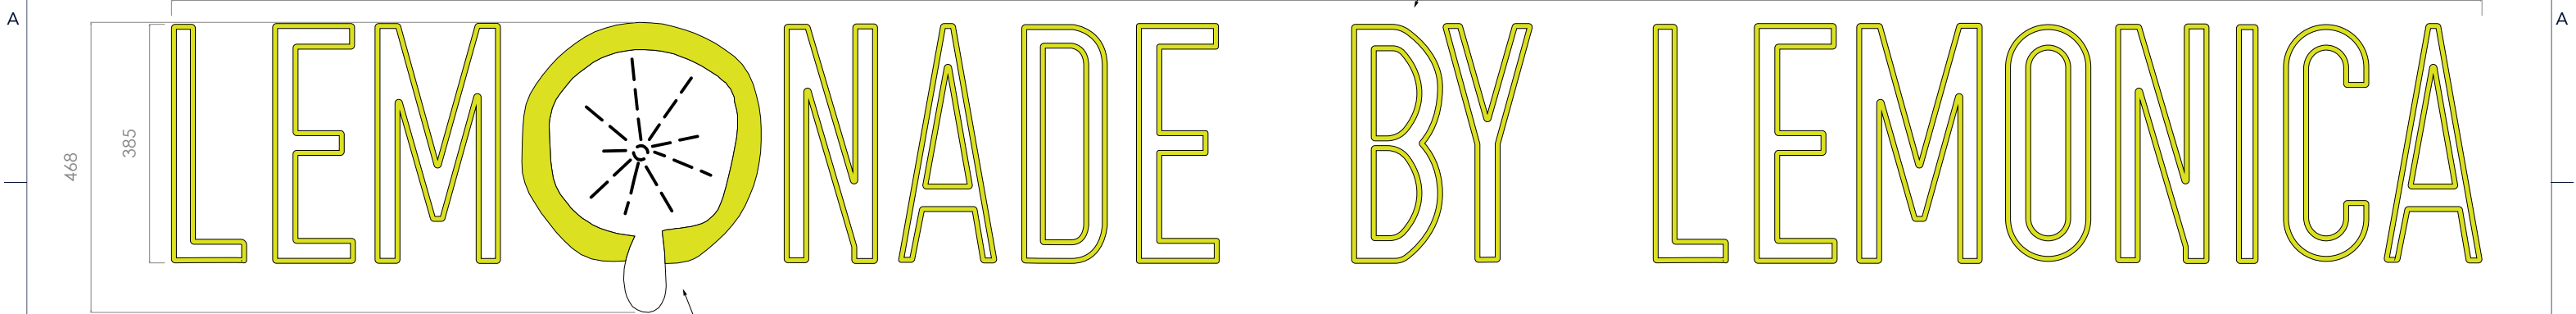


FRONT ELEVATION
SCALE 1:10

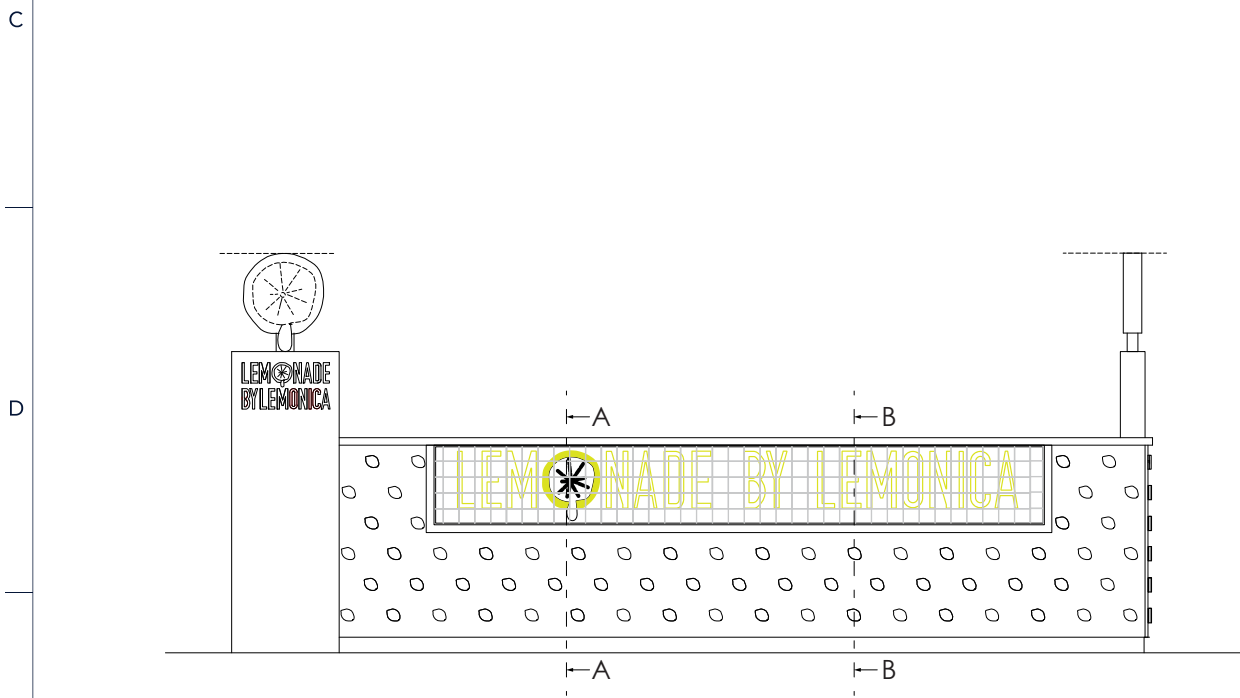

ELEVATION VIEW

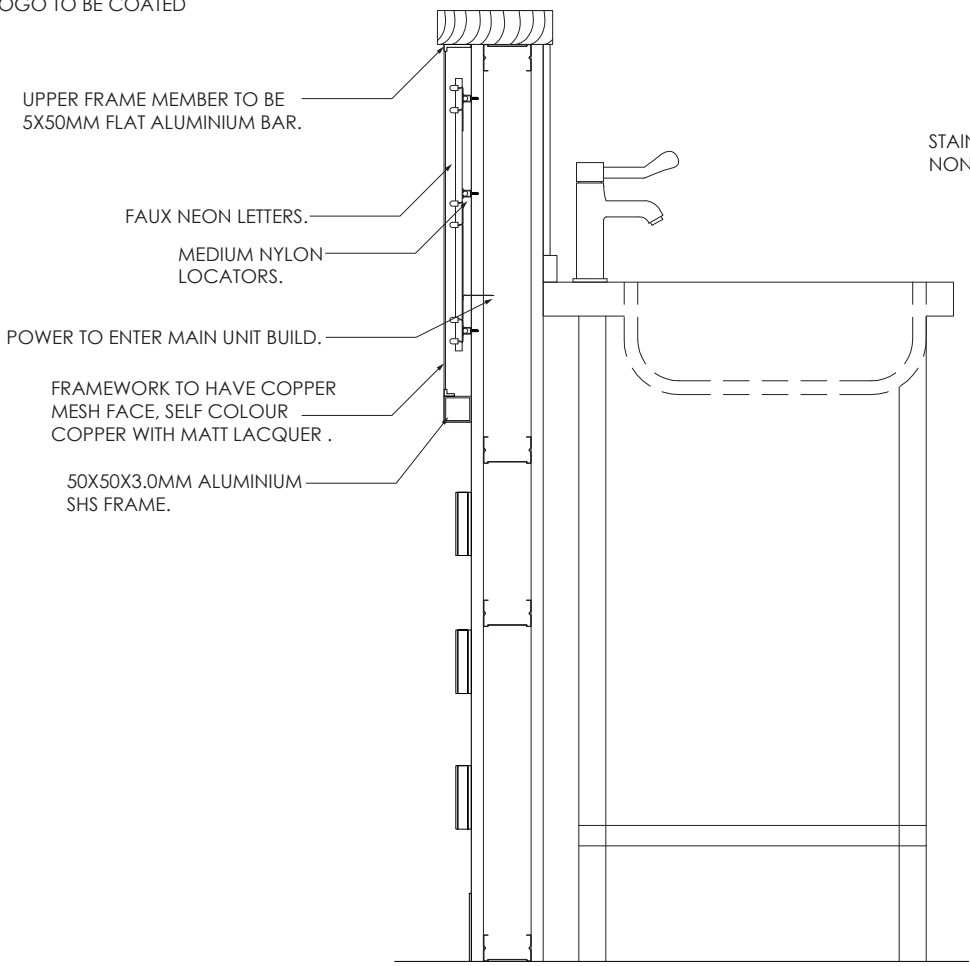

SECTION A - A

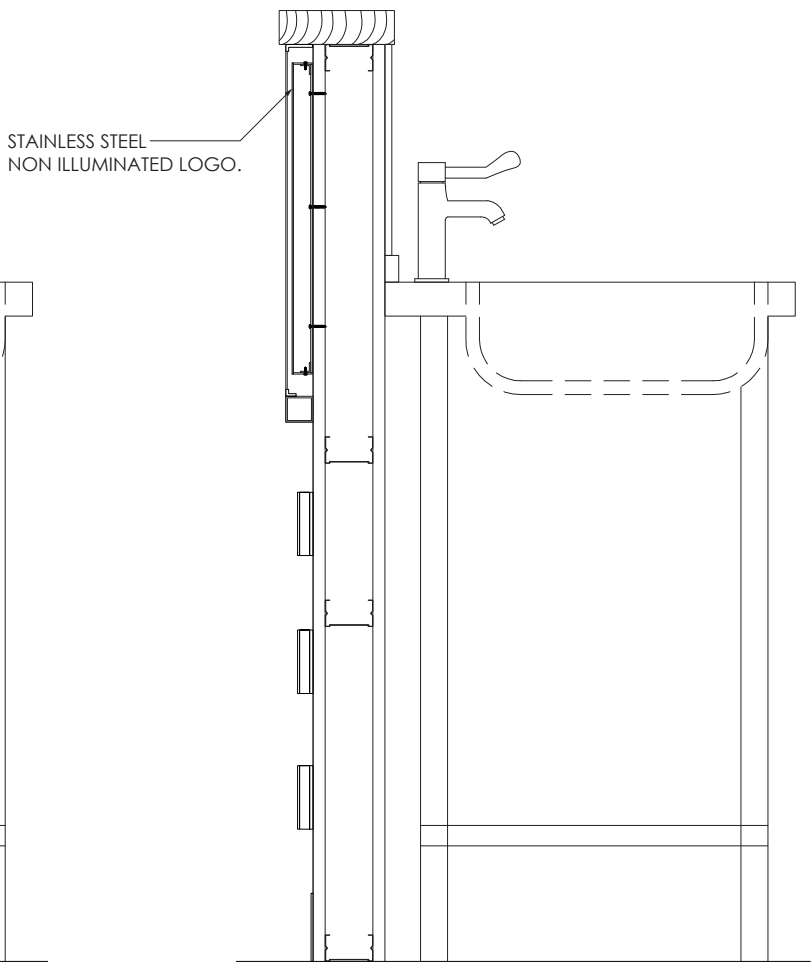

SECTION B - B

NOTES:


- 1 UNLESS OTHERWISE SPECIFIED DIMENSIONS ARE IN MILLIMETERS.
- 2 ALL INSIDE BEND RADII TO BE MINIMUM.
- 3 REMOVE ALL BURS AND SHARP EDGES.
- 4 PART TO BE MANUFACTURED FROM SEPARATE SUPPLIED CAD FILE.
- 5 DRAWING IS FOR REFERENCE ONLY, ACTUAL DRAWINGS SUPPLIED FROM 3D ELECTRONIC DATABASE.
- 6 DO NOT SCALE DRAWING.

THIS DRAWING IS THE PROPERTY OF OLLYWOOD SERVICES AND IS PROTECTED.
IT MAY NOT BE DISTRIBUTED OR USED IN ANY FORM WITHOUT WRITTEN PERMISSION.


CLIENT : LEMONICA				DRAWING TITLE :			
PROJECT : LEMONICA WESTFIELD KIOSK DETAIL				SUMMARY :			
JOB NO :	NAME	SIGNATURE	DATE	DRAWING NO :	REVISION A	MATERIAL :	
DRAWN BY :	JR		17/04/2024	PROCESS :		FINISH :	
CHECKED BY :				SCALE :		PAGE SIZE : A3	


OLLYWOOD

01633 547 979 | info@ollywoodservices.co.uk
Unit 19B Springvale Industrial Estate, Cwmbran, South Wales NP44 5BA

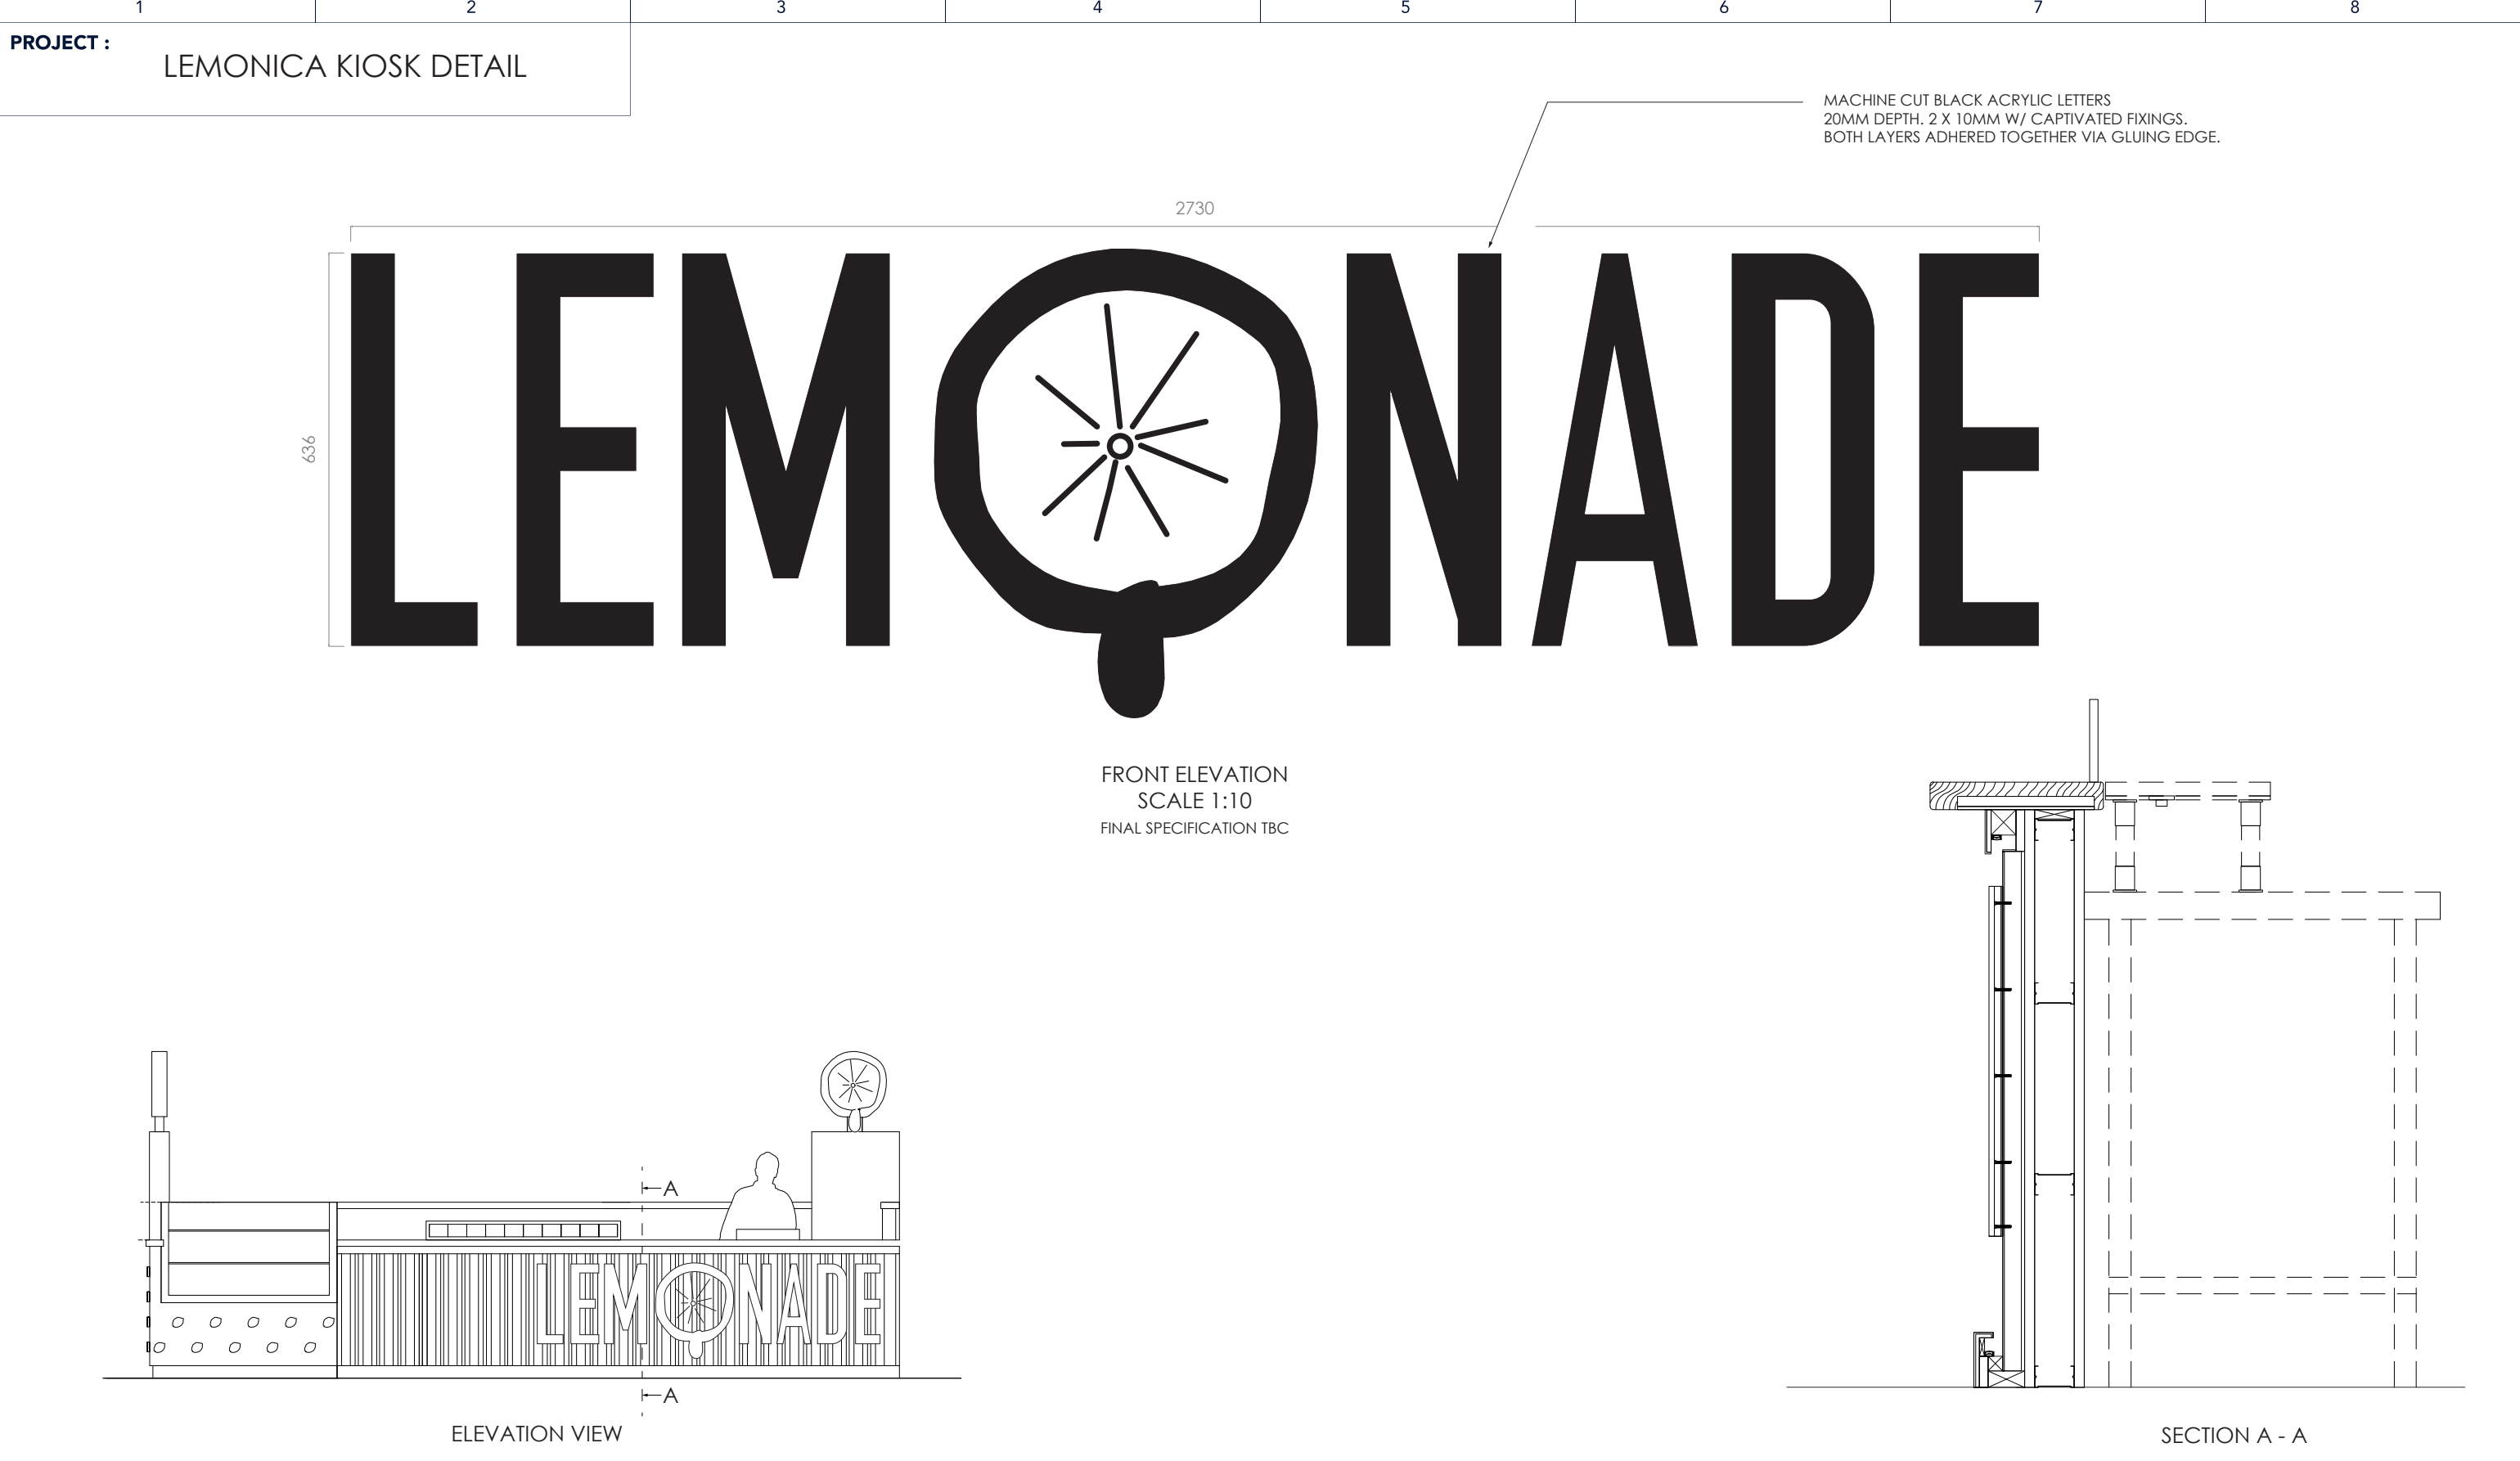

OLLYWOOD 01633 547 979 info@ollywoodservices.co.uk Unit 19B Springvale Industrial Estate, Cwmbran, South Wales NP44 5BA		NOTES: 1 UNLESS OTHERWISE SPECIFIED DIMENSIONS ARE IN MILLIMETERS. 2 ALL INSIDE BEND RADII TO BE MINIMUM. 3 REMOVE ALL BURS AND SHARP EDGES. 4 PART TO BE MANUFACTURED FROM SEPARATE SUPPLIED CAD FILE. 5 DRAWING IS FOR REFERENCE ONLY, ACTUAL DRAWINGS SUPPLIED FROM 3D ELECTRONIC DATABASE. 6 DO NOT SCALE DRAWING. THIS DRAWING IS THE PROPERTY OF OLLYWOOD SERVICES AND IS PROTECTED. IT MAY NOT BE DISTRIBUTED OR USED IN ANY FORM WITHOUT WRITTEN PERMISSION.		CLIENT : LEMONICA		DRAWING TITLE :		
				PROJECT : LEMONICA WESTFIELD KIOSK DETAIL		SUMMARY :		
				JOB NO :	NAME	SIGNATURE	DATE	DRAWING NO : REVISIONA MATERIAL :
				DRAWN BY :	JR		17/04/2024	PROCESS :FINISH :
				CHECKED BY :				SCALE :PAGE SIZE :A3

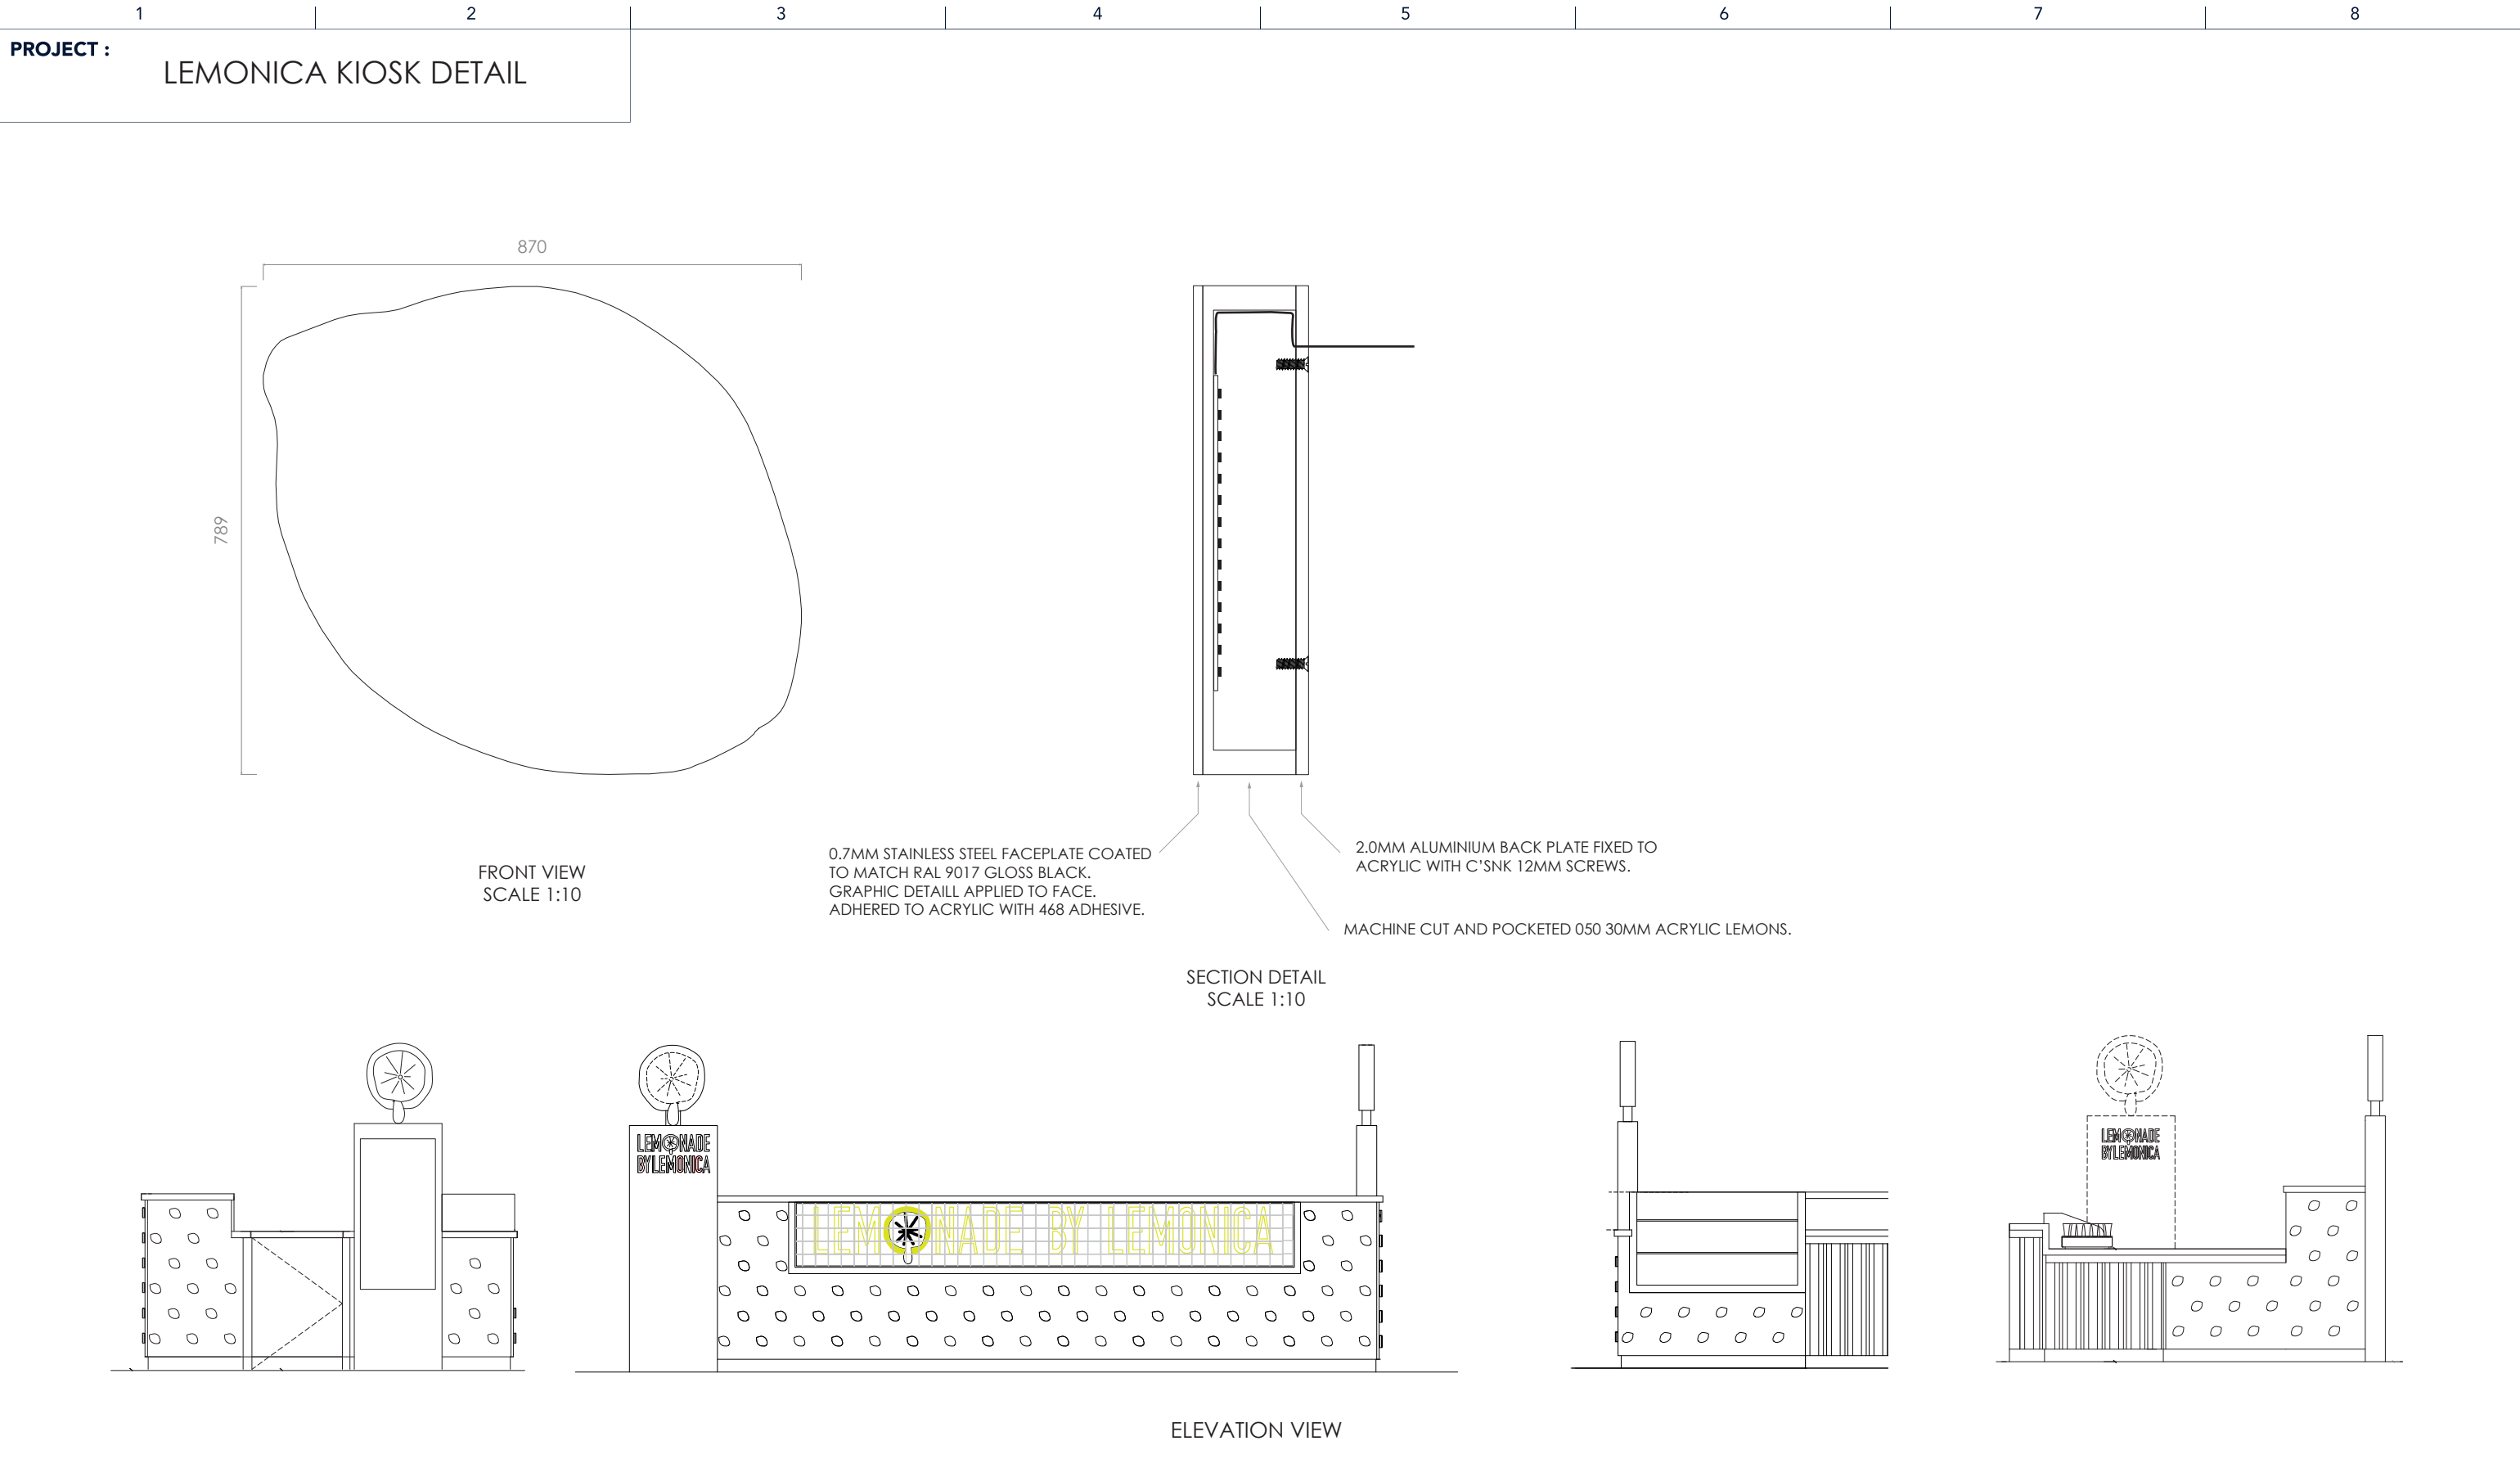

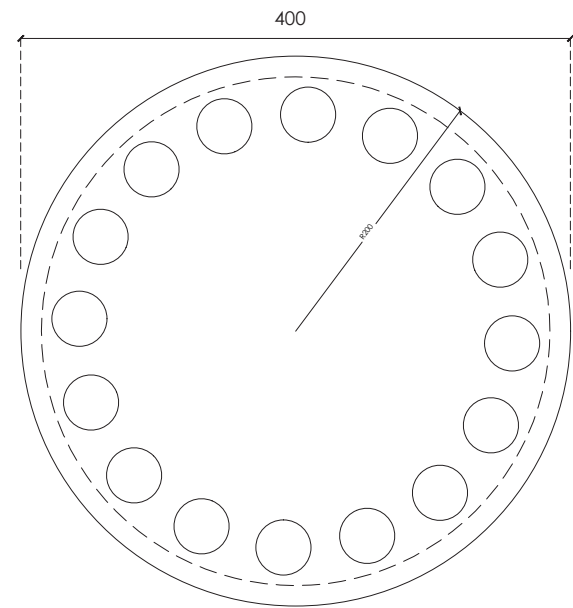

01633 547 979 | info@ollywoodservices.co.uk
Unit 19B Springvale Industrial Estate, Cwmbran, South Wales NP44 5BA

- 1 UNLESS OTHERWISE SPECIFIED DIMENSIONS ARE IN MILLIMETERS.
- 2 ALL INSIDE BEND RADII TO BE MINIMUM.
- 3 REMOVE ALL BURS AND SHARP EDGES.
- 4 PART TO BE MANUFACTURED FROM SEPARATE SUPPLIED CAD FILE.
- 5 DRAWING IS FOR REFERENCE ONLY, ACTUAL DRAWINGS SUPPLIED FROM 3D ELECTRONIC DATABASE.
- 6 DO NOT SCALE DRAWING.

THIS DRAWING IS THE PROPERTY OF OLLYWOOD SERVICES AND IS PROTECTED.
IT MAY NOT BE DISTRIBUTED OR USED IN ANY FORM WITHOUT WRITTEN PERMISSION.

CHECKED BY :

PAGE SIZE : A

A

B

C

D

E



A

B


C

D


E

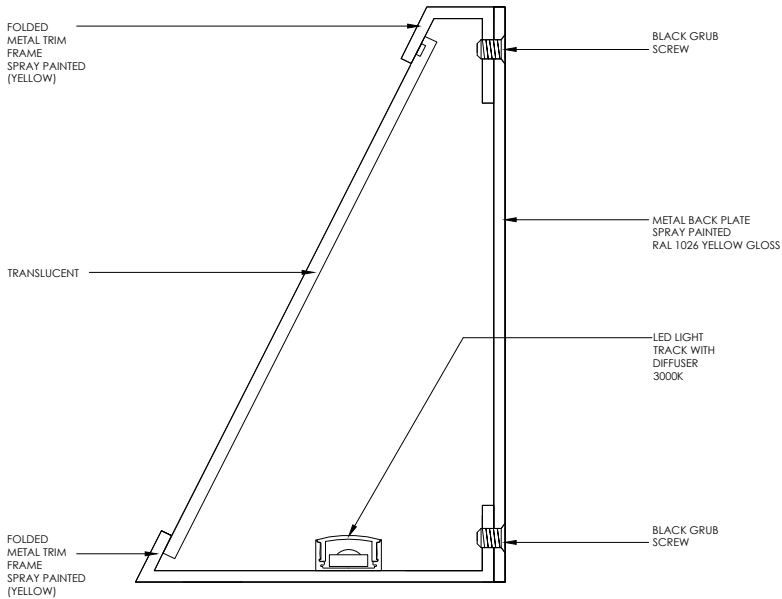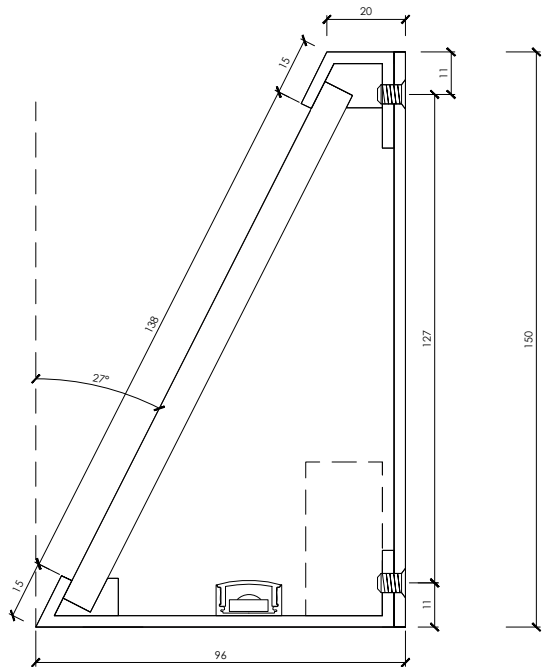

SECTION DETAIL

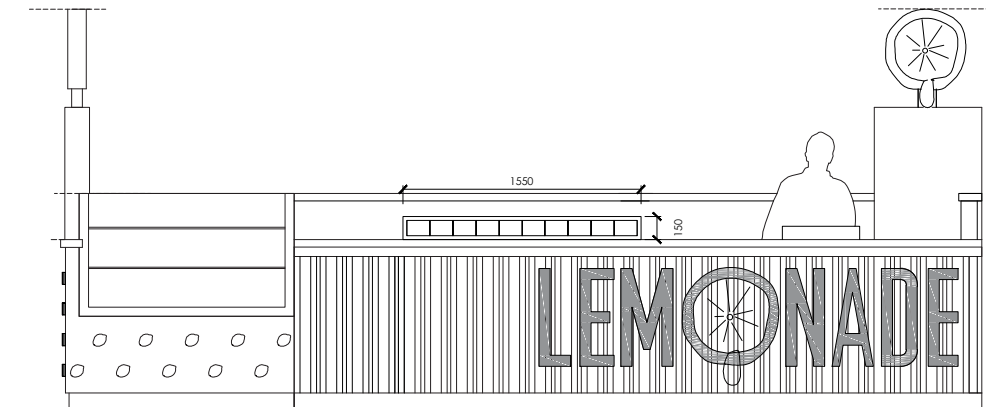

ELEVATION DETAIL

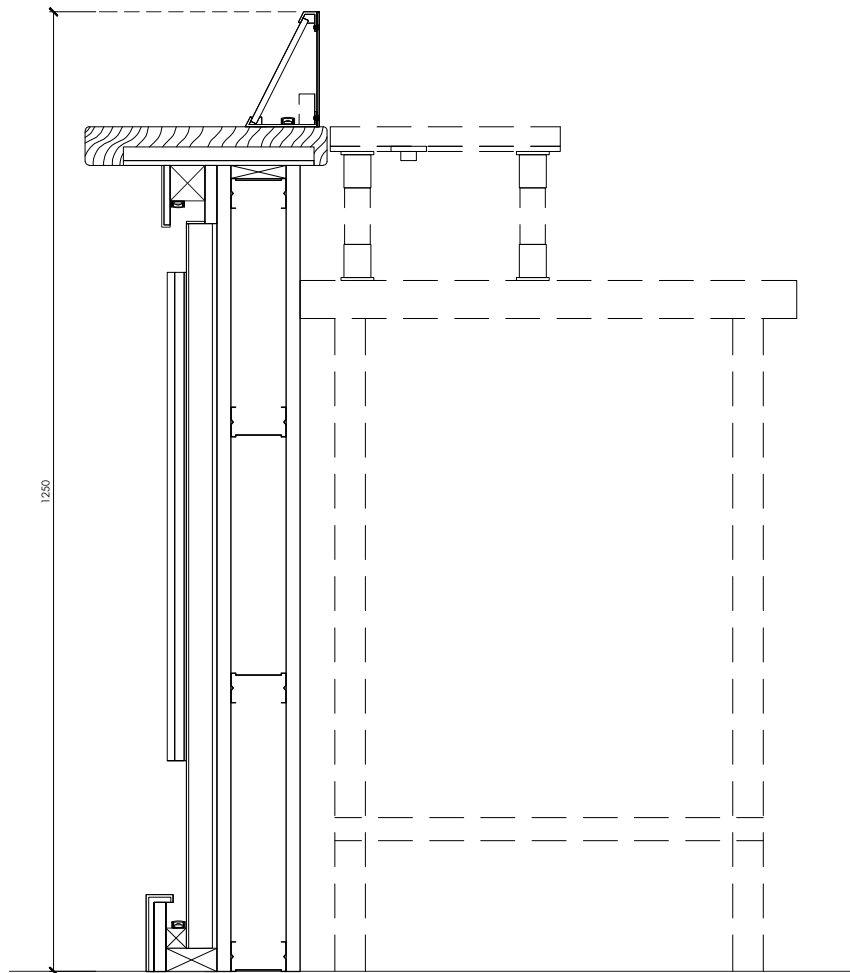

NOTES:

- 1 UNLESS OTHERWISE SPECIFIED DIMENSIONS ARE IN MILLIMETERS.
- 2 ALL INSIDE BEND RADII TO BE MINIMUM.
- 3 REMOVE ALL BURS AND SHARP EDGES.
- 4 PART TO BE MANUFACTURED FROM SEPARATE SUPPLIED CAD FILE.
- 5 DRAWING IS FOR REFERENCE ONLY, ACTUAL DRAWINGS SUPPLIED FROM 3D ELECTRONIC DATABASE.
- 6 DO NOT SCALE DRAWING.

THIS DRAWING IS THE PROPERTY OF OLLYWOOD SERVICES AND IS PROTECTED. IT MAY NOT BE DISTRIBUTED OR USED IN ANY FORM WITHOUT WRITTEN PERMISSION.

CLIENT : LEMONICA

PROJECT : LEMONICA WESTFIELD KIOSK DETAIL

JOB NO :

NAME

SIGNATURE

DATE

DRAWN BY :

JR

17/04/2024

CHECKED BY :

DRAWING TITLE :

SUMMARY :


DRAWING NO :

REVISION
A

MATERIAL :

PROCESS :

FINISH :

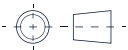

SCALE :

PAGE SIZE :

A3

OLLYWOOD

01633 547 979 | info@ollywoodservices.co.uk
Unit 19B Springvale Industrial Estate, Cwmbran, South Wales NP44 5BA