

**OVER 25 YEARS
OF MANUFACTURING
SOLUTIONS**




Retail • Exhibitions • Manufacturing • Interiors


Lemonica Kiosk

Westfield White City

Rev:	Description:
A	20/10/25 Ramp Added. Glass now pocket glazed. Totem height reduced.
B	28/10/25 Updated to comments.
C	01/12/25 Mass change to layout.
D	16/12/25 Checker plate to ramp RAL 1023.
E	21/01/26 PC removed from ramp. Door added to shelving unit. Stopping acrylic now glass.
F	27/01/26 Acrylic shroud added to slush machines.
G	

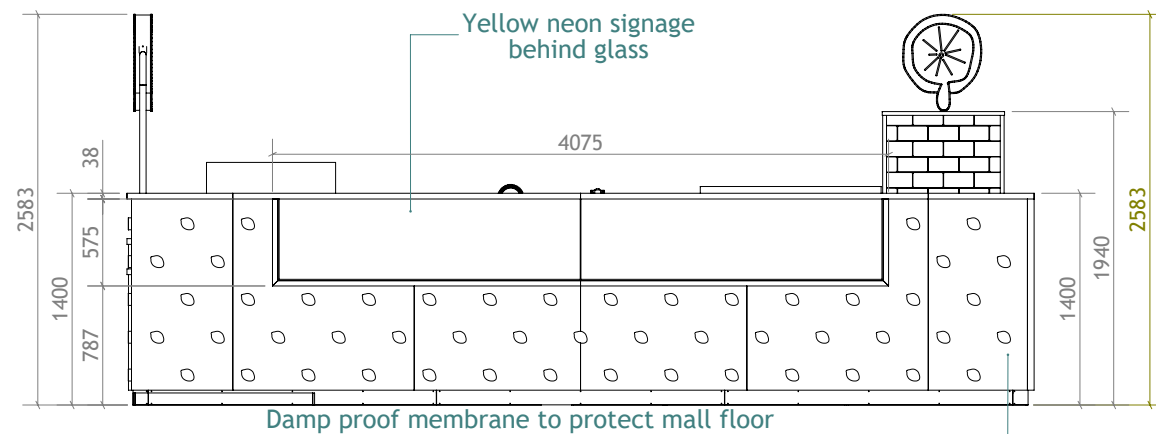

20mm black acrylic VHB taped to corrugated panels.
9.5mm toughened laminated glass in front.
Void created to be illuminated from top and bottom.

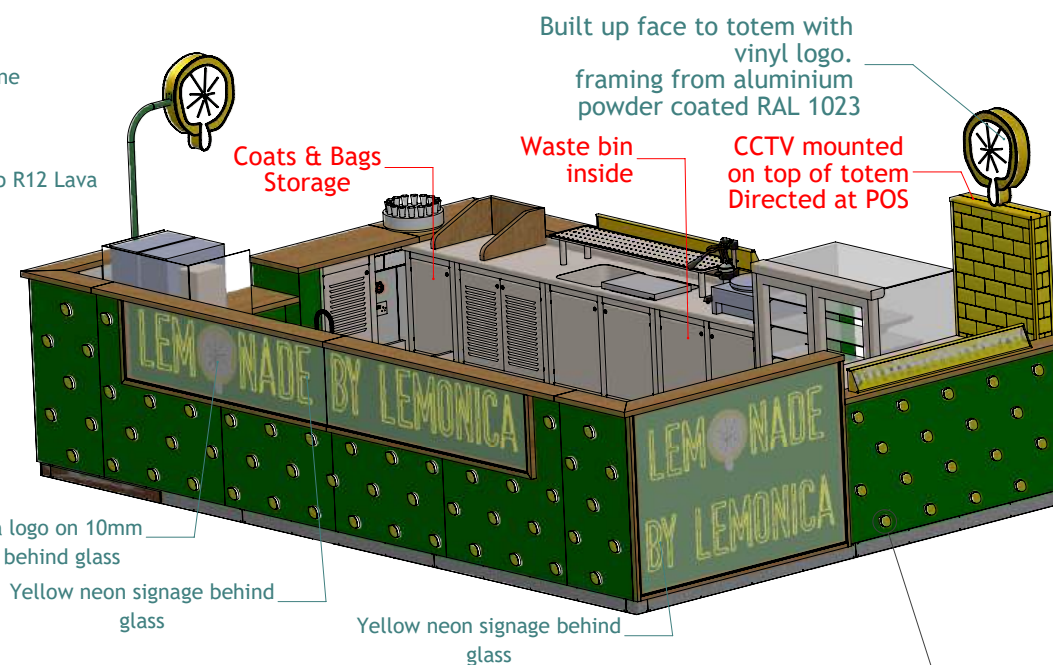


DETAIL K
SCALE 1 : 10

30mm opal acrylic cut out with bevel
- Faced with 1mm SS coated RAL 1023

External Panel

Slush Machine Shroud
Clear Acrylic

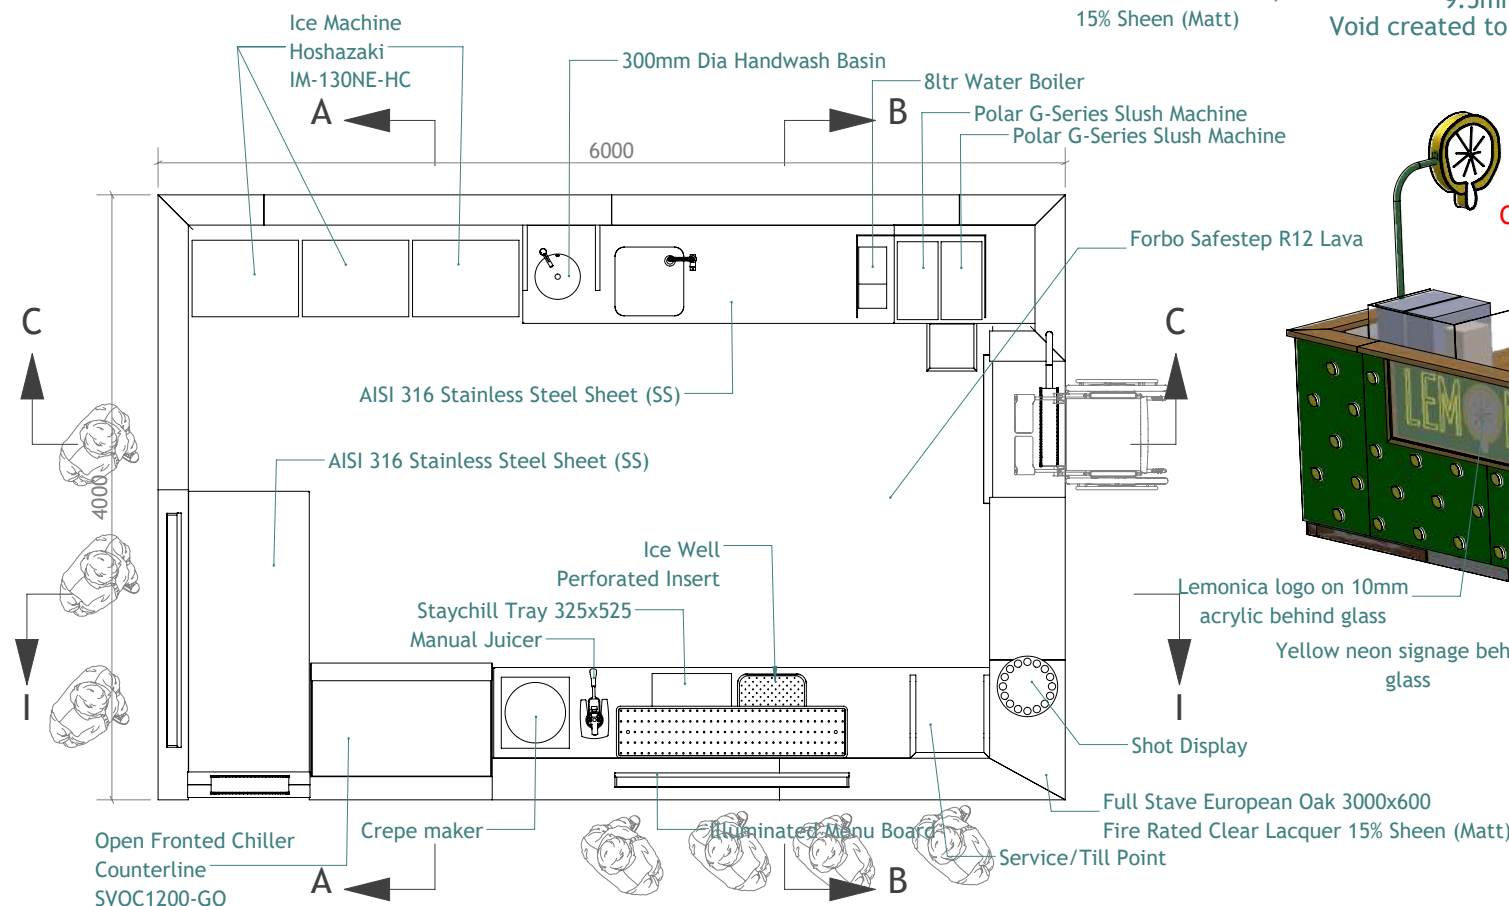

Built up face to totem with
vinyl logo.
framing from aluminium
powder coated RAL 1023

Glass Cover
In front of illuminated
graphic panel.


Full Stave European Oak 3000x600
Fire rated Clear Lacquer 15% Sheen (Matt)
Ceramic Metro Tile (White)

Shot Display

Damp proof membrane to protect mall floor

0.9mm DP1 304 Stainless Steel

9.5 (4+1.5 Clear
EVA+4)Toughened
Lam' Glass PAR

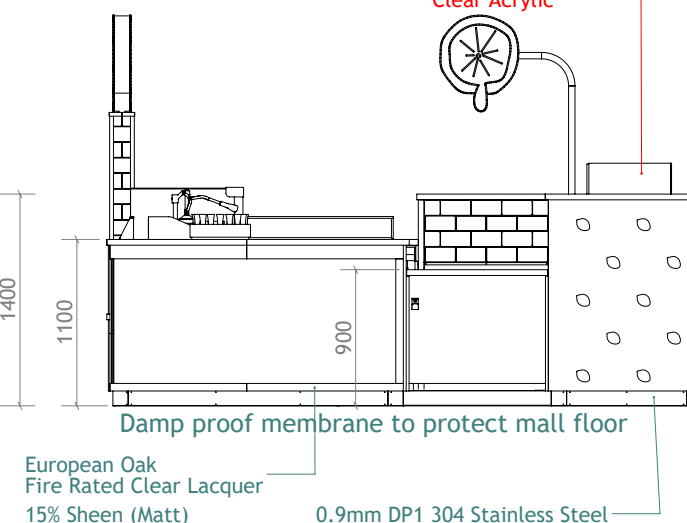

Weight of Item :- 4115.79KG



Client:
VB Interiors Ltd

Address:
Westfield, White City, London

Project:
Lemonica Kiosk

Title:
General Arrangement

Designer:
Jason Young

Date: 28/01/2026 Scale: 1:50 @ A3

Drawing No:
5271-03-00-GA



Dwg Sht: 1 of 1

Revision: F

Unit 4
Arundel Works
Claywheels Lane
Sheffield
S6 1LZ

eclipsemanufacturingsolutions.co.uk

Date Last Saved:- 27 January 2026 13:07:32

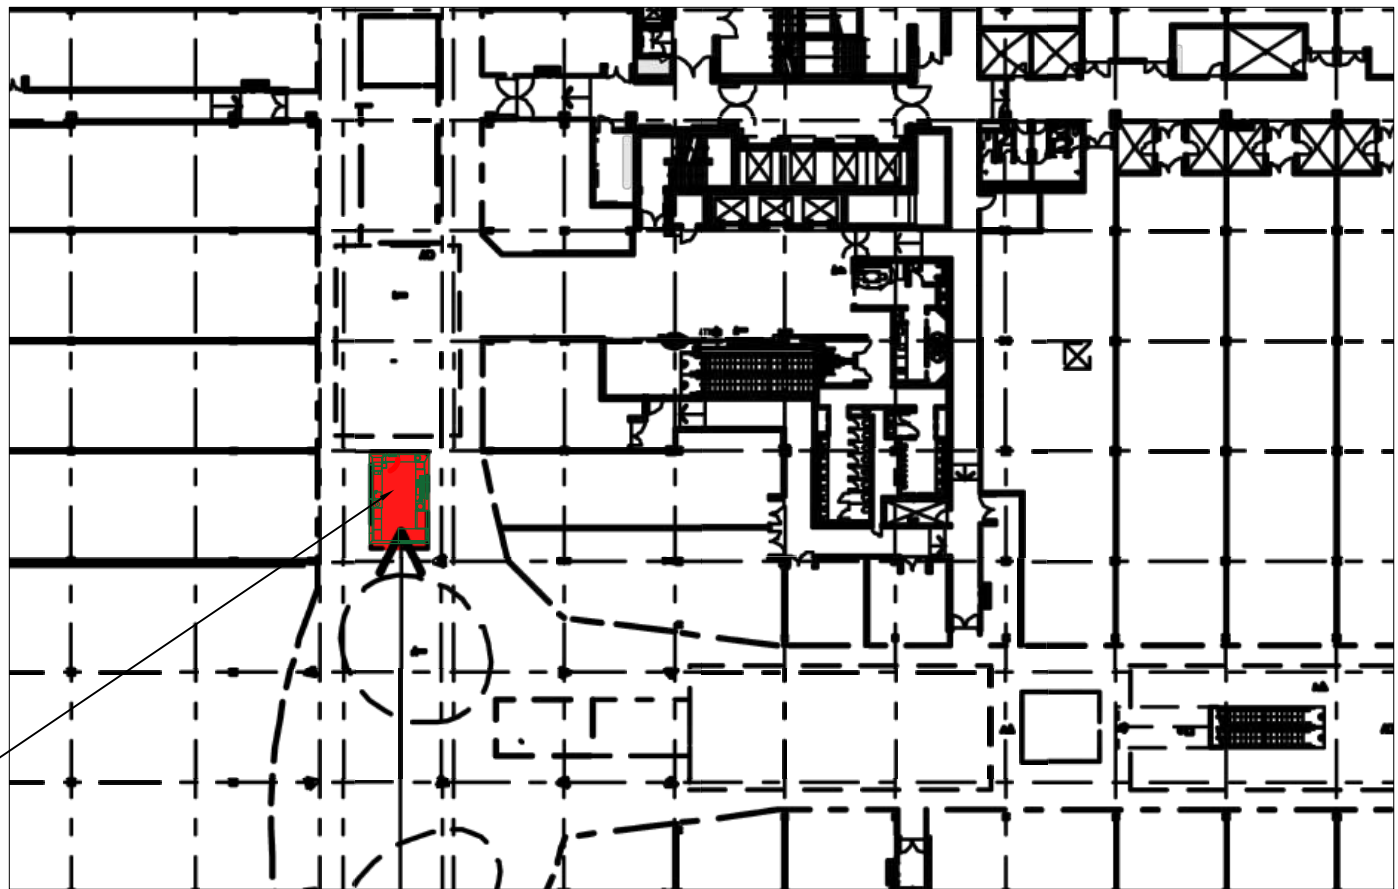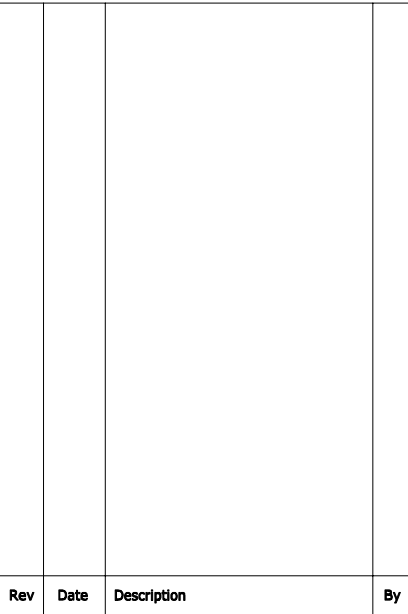

CLIENT
Lemonica


PROJECT TITLE
Mid Mall Kiosk
Westfield, White City (K1009)

DRAWING TITLE

Proposed
Location Plan

PROJECT NO.		DRAWING NO.		REV
5217		01-001		D
Scale.	Drawn by.	Sheet Size	Date.	
NTS	JY	A1	12/12/25	

Kiosk K1009

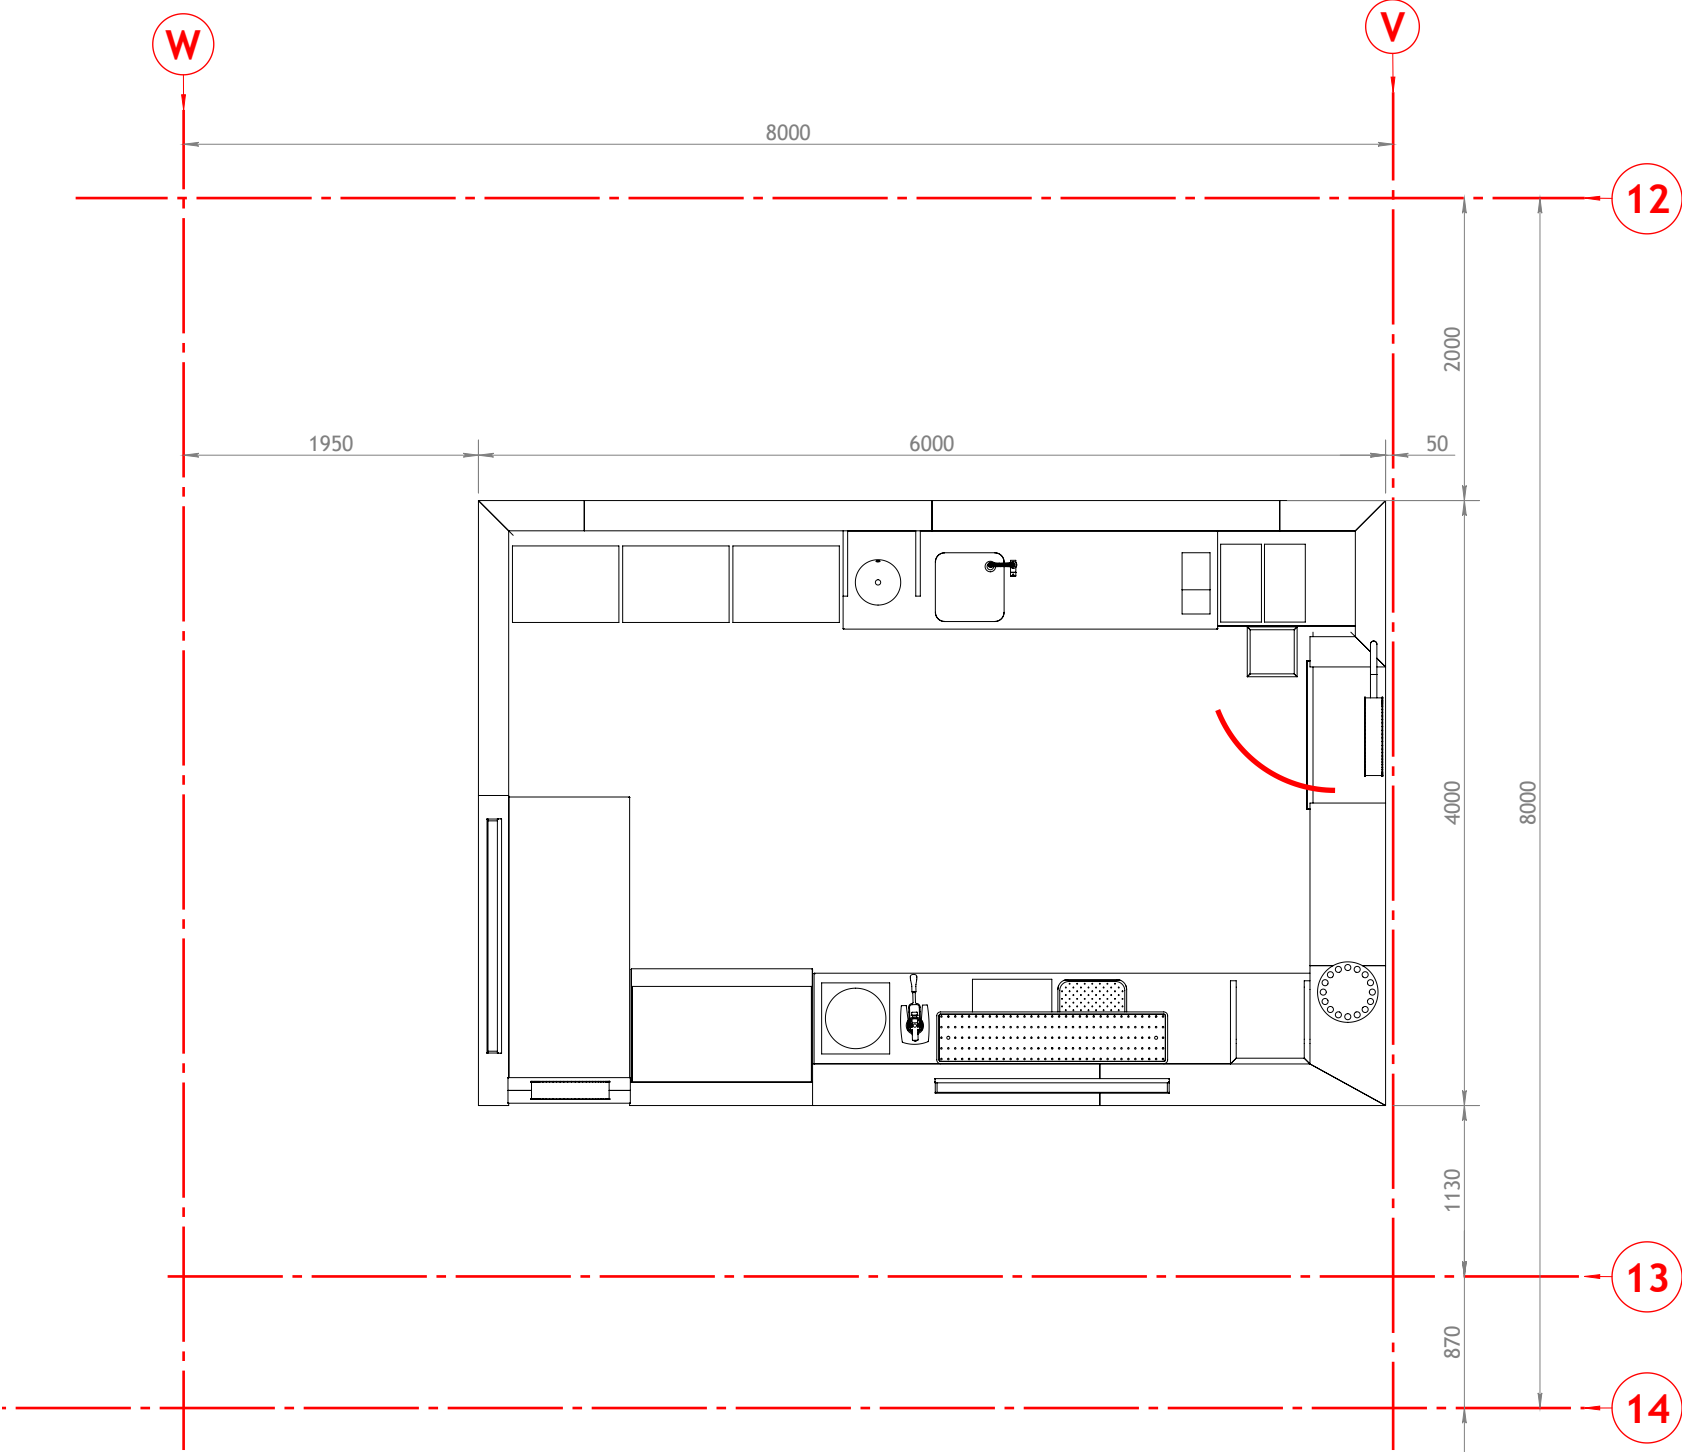

This drawing is the property of Eclipse Manufacturing Solutions: and is protected by the Design Copyright Act 1988. This drawing must not be copied or otherwise reproduced without the express written consent of Eclipse Manufacturing Solutions:
Do not scale from this drawing. All dimensions are to be confirmed on site and subject to building control and statutory approvals.

Rev:	Description:
A	20/10/25 Ramp Added. Glass now pocket glazed. Totem height reduced.
B	28/10/25 Updated to comments.
C	01/12/25 Mass change to layout.
D	16/12/25 Checker plate to ramp RAL 1023.
E	
F	
G	

Weight of Item :- 4001.64KG



Client:
VB Interiors Ltd

Address:
Westfield, White City, London

Project:
Lemonica Kiosk

Title:
General Arrangement
Location Plan


Designer:
Jason Young

Date: 17/12/2025 Scale: 1:50 @ A3
Drawing No:
5271-03-00-GA
Dwg Sht: 1 of 1 Revision: **D**

Unit 4
Arundel Works
Claywheels Lane
Sheffield
S6 1LZ

eclipsemanufacturingsolutions.co.uk

Date Last Saved:- 17 December 2025 10:58:22

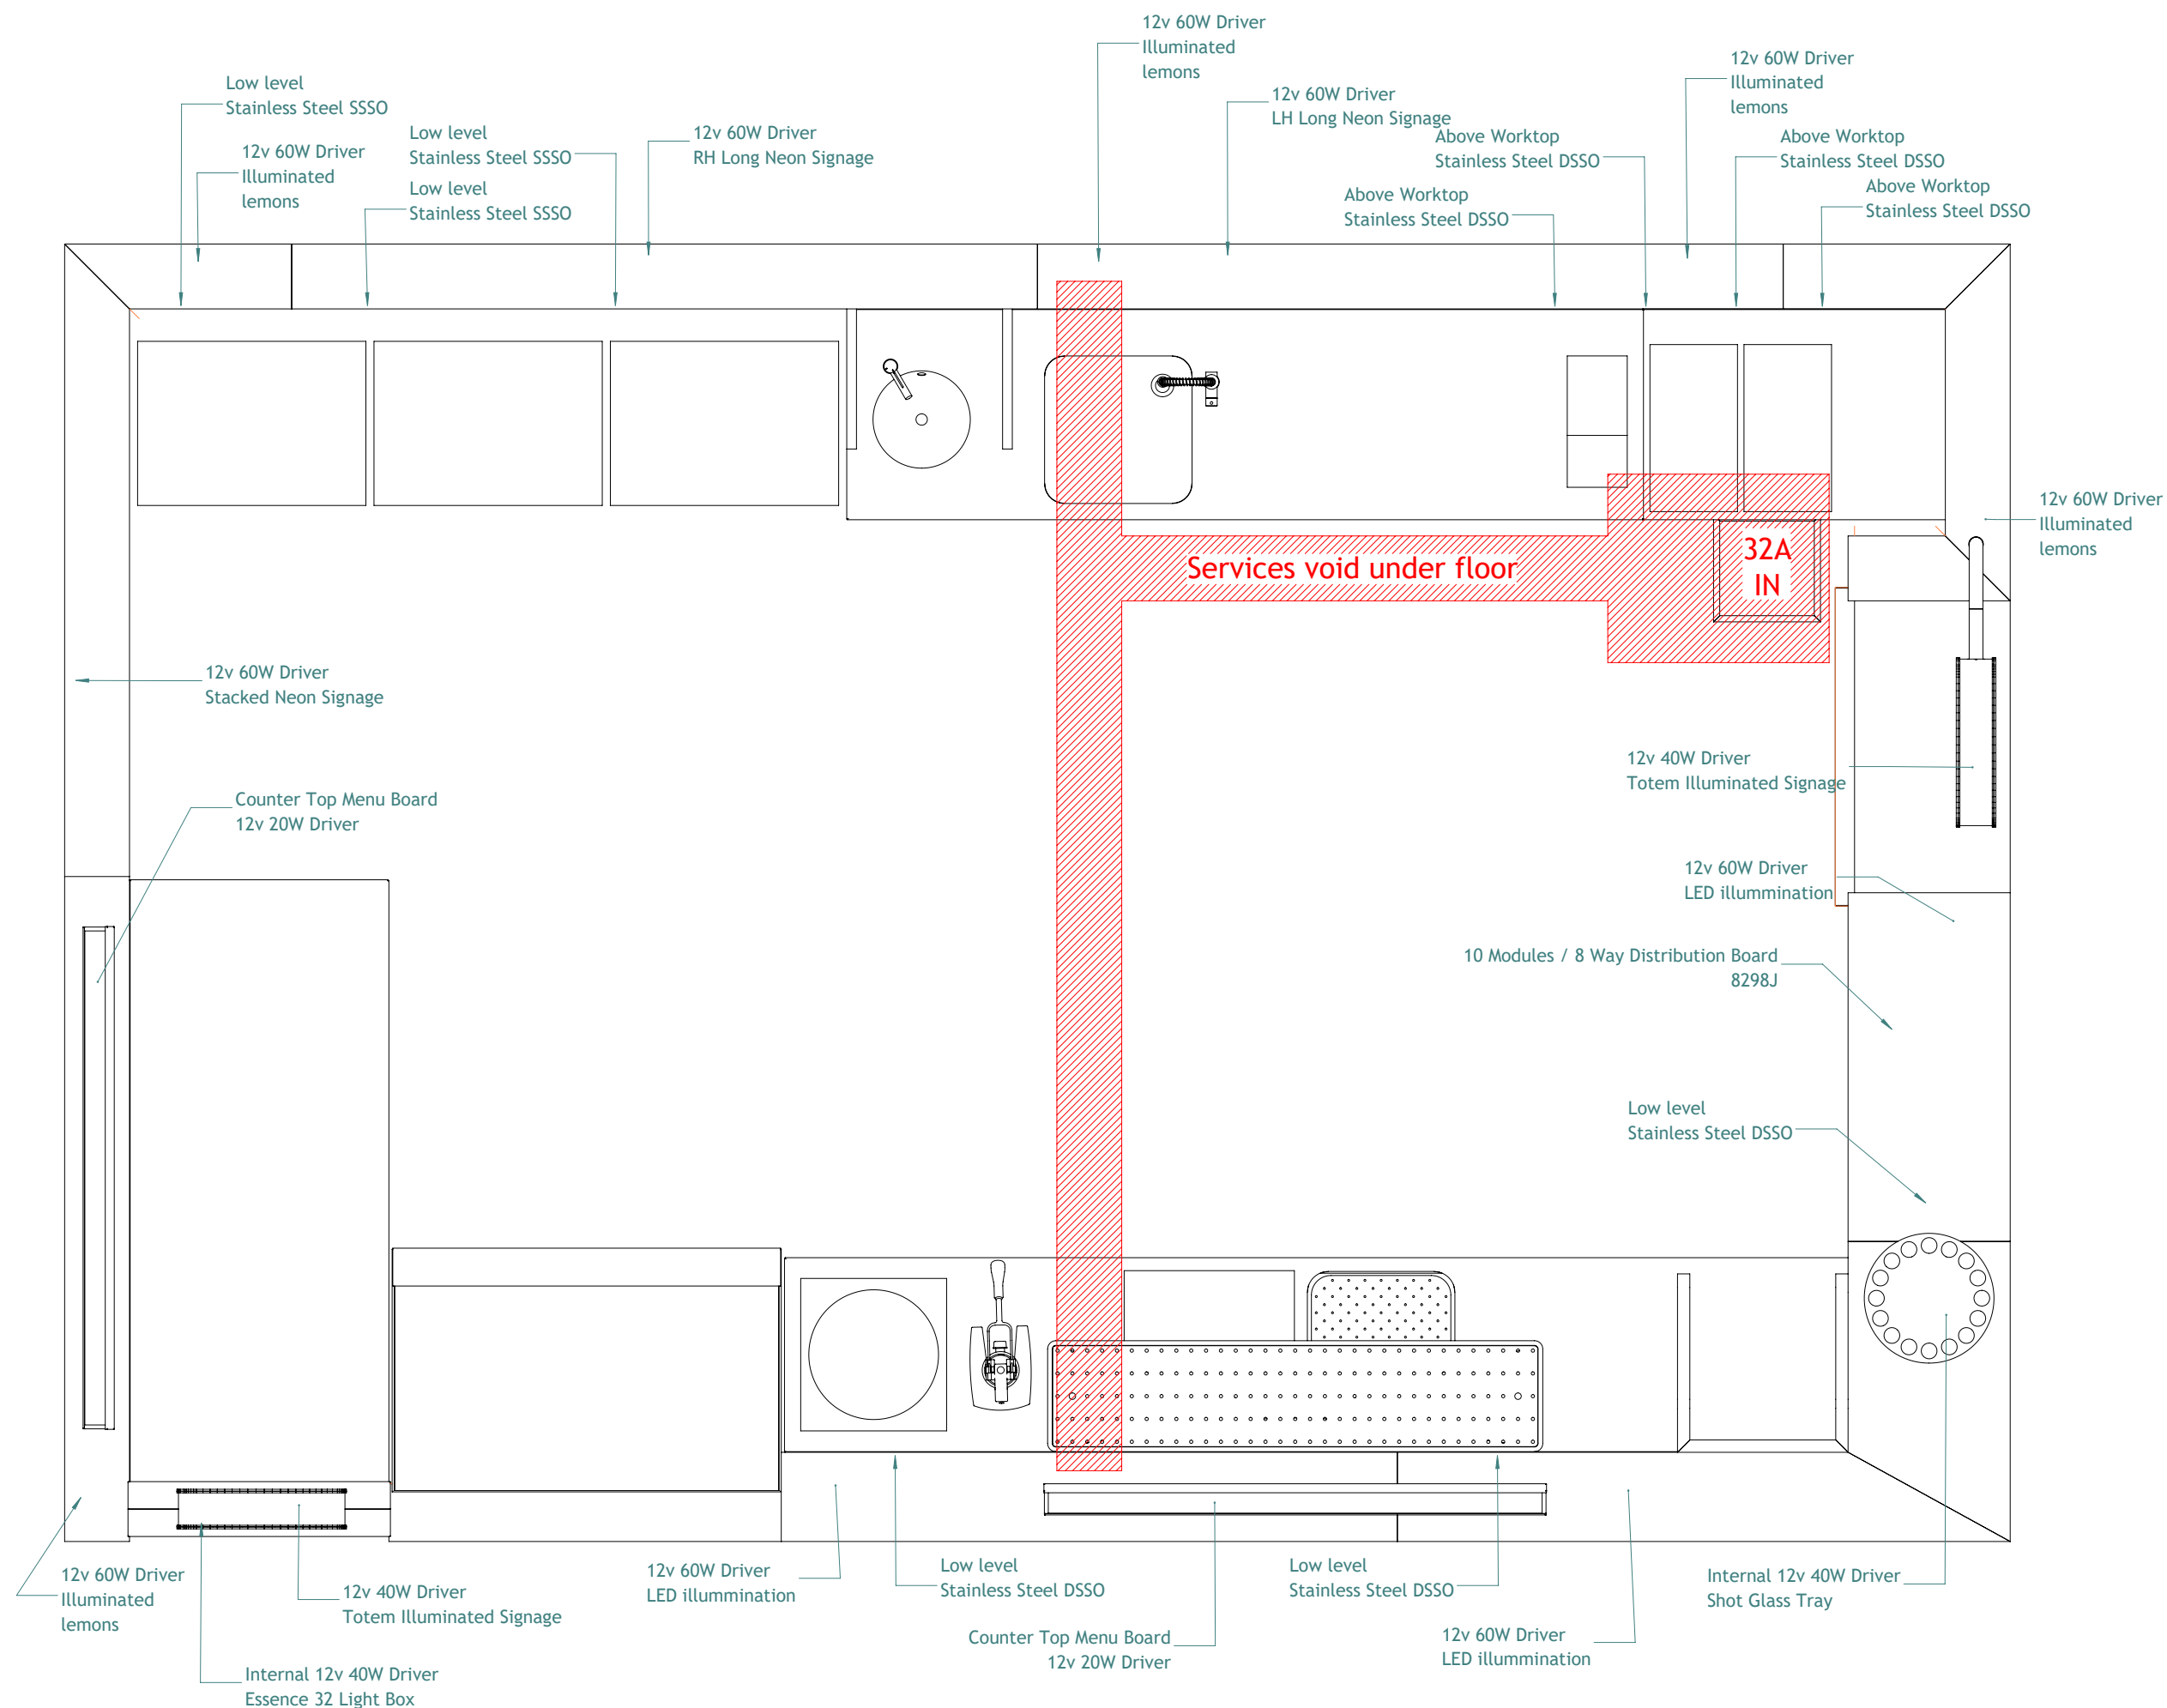

This drawing is the property of Eclipse Manufacturing Solutions: and is protected by the Design Copyright Act 1988. This drawing must not be copied or otherwise reproduced without the express written consent of Eclipse Manufacturing Solutions:
Do not scale from this drawing. All dimensions are to be confirmed on site and subject to building control and statutory approvals.

Rev:	Description:
A	20/10/25 Ramp Added. Glass now pocket glazed. Totem height reduced.
B	28/10/25 Updated to comments.
C	01/12/25 Mass change to layout.
D	16/12/25 Checker plate to ramp RAL 1023.
E	21/01/26 PC removed from ramp. Door added to shelving unit. Sloping acrylic now glass.
F	
G	

Weight of Item :- 4104.63KG



Client:
VB Interiors Ltd

Address:
Westfield, White City, London

Project:
Lemonica Kiosk

Title:
General Arrangement
Electrical


Designer:
Jason Young

Date: 22/01/2026 Scale: 1:20 @ A3
Drawing No: 5271-03-00-GA
Dwg Sht: 1 of 1 Revision: **E**

Unit 4
Arundel Works
Claywheels Lane
Sheffield
S6 1LZ

eclipsemanufacturingsolutions.co.uk

Date Last Saved:- 05 January 2026 10:25:29

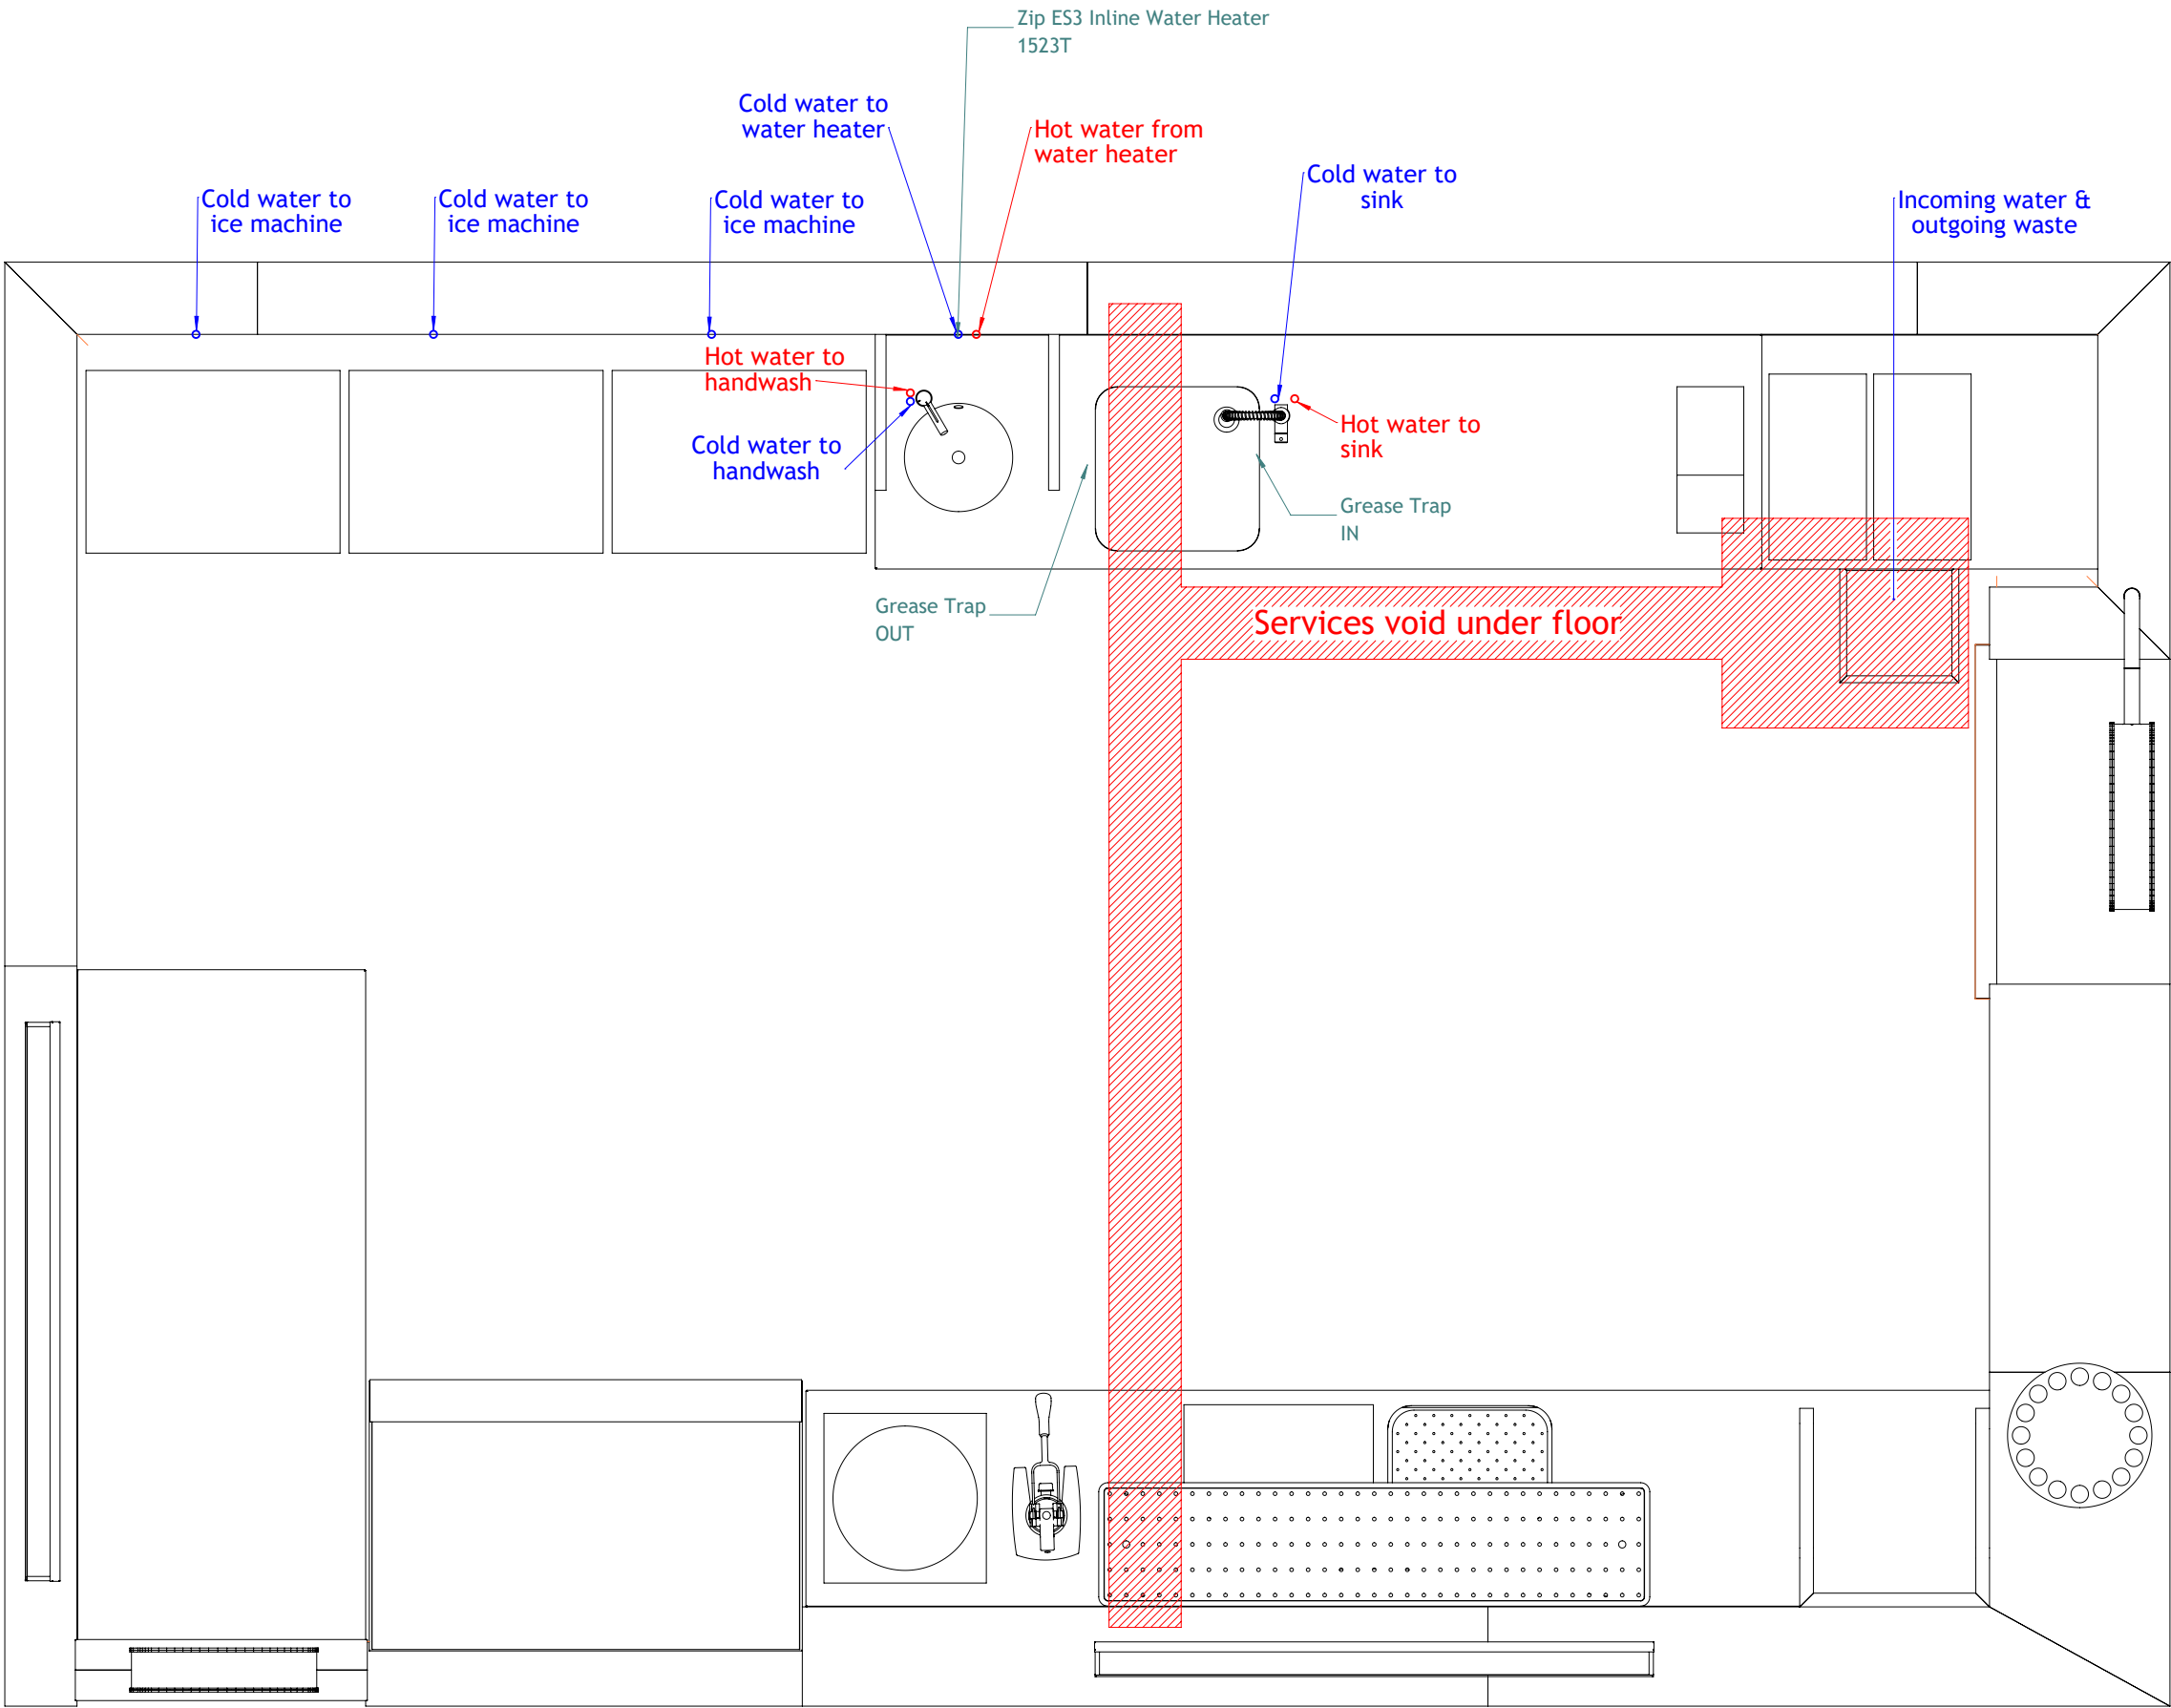

This drawing is the property of Eclipse Manufacturing Solutions: and is protected by the Design Copyright Act 1988. This drawing must not be copied or otherwise reproduced without the express written consent of Eclipse Manufacturing Solutions:
Do not scale from this drawing. All dimensions are to be confirmed on site and subject to building control and statutory approvals.

Rev:	Description:
A	20/10/25 Ramp Added. Glass now pocket glazed. Totem height reduced.
B	28/10/25 Updated to comments.
C	01/12/25 Mass change to layout.
D	16/12/25 Checker plate to ramp RAL 1023.
E	21/01/26 PC removed from ramp. Door added to shelving unit. Stopping acrylic now glass.
F	
G	

Weight of Item :- 4104.63KG



Client:
VB Interiors Ltd

Address:
Westfield, White City, London

Project:
Lemonica Kiosk

Title:
General Arrangement
Plumbing

Designer:
Jason Young

Date: 22/01/2026 Scale: 1:20 @ A3
Drawing No: 5271-03-00-GA
Dwg Sht: 1 of 1 Revision: **E**

Unit 4
Arundel Works
Claywheels Lane
Sheffield
S6 1LZ
eclipsemanufacturingsolutions.co.uk
Date Last Saved:- 18 December 2025 14:35:54

Rev:	Description:
A	20/10/25 Ramp Added. Glass now pocket glazed. Totem height reduced.
B	28/10/25 Updated to comments.
C	01/12/25 Mass change to layout.
D	16/12/25 Checker plate to ramp RAL 1023.
E	21/01/26 PC removed from ramp. Door added to shelving unit. Sloping acrylic now glass.
F	27/01/26 Acylic shroud added to slush machines.
G	

Weight of Item :- 4115.79KG



Client:
VB Interiors Ltd

Address:
Westfield, White City, London

Project:
Lemonica Kiosk

Title:
General Arrangement
Finishes 1

Designer:
Jason Young

Date: 27/01/2026 Scale: 1:30 @ A3
Drawing No:
5271-03-00-GA
Dwg Sht: 1 of 2 Revision: **F**

Unit 4
Arundel Works
Claywheels Lane
Sheffield
S6 1LZ

eclipsemanufacturingsolutions.co.uk

Date Last Saved:- 27 January 2026 13:31:16


Ceramic Metro Tile (White)

DP1 Stainless Steel




DETAIL B
SCALE 1 : 10

Ceramic Metro Tile (White)

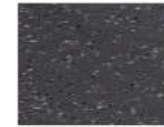

DETAIL E
SCALE 1 : 10

Full Stave European Oak 3000x600
Fire rated Clear Lacquer 15% Sheen (Matt)

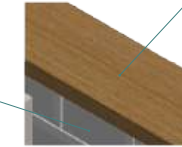

DETAIL D
SCALE 1 : 15

C



B



D



Forbo Safestep R12 Lava

9.5 (4+1.5 Clear EVA+4)Toughened Lam' Glass PAR
In front of illuminted graphic panel.

Full Stave European Oak 3000x600

9.5 (4+1.5 Clear EVA+4)Toughened Lam' Glass PAR
Pocket glazed in front of corrugated panel and acrylic logo.

European Oak
Fire Rated Clear Lacquer 15% Sheen (Matt)

0.9mm DP1 304 Stainless Steel

2mm SS Checker Plate
Self Colour

Green Mint Valchromat
Fire rated Clear Lacquer 15% Sheen (Matt)




Aluminium
RAL 1023 Traffic Yellow

European Oak
Fire Rated Clear Lacquer 15% Sheen (Matt)

Ceramic Metro Tile (Yellow)

DETAIL A
SCALE 1 : 5

DETAIL C
SCALE 1 : 10

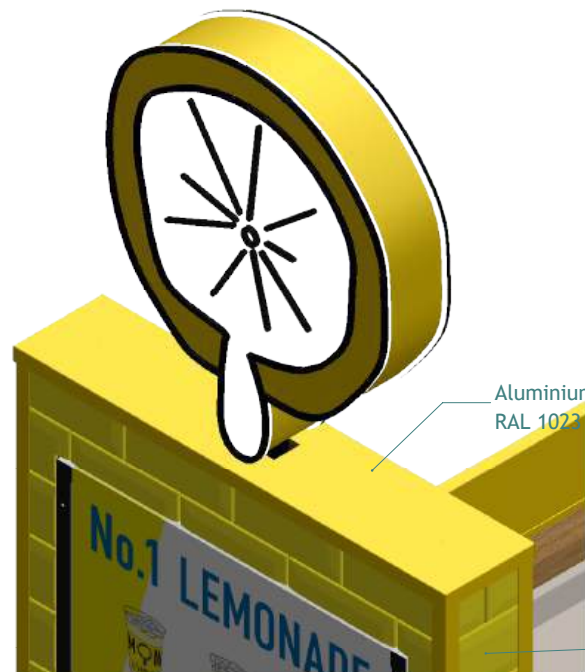

Rev: Description:


A	20/10/25 Ramp Added. Glass now pocket glazed.. Totem height reduced. 28/10/25 Updated to comments.
B	
C	01/12/25 Mass change to layout.
D	16/12/25 Checker plate to ramp RAL 1023.
E	21/01/26 PC removed from ramp. Door added to shelving unit. Sloping acrylic now glass.
F	27/01/26 Acylic shroud added to slush machines.
G	



DETAIL F
SCALE 1 : 15

- Full Stave European Oak 3000x600
Fire rated Clear Lacquer 15% Sheen (Matt)
- Yellow Neon Signage behind Glass
- 9.5 (4+1.5 Clear EVA+4)Toughened Lam' Glass PAR
- European Oak
Fire Rated Clear Lacquer 15% Sheen (Matt)
- Illuminated Acrylic Lemon
Plain Carbon Steel
30mm opal acrylic cut out with bevel
- Faced with 1mm SS coated RAL 1023

- Green Mint Valchromat
Fire rated Clear Lacquer 15% Sheen (Matt)

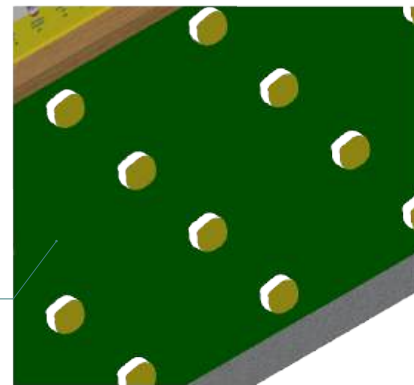

DETAIL G
SCALE 1 : 15

Weight of Item :- 4115.79KG



Client:
VB Interiors Ltd

Address:
Westfield, White City, London

Project:
Lemonica Kiosk

Title:
General Arrangement
Finishes 2

Designer:
Jason Young

Date: 27/01/2026 Scale: 1:30 @ A3

Drawing No:
5271-03-00-GA

Dwg Sht: 2 of 2

Revision: **F**

Unit 4
Arundel Works
Claywheels Lane
Sheffield
S6 1LZ

eclipsemanufacturingsolutions.co.uk

Date Last Saved:- 27 January 2026 13:42:32

Rev:	Description:
A	20/10/25 Ramp Added. Glass now pocket glazed. Totem height reduced.
B	28/10/25 Updated to comments.
C	01/12/25 Mass change to layout.
D	16/12/25 Checker plate to ramp RAL 1023.
E	21/01/26 PC removed from ramp. Door added to shelving unit. Sloping acrylic now glass.
F	
G	

Weight of Item :- 4104.63KG



Client:
VB Interiors Ltd

Address:
Westfield, White City, London

Project:
Lemonica Kiosk

Title:
General Arrangement
Sections 1


Designer:
Jason Young

Date: 22/01/2026 Scale: 1:20 @ A3
Drawing No: 5271-03-00-GA
Dwg Sht: 2 of 2 Revision: **E**

Unit 4
Arundel Works
Claywheels Lane
Sheffield
S6 1LZ

eclipsemanufacturingsolutions.co.uk

Date Last Saved:- 08 January 2026 10:46:01

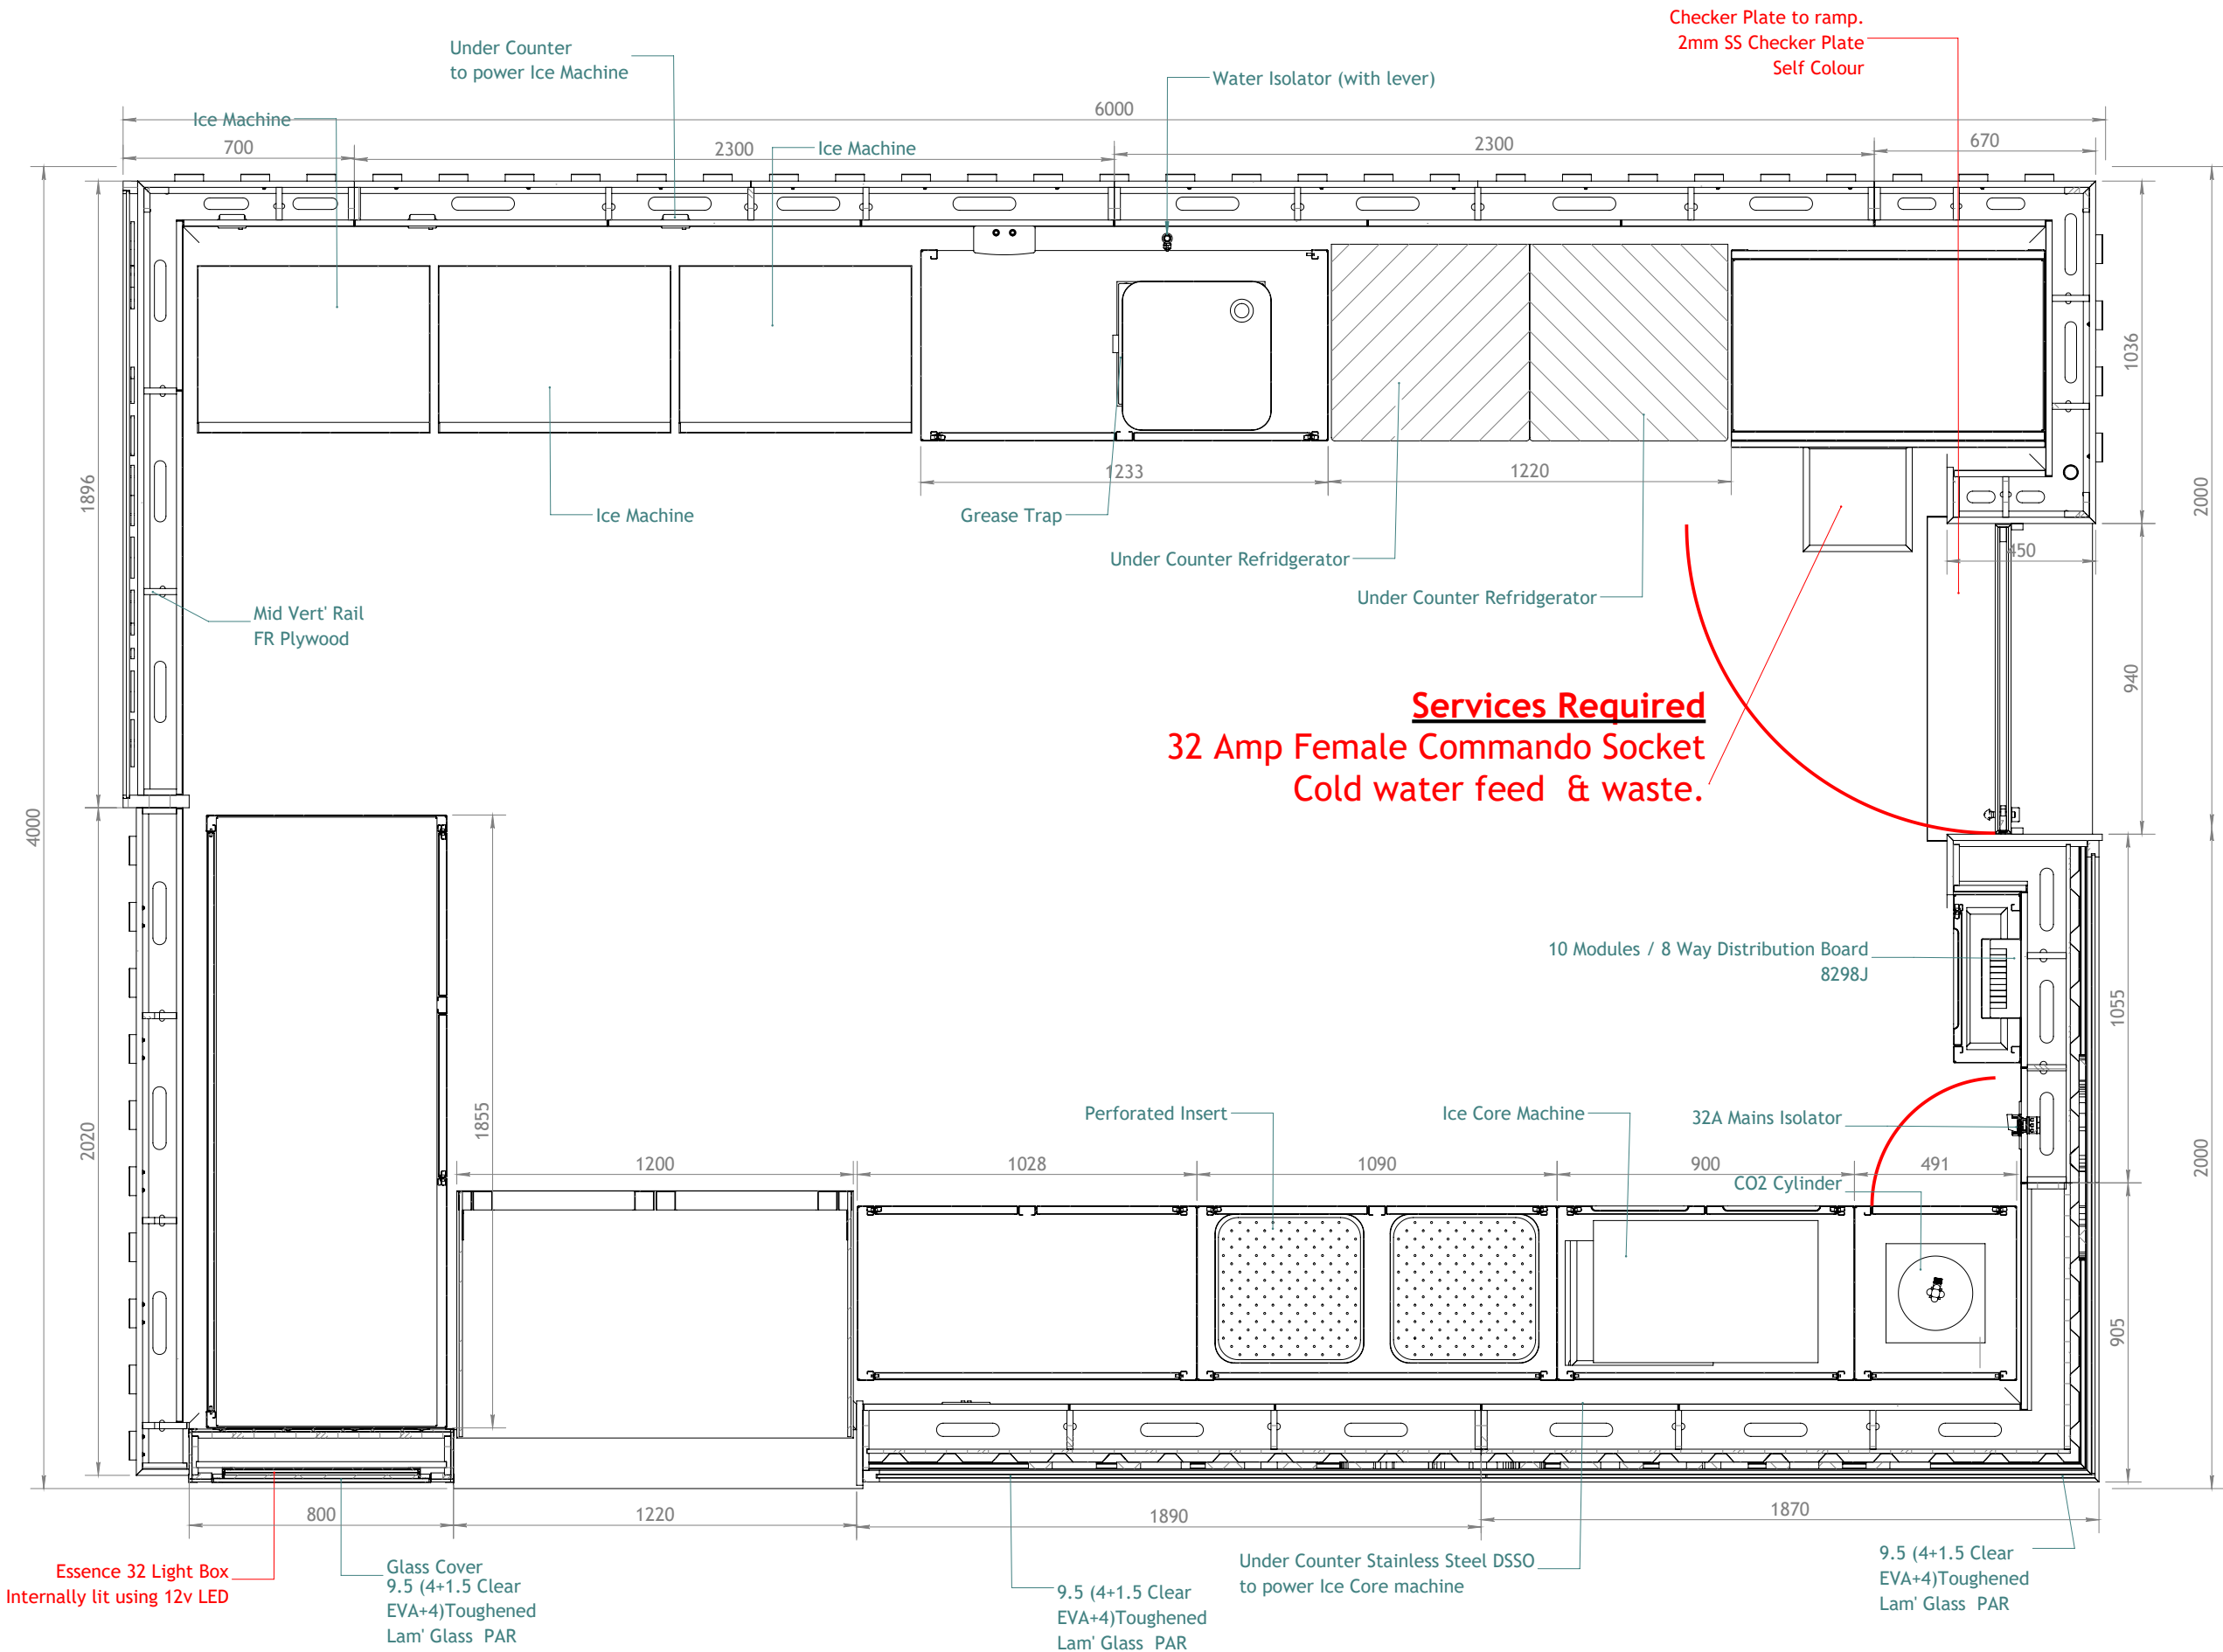

SECTION E-E

Rev:	Description:
A	20/10/25 Ramp Added. Glass now pocket glazed. Totem height reduced.
B	28/10/25 Updated to comments.
C	01/12/25 Mass change to layout.
D	16/12/25 Checker plate to ramp RAL 1023.
E	21/01/26 PC removed from ramp. Door added to shelving unit. Stopping acrylic now glass.
F	27/01/26 Acylic shroud added to slush machines.
G	

Weight of Item :- 4115.79KG



Client:
VB Interiors Ltd

Address:
Westfield, White City, London

Project:
Lemonica Kiosk

Title:
General Arrangement
Sections 2

Designer:
Jason Young

Date: 27/01/2026 Scale: 1:20 @ A3

Drawing No:
5271-03-00-GA


Dwg Sht: 1 of 1

Revision: **F**

Unit 4
Arundel Works
Claywheels Lane
Sheffield
S6 1LZ



eclipsemanufacturingsolutions.co.uk

Date Last Saved:- 22 January 2026 10:14:23

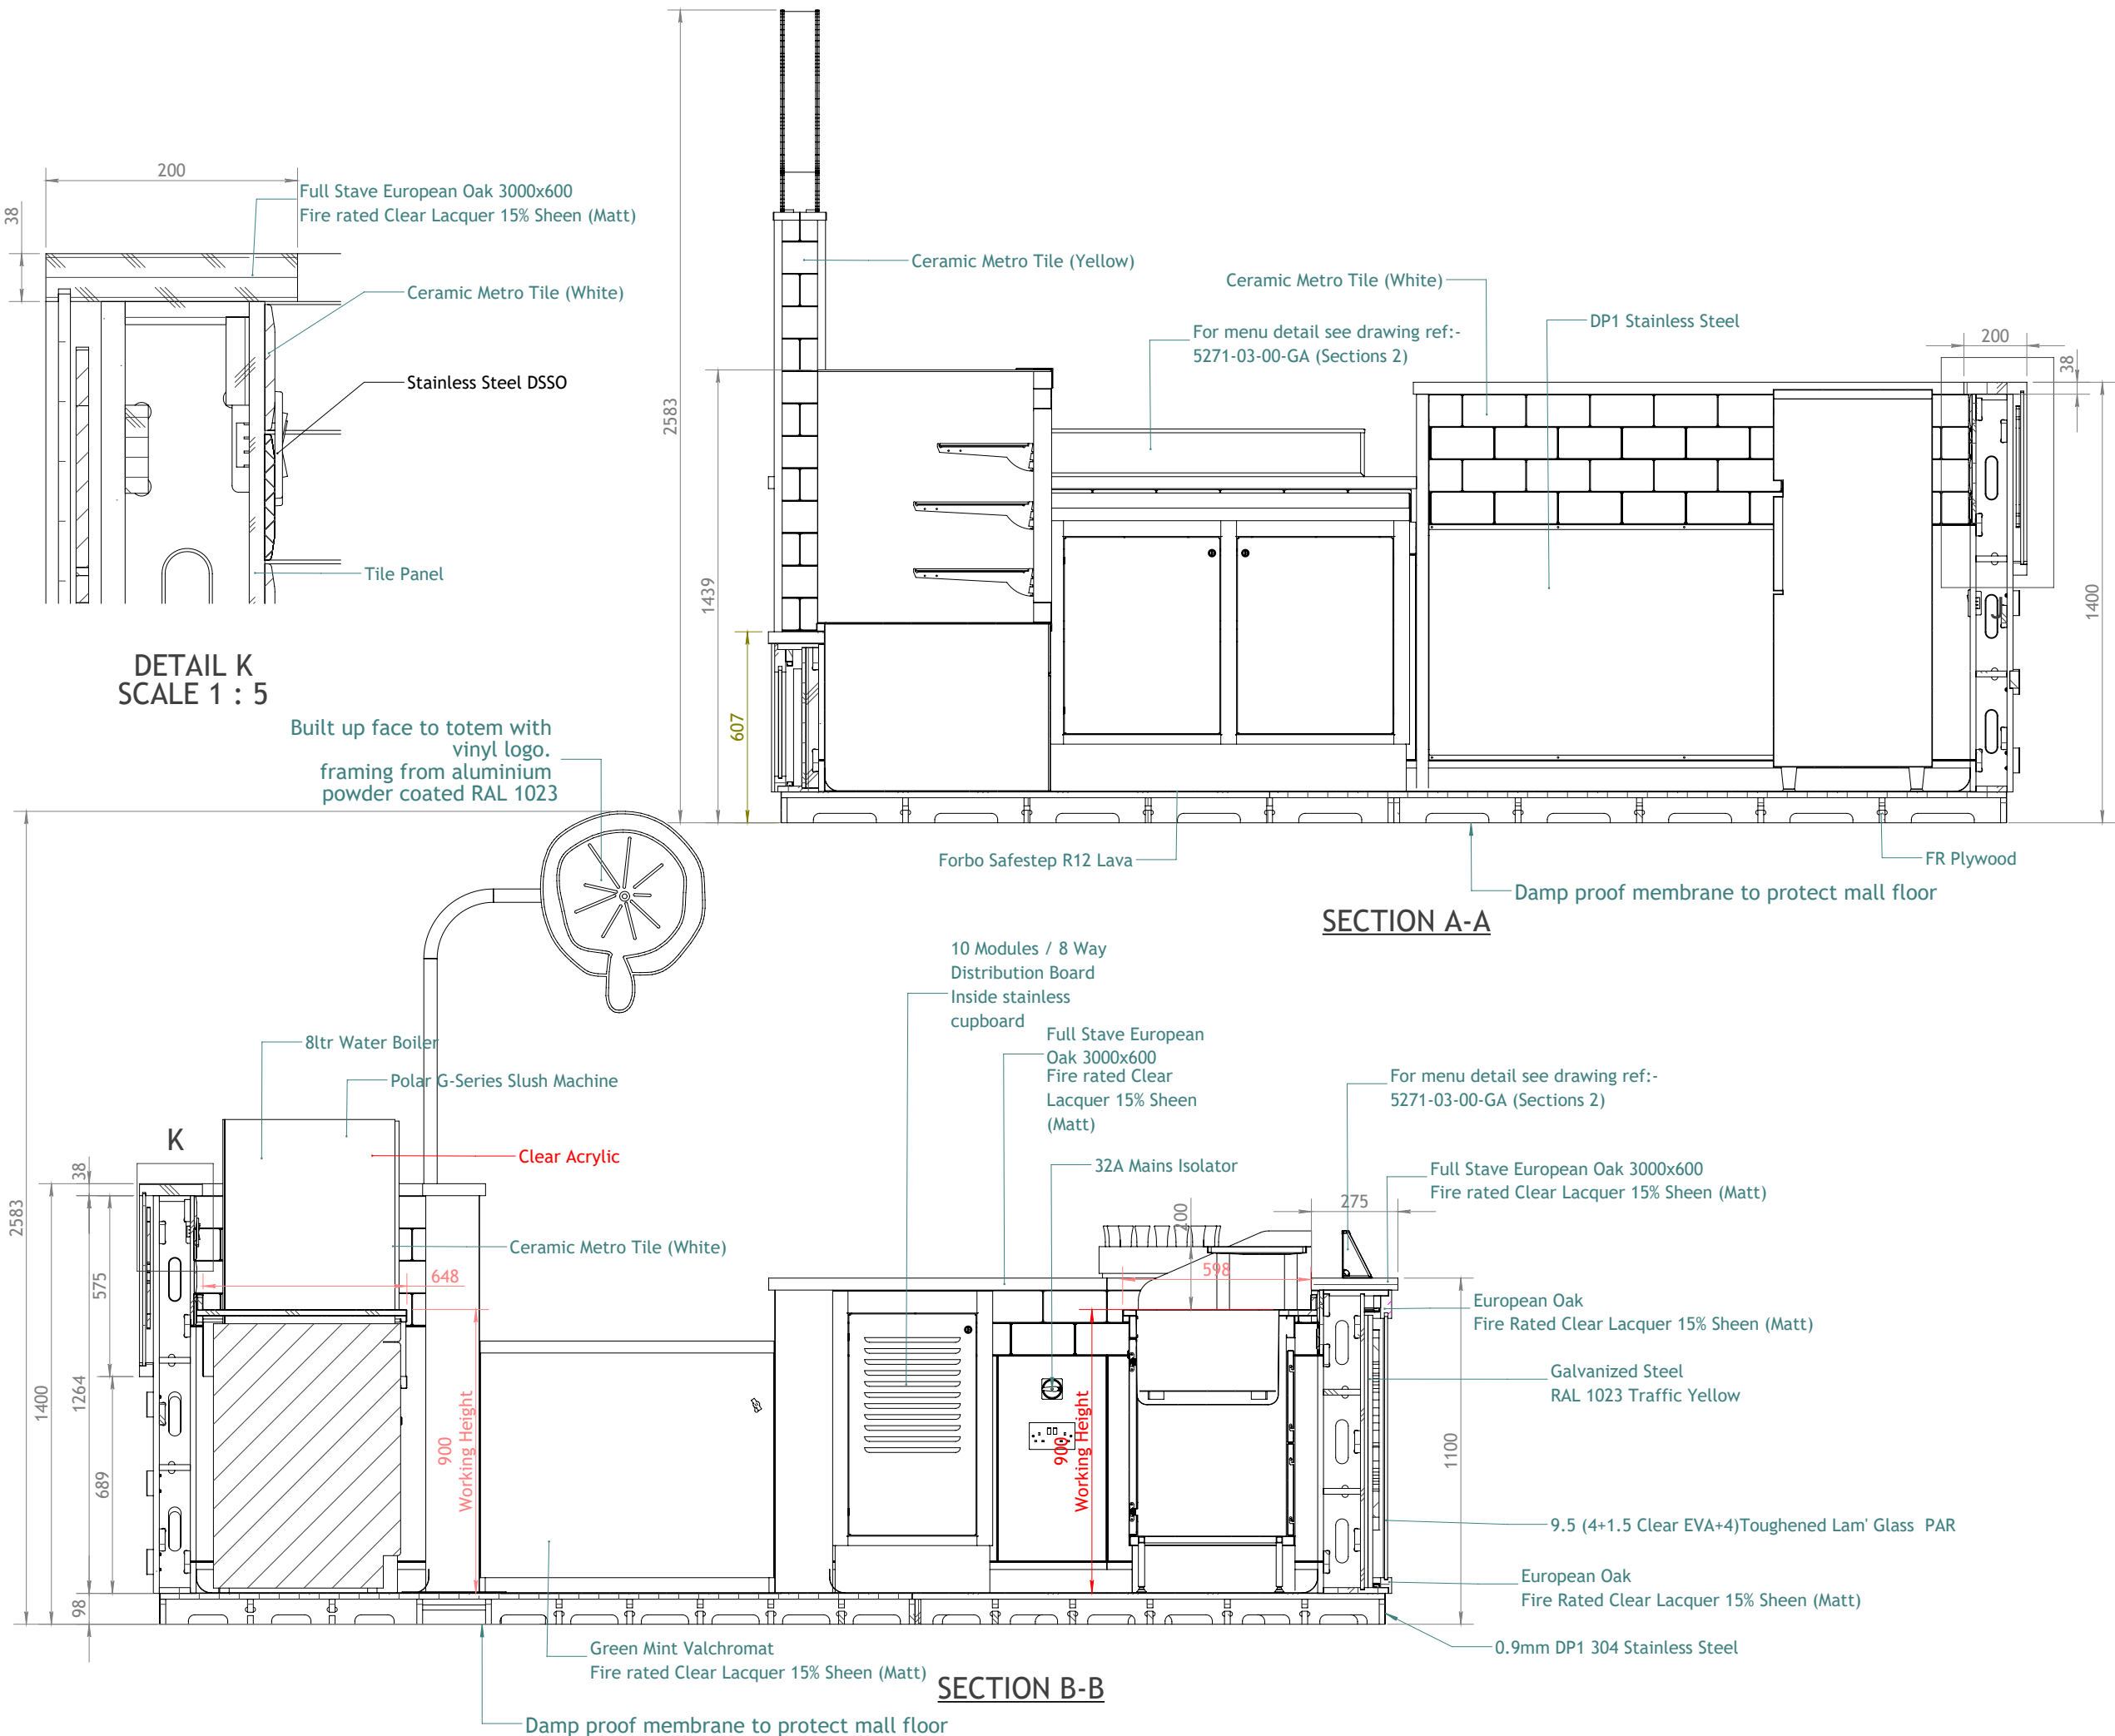

Rev: Description:

- A** 20/10/25 Ramp Added. Glass now pocket glazed.. Totem height reduced.
B 28/10/25 Updated to comments.
C 01/12/25 Mass change to layout.
D 16/12/25 Checker plate to ramp RAL 1023.
E 21/01/26 PC removed from ramp. Door added to shelving unit. Sloping acrylic now glass.
F 27/01/26 Acylic shroud added to slush machines.
G

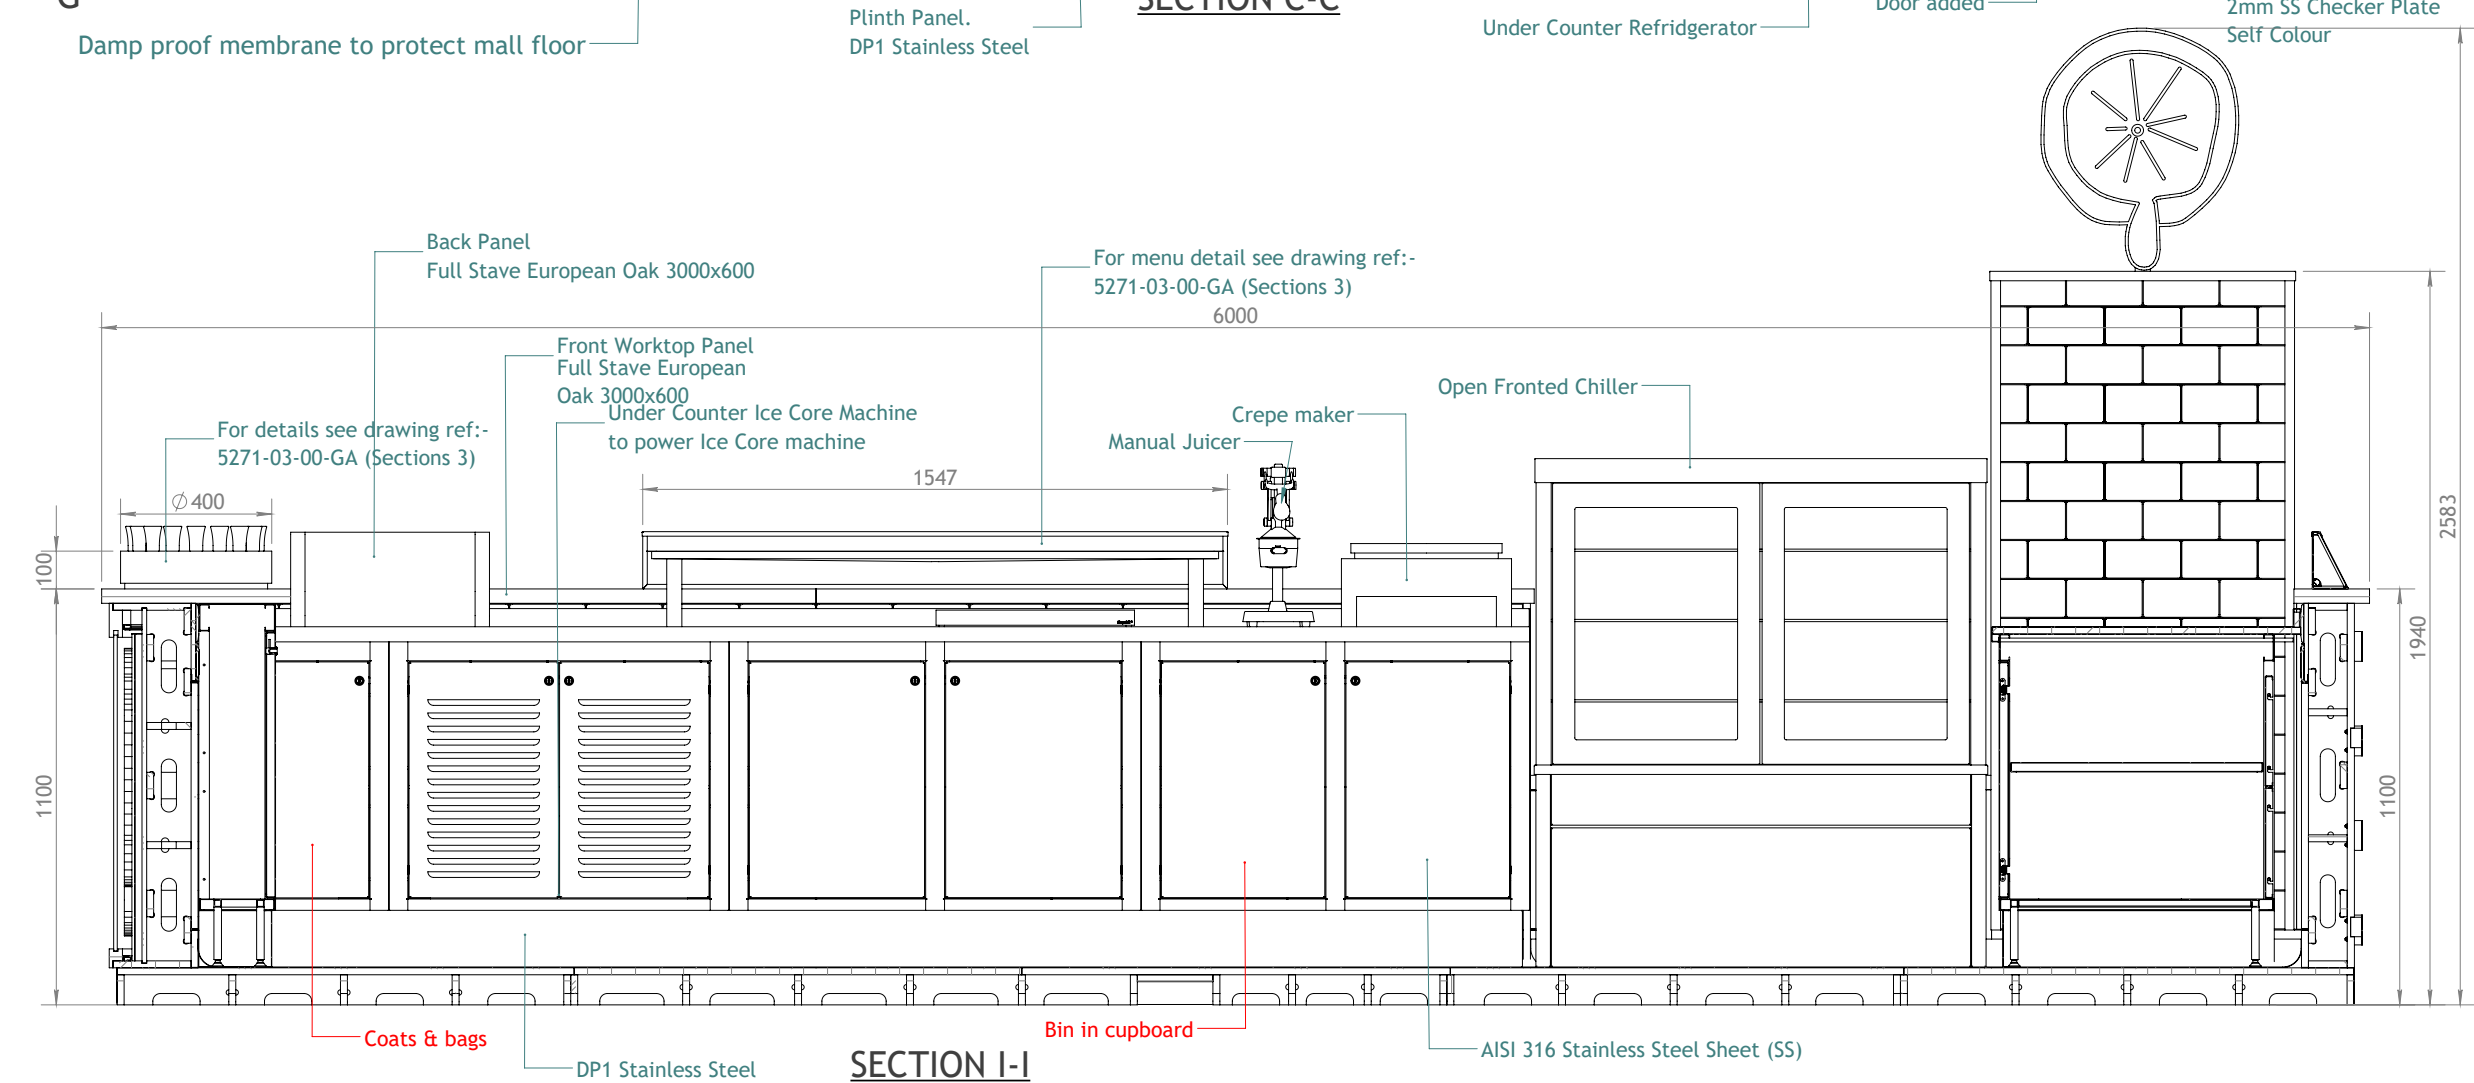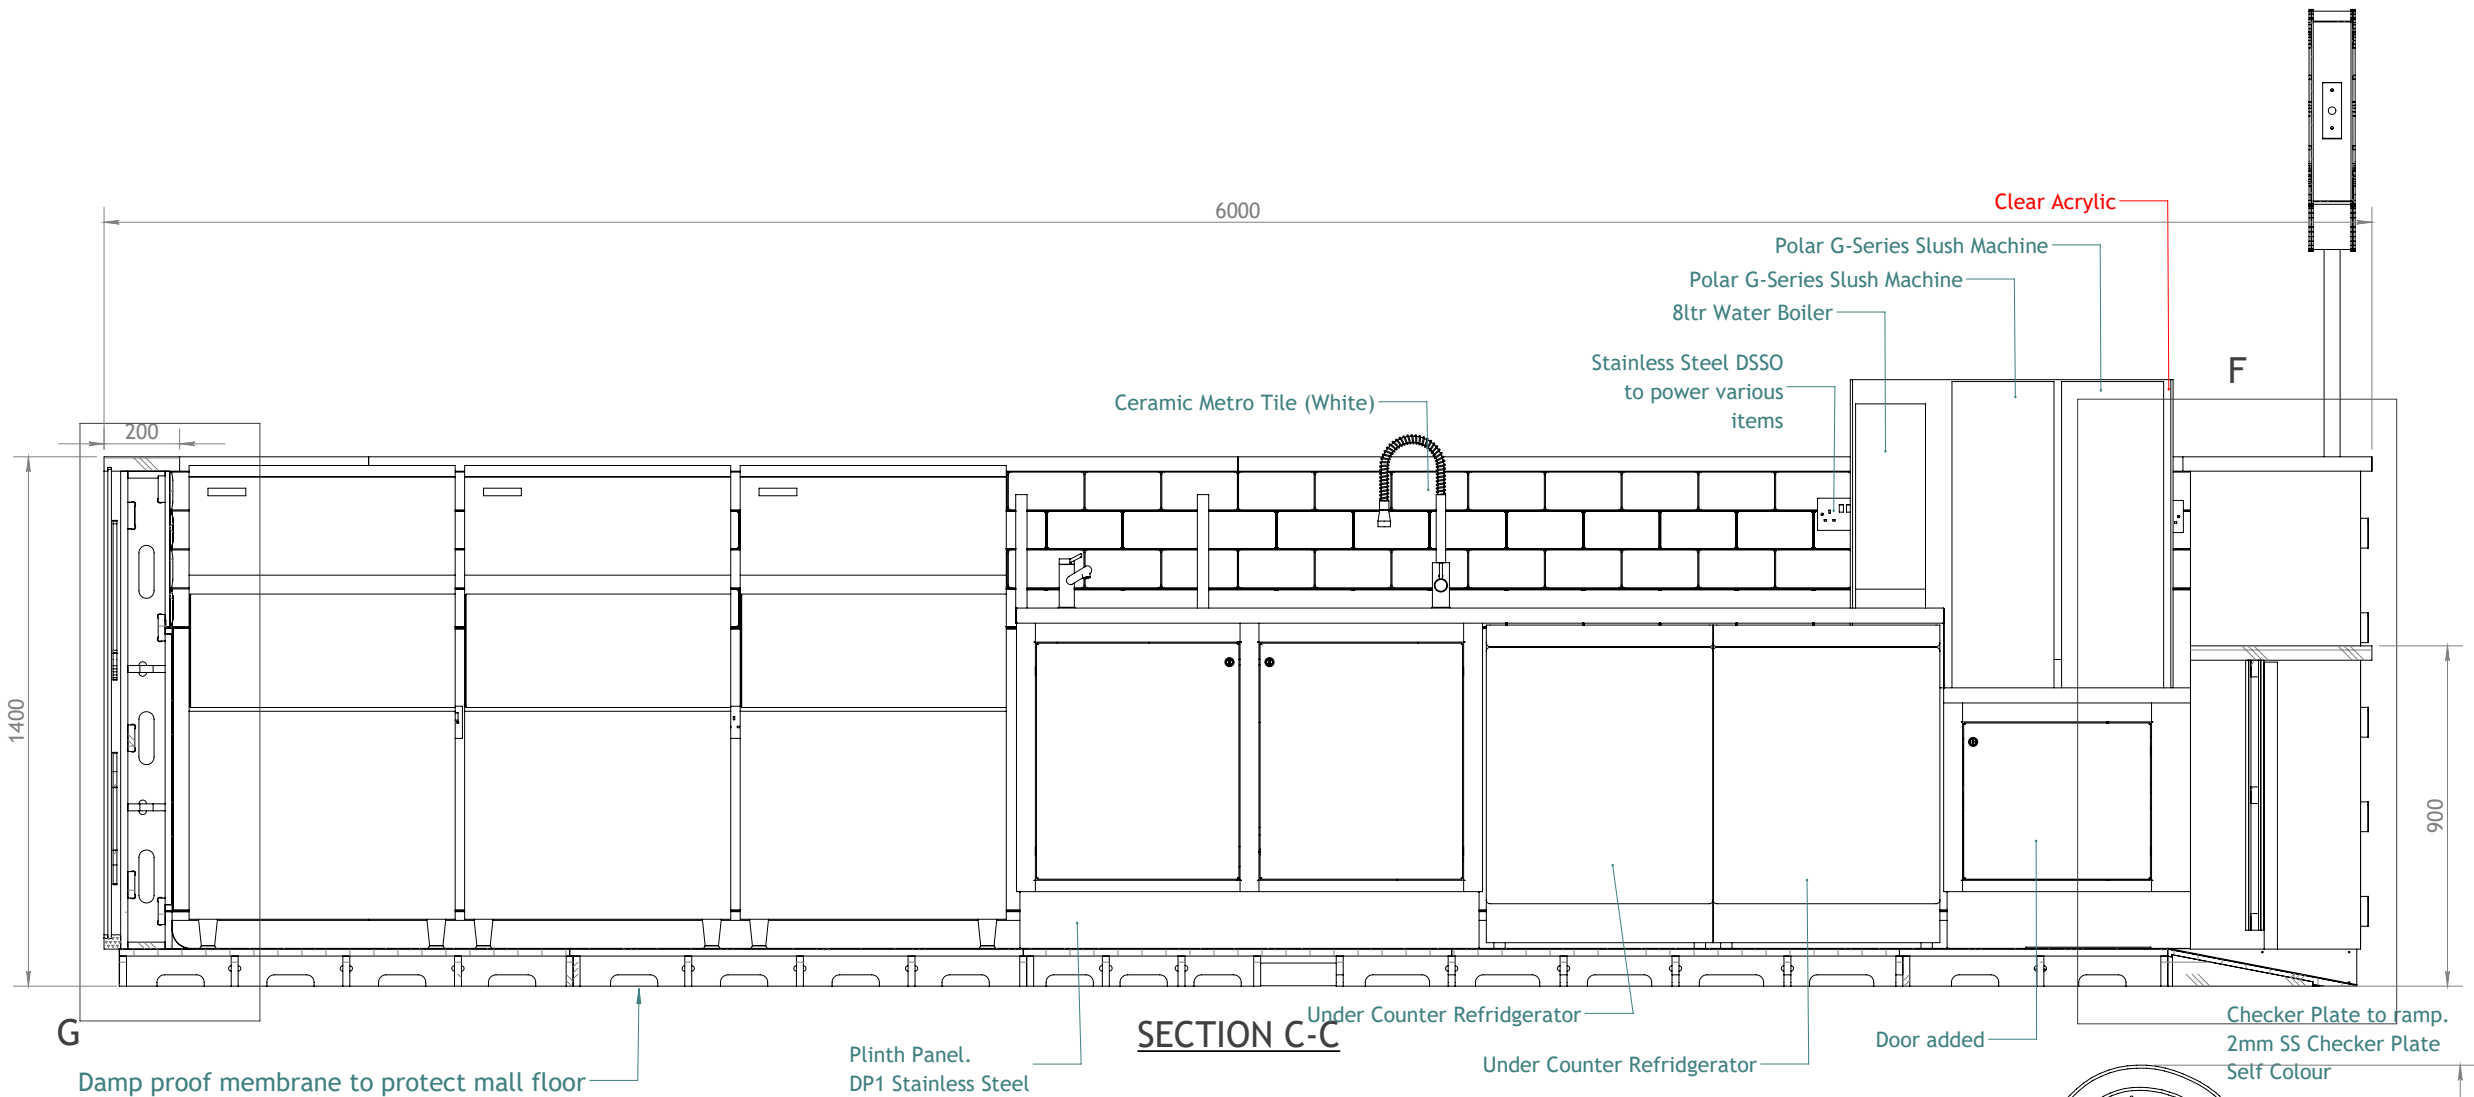

Weight of Item :- 4115.79KG



Client:
VB Interiors Ltd

Address:
Westfield, White City, London

Project:
Lemonica Kiosk

Title:
General Arrangement
Sections 3

Designer:
Jason Young

Date: 27/01/2026 Scale: 1:20 @ A3

Drawing No:
5271-03-00-GA

Dwg Sht: 1 of 1

Revision: **F**

Unit 4
Arundel Works
Claywheels Lane
Sheffield
S6 1LZ

eclipsemanufacturingsolutions.co.uk

Date Last Saved:- 22 January 2026 10:31:06

Rev:	Description:
A	20/10/25 Ramp Added. Glass now pocket glazed. Totem height reduced.
B	28/10/25 Updated to comments.
C	01/12/25 Mass change to layout.
D	16/12/25 Checker plate to ramp RAL 1023.
E	21/01/26 PC removed from ramp. Door added to shelving unit. Sloping acrylic now glass.
F	
G	

Weight of Item :- 4104.63KG



Client:
VB Interiors Ltd

Address:
Westfield, White City, London

Project:
Lemonica Kiosk

Title:
General Arrangement
Sections 4


Designer:
Jason Young

Date: 22/01/2026 Scale: 1:20 @ A3
Drawing No: 5271-03-00-GA
Dwg Sht: 1 of 1 Revision: **E**

Unit 4
Arundel Works
Claywheels Lane
Sheffield
S6 1LZ

eclipsemanufacturingsolutions.co.uk

Date Last Saved:- 22 January 2026 10:35:20

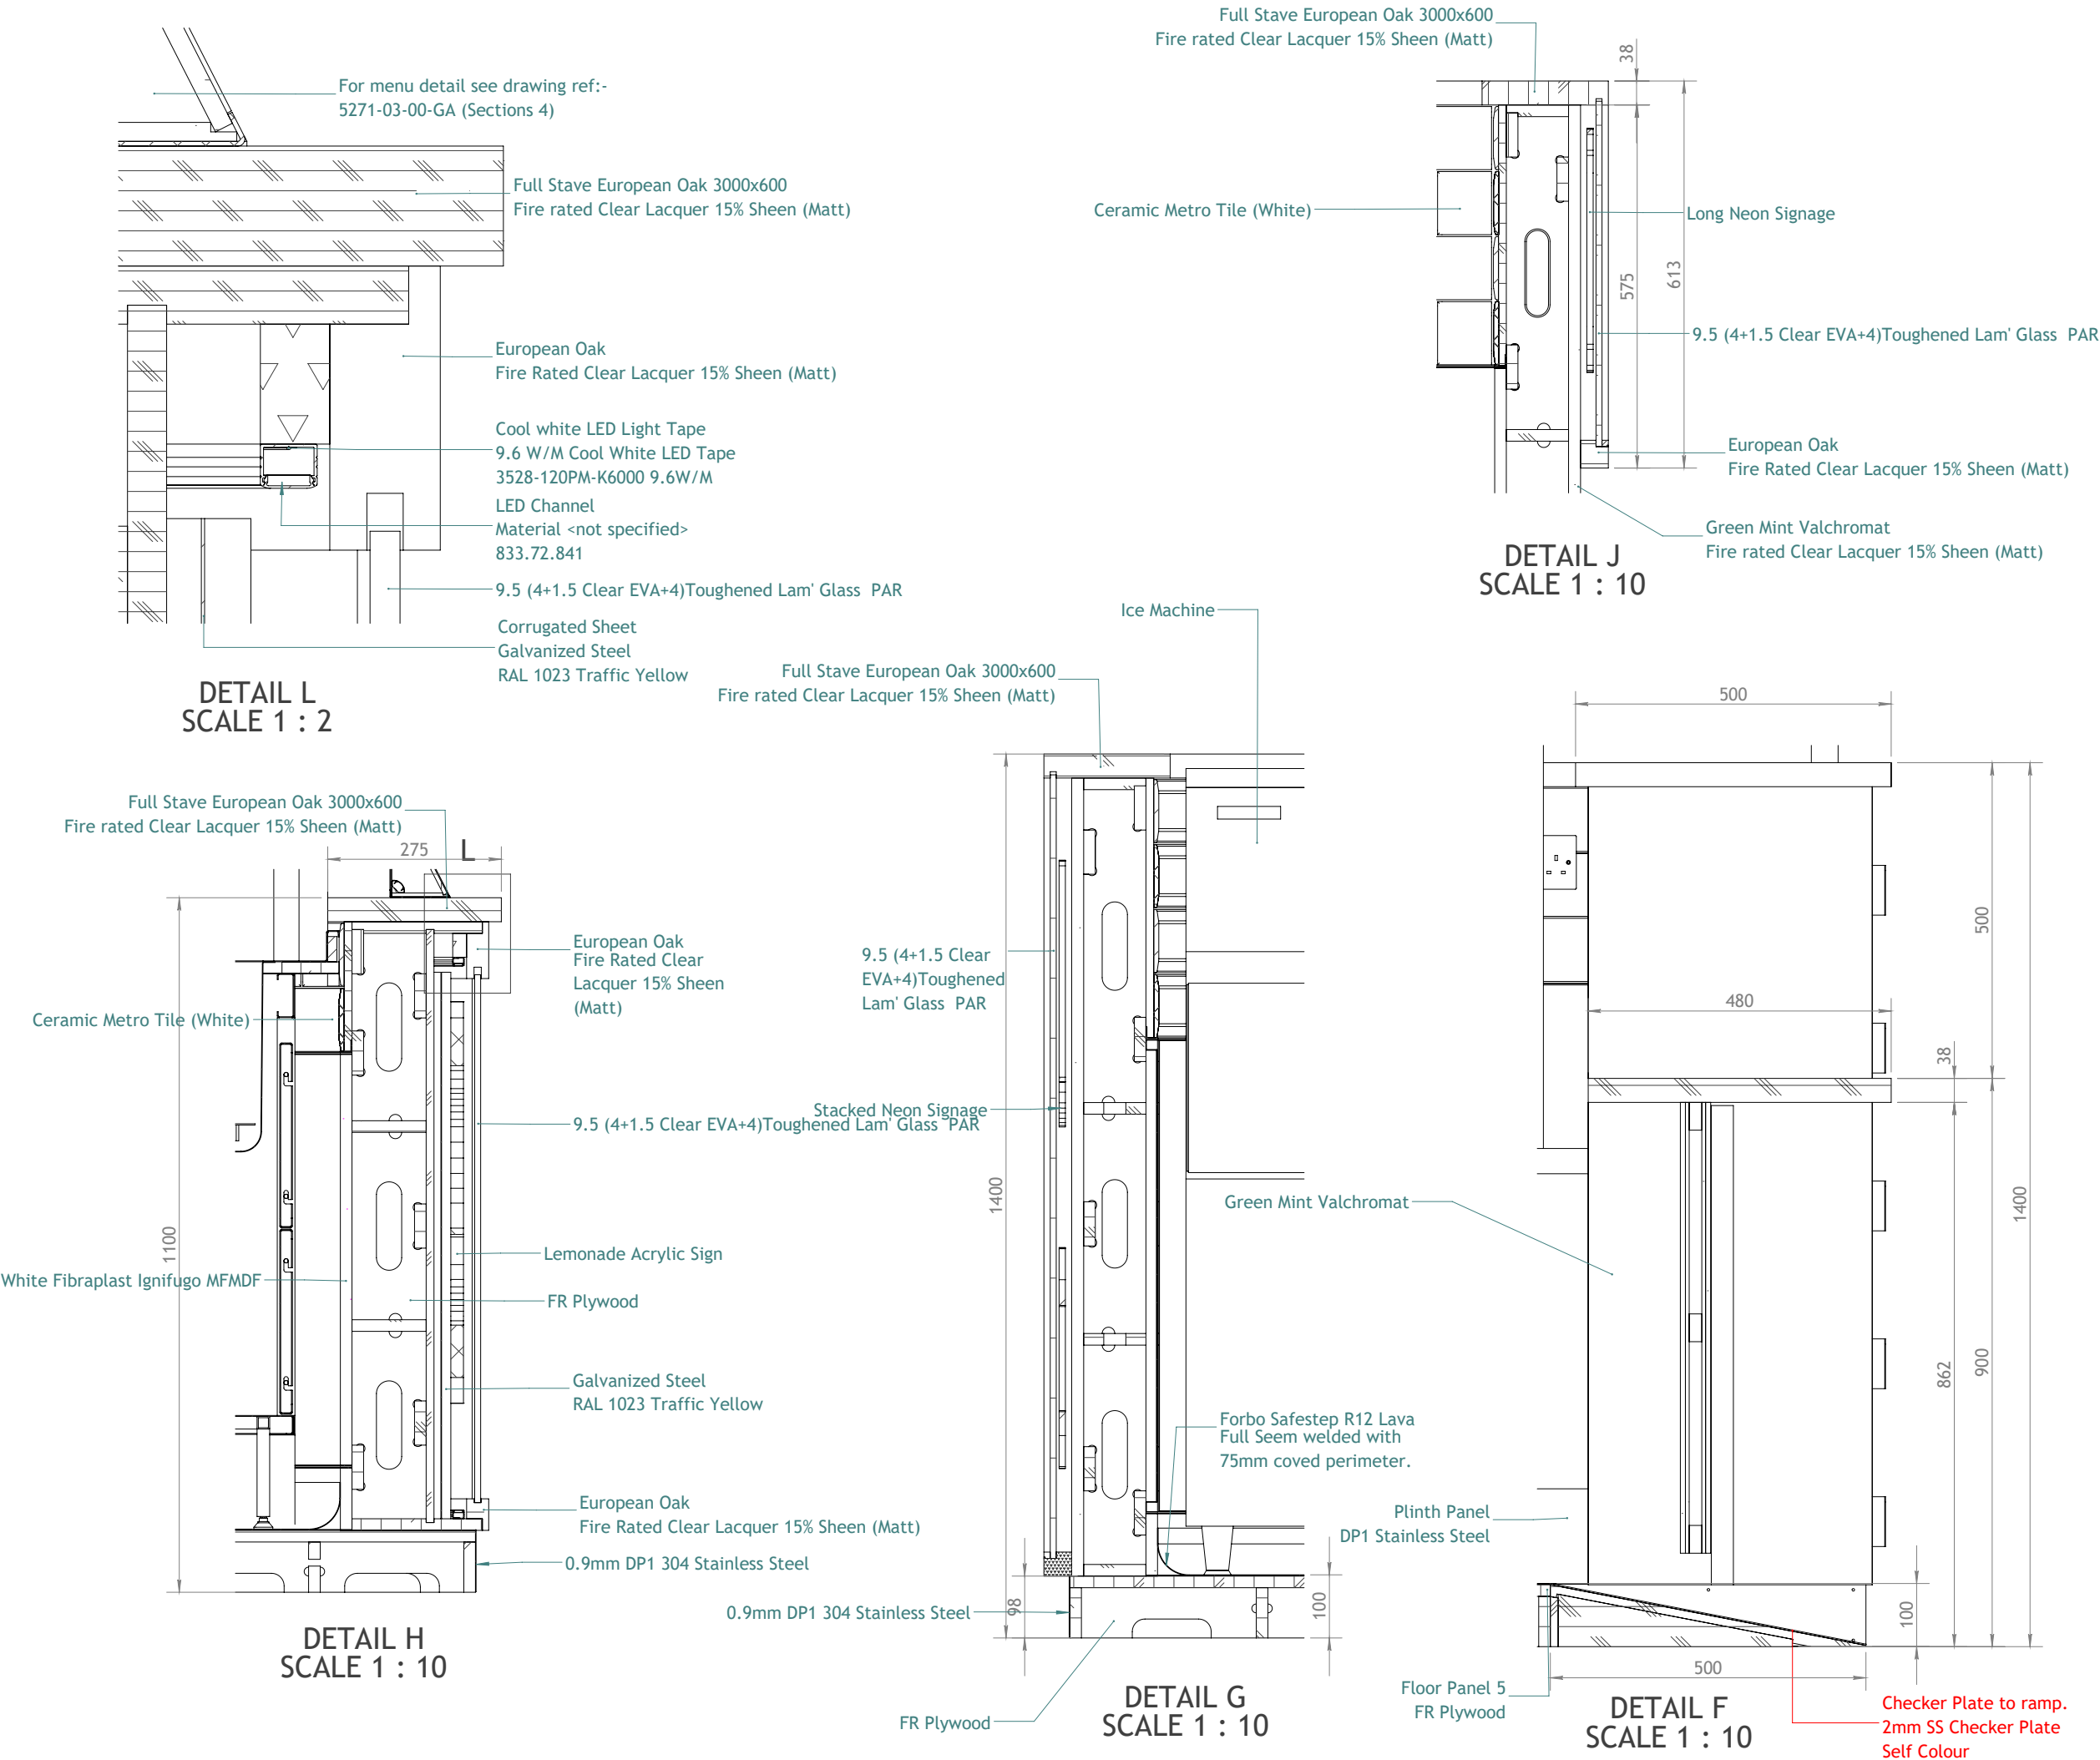



ITEM NO.	PART NUMBER	Item	Weight(Kg)	QTY.
1	5271-03-01-SA1	Flooring Frame 1	10.25	1
2	5271-03-01-SA2	Flooring Frame 2	10.05	1
3	5271-03-01-SA3	Flooring Frame 3	6.45	1
4	5271-03-01-SA4	Flooring Frame 4	7.00	1
5	5271-03-01-SA5	Flooring Frame 5	11.35	1
6	5271-03-01-SA6	Flooring Frame 6	10.72	1
7	5271-03-01-SA7	Flooring Frame 7	10.25	1
8	5271-03-01-SA8	Flooring Frame 8	9.03	1
9	5271-03-01-SA9	Flooring Panels	157.07	1
10	5271-03-01-SA10	Stainless Skirting	13.83	1
11	5271-03-01-SA11	Access Ramp	12.20	1
12	5271-03-01-SA12	300x300 Floor Access panel	2.10	1
13	5271-03-01-SA13	Flooring Frame 13	10.05	1
14	5271-03-01-SA14	Flooring Frame 14	6.45	1
15	5271-03-01-SA15	Flooring Frame 15	11.81	1
16	5271-03-01-GA-01	Vinyl Flooring	25.18 kg	1

This drawing is the property of Eclipse Manufacturing Solutions: and is protected by the Design Copyright Act 1968. This drawing must not be copied or otherwise reproduced without the express written consent of Eclipse Manufacturing Solutions:


Do not scale from this drawing. All dimensions are to be confirmed on site and subject to building control and statutory approvals.

Rev: Description:

A
B
C
D
E
F
G

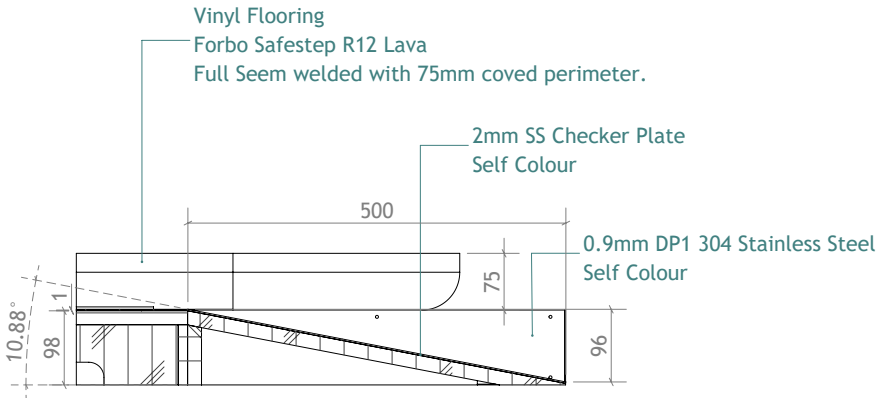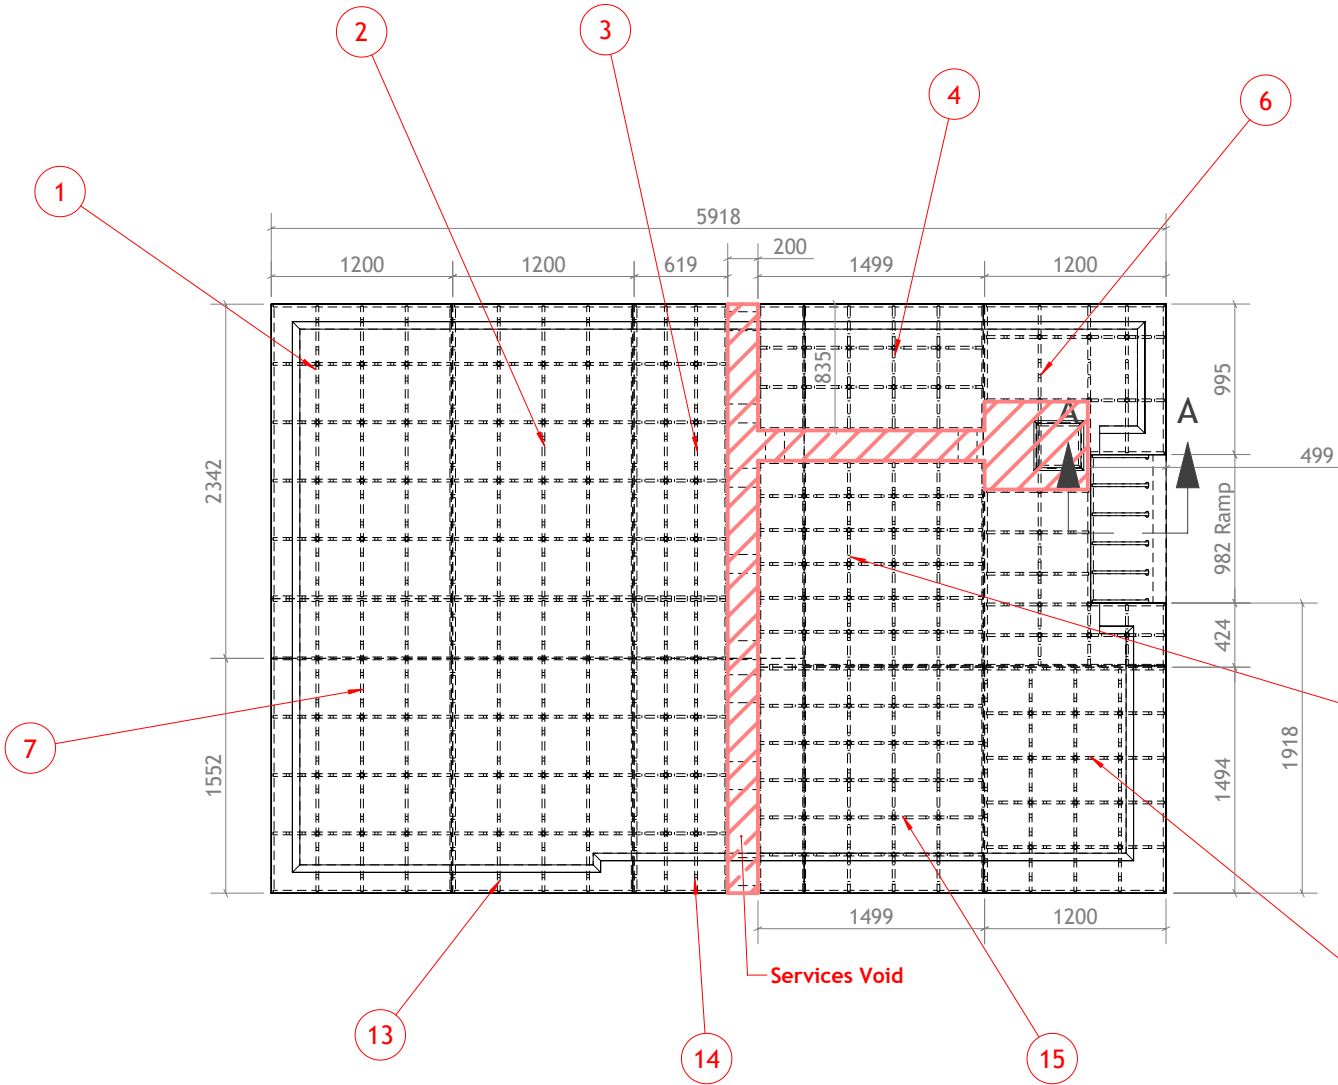

SECTION A-A
SCALE 1 : 10

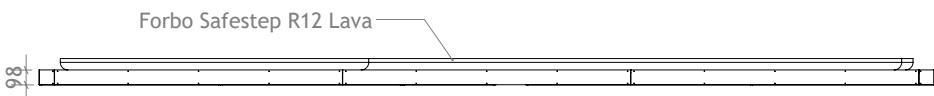

Weight of Item :- 313.79KG



Client:
VB Interiors Ltd

Address:
Westfield, White City, London

Project:
Lemonica Kiosk

Title:
Floor Assembly

Designer:
Jason Young






Date: 21/01/2026 Scale: 1:50 @ A3
Drawing No: 5271-03-01-GA
Dwg Sht: 1 of 1 Revision:

Unit 4
Arundel Works
Claywheels Lane
Sheffield
S6 1LZ

eclipsemanufacturingsolutions.co.uk

Date Last Saved:- 08 January 2026 15:05:21

ITEM NO.	PART NUMBER	Item	Weight(Kg)	Default/QTY.
1	5271-03-02-SA1	Perimeter Wall 1	149.80	1
2	5271-03-02-SA2	Perimeter Wall 2	90.96	1
3	5271-03-02-SA3	Perimeter Wall 3	90.66	1
4	5271-03-02-SA4	Perimeter Wall 4	78.23	1
5	5271-03-02-SA5	Perimeter Wall 5	52.15	1
6	5271-03-02-SA6	Perimeter Wall 6	82.95	1
7	5271-03-02-SA7	Perimeter Wall 7	62.94	1
8	5271-03-02-SA8	Perimeter Wall 8	23.06	1
9	5271-03-02-SA9	Perimeter Wall 9	65.26	1
10	5271-03-02-SA10	Hinged Gate	24.54	1
11	5271-03-10-SA5-SA1-01	Long Neon Signage	3.32 kg	1
12	5271-03-10-SA5-SA1-02	Stacked Neon Signage	2.71 kg	1
13	5271-03-02-GA-01	Corrugated Sheet	4.92	1
14	5271-03-02-GA-02	Corrugated Sheet	5.84	2
15	5271-03-02-GA-03	Corrugated Sheet	5.21	1
16	5271-03-02-GA-04	Corrugated Sheet	5.15	1
17	5271-03-02-GA-05	Corrugated Sheet	5.34	1
18	5271-03-02-GA-06	Corrugated Sheet	2.32	1
19	5271-03-10-SA1-01	Lemonade Acrylic Sign	18.40 kg	1
20	5271-03-10-SA1-02	Lemonade Acrylic Logo	3.55 kg	1
21	5271-03-05-SA1	Low Glass Panels	120.14	1
22	5271-03-05-SA2	High Glass Panels	51.90	1
23	5271-03-04-SA20-A	White Metro Tiles	67.20	1
24	5271-03-04-SA20-B	White Metro Tiles	10.53	1
25	5271-03-04-SA20-C	White Metro Tiles	3.25	1
26	5271-03-04-SA20-D	White Metro Tiles	1.43	1
27	5271-03-04-SA20-E	White Metro Tiles	0.85	1
28	5271-03-04-SA20-F	White Metro Tiles	5.01	1
29	5271-03-04-SA20-G	White Metro Tiles	28.72	1
30	5271-03-04-SA20-H	White Metro Tiles	6.11	1
31	Lemons 1	Lemons Set 1	65.01	1
32	Lemons 2	Lemons Set 2	25.49	1
33	Lemons 3	Lemons Set 3	12.75	1
34	Stainless Steel Double Socket	Stainless Steel DSSO		4
35	2G Dry Lining Back Box	2G Drying Back Box		4

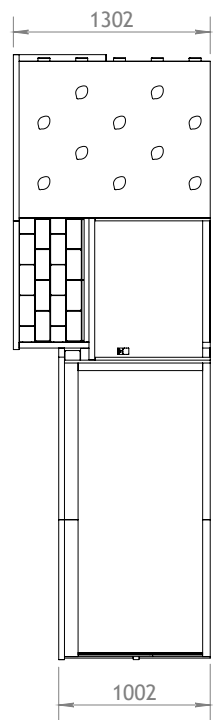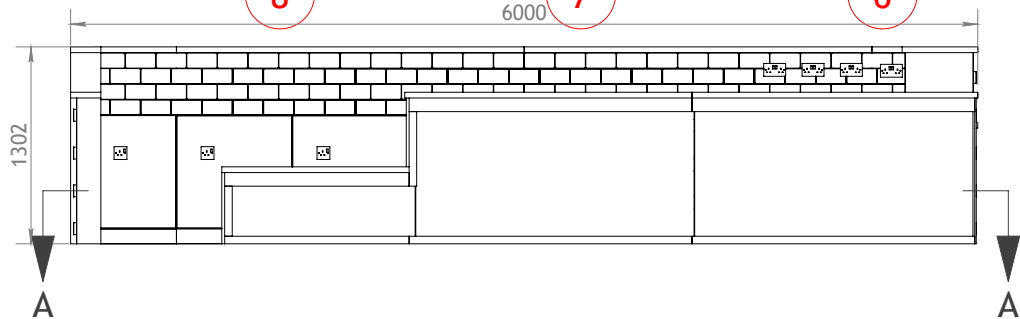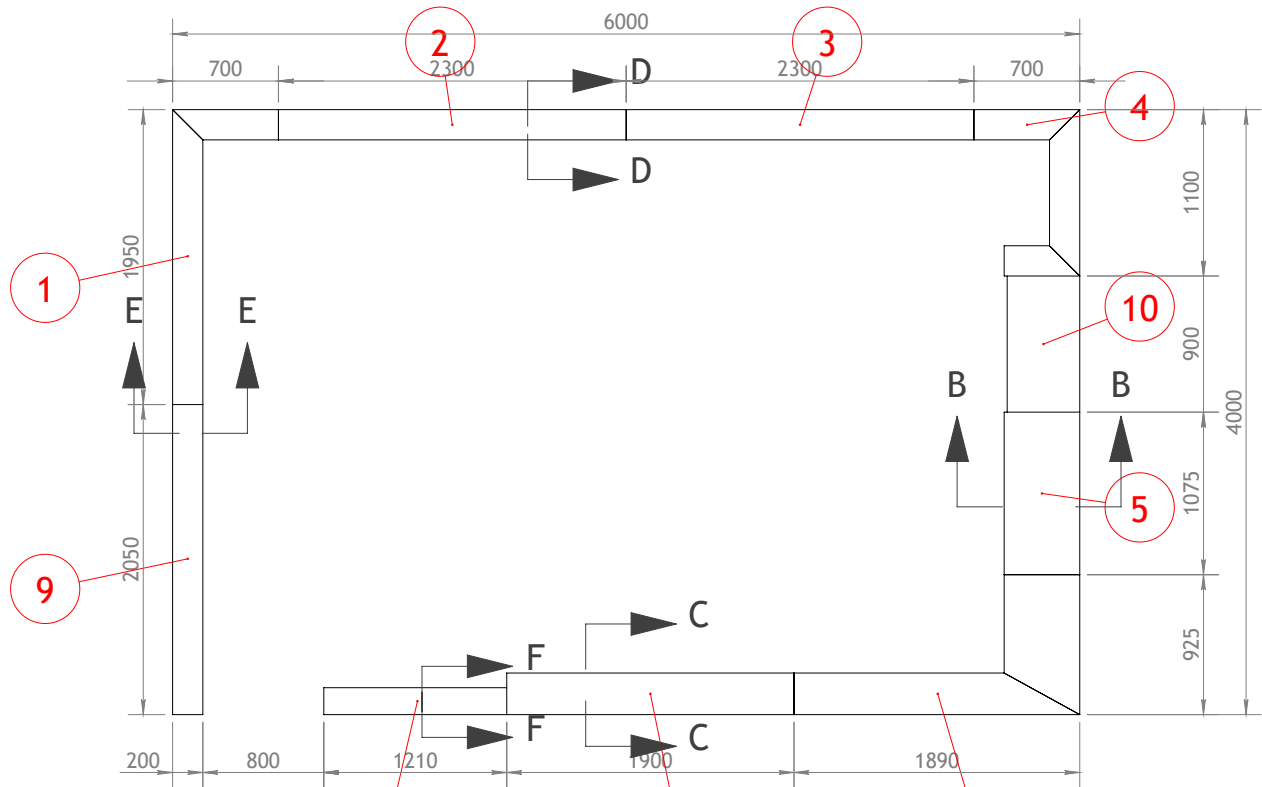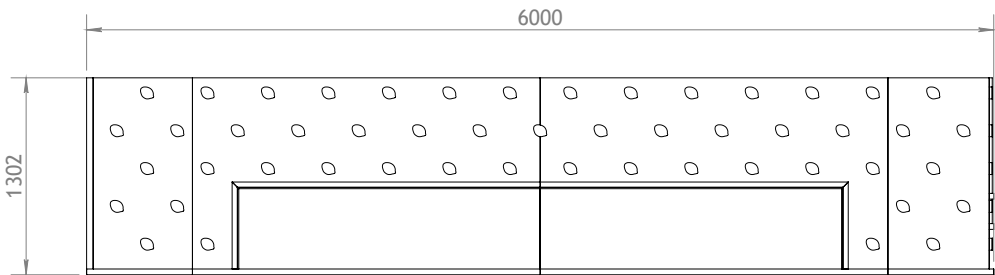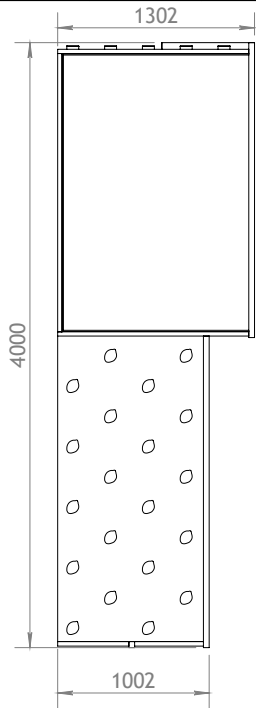

This drawing is the property of Eclipse Manufacturing Solutions: and is protected by the Design Copyright Act 1968. This drawing must not be copied or otherwise reproduced without the express written consent of Eclipse Manufacturing Solutions:
Do not scale from this drawing. All dimensions are to be confirmed on site and subject to building control and statutory approvals.

Rev:	Description:
A	
B	
C	
D	
E	
F	
G	

Weight of Item :- 1182.60KG



Client:
VB Interiors Ltd

Address:
Westfield, White City, London

Project:
Lemonica Kiosk

Title:
Walls

Designer:
Jason Young

Date: 17/12/2025 Scale: 1:50 @ A3
Drawing No:
5271-03-02-GA
Dwg Sht: 1 of 3 Revision:

Unit 4
Arundel Works
Claywheels Lane
Sheffield
S6 1LZ
eclipsemanufacturingsolutions.co.uk
Date Last Saved:- 17 December 2025 14:56:50

This drawing is the property of Eclipse Manufacturing Solutions: and is protected by the Design Copyright Act 1968. This drawing must not be copied or otherwise reproduced without the express written consent of Eclipse Manufacturing Solutions:

Do not scale from this drawing. All dimensions are to be confirmed on site and subject to building control and statutory approvals.

Rev: Description:

A
B
C
D
E
F
G

Weight of Item :- 1182.60KG



Client:
VB Interiors Ltd
Address:
Westfield, White City, London

Project:
Lemonica Kiosk
Title:
Walls
Horizontal Section


Designer:
Jason Young

Date: 17/12/2025 Scale: 1:20 @ A3
Drawing No: 5271-03-02-GA
Dwg Sht: 2 of 3 Revision:

Unit 4
Arundel Works
Claywheels Lane
Sheffield
S6 1LZ

eclipsemanufacturingsolutions.co.uk

Date Last Saved:- 17 December 2025 14:56:50

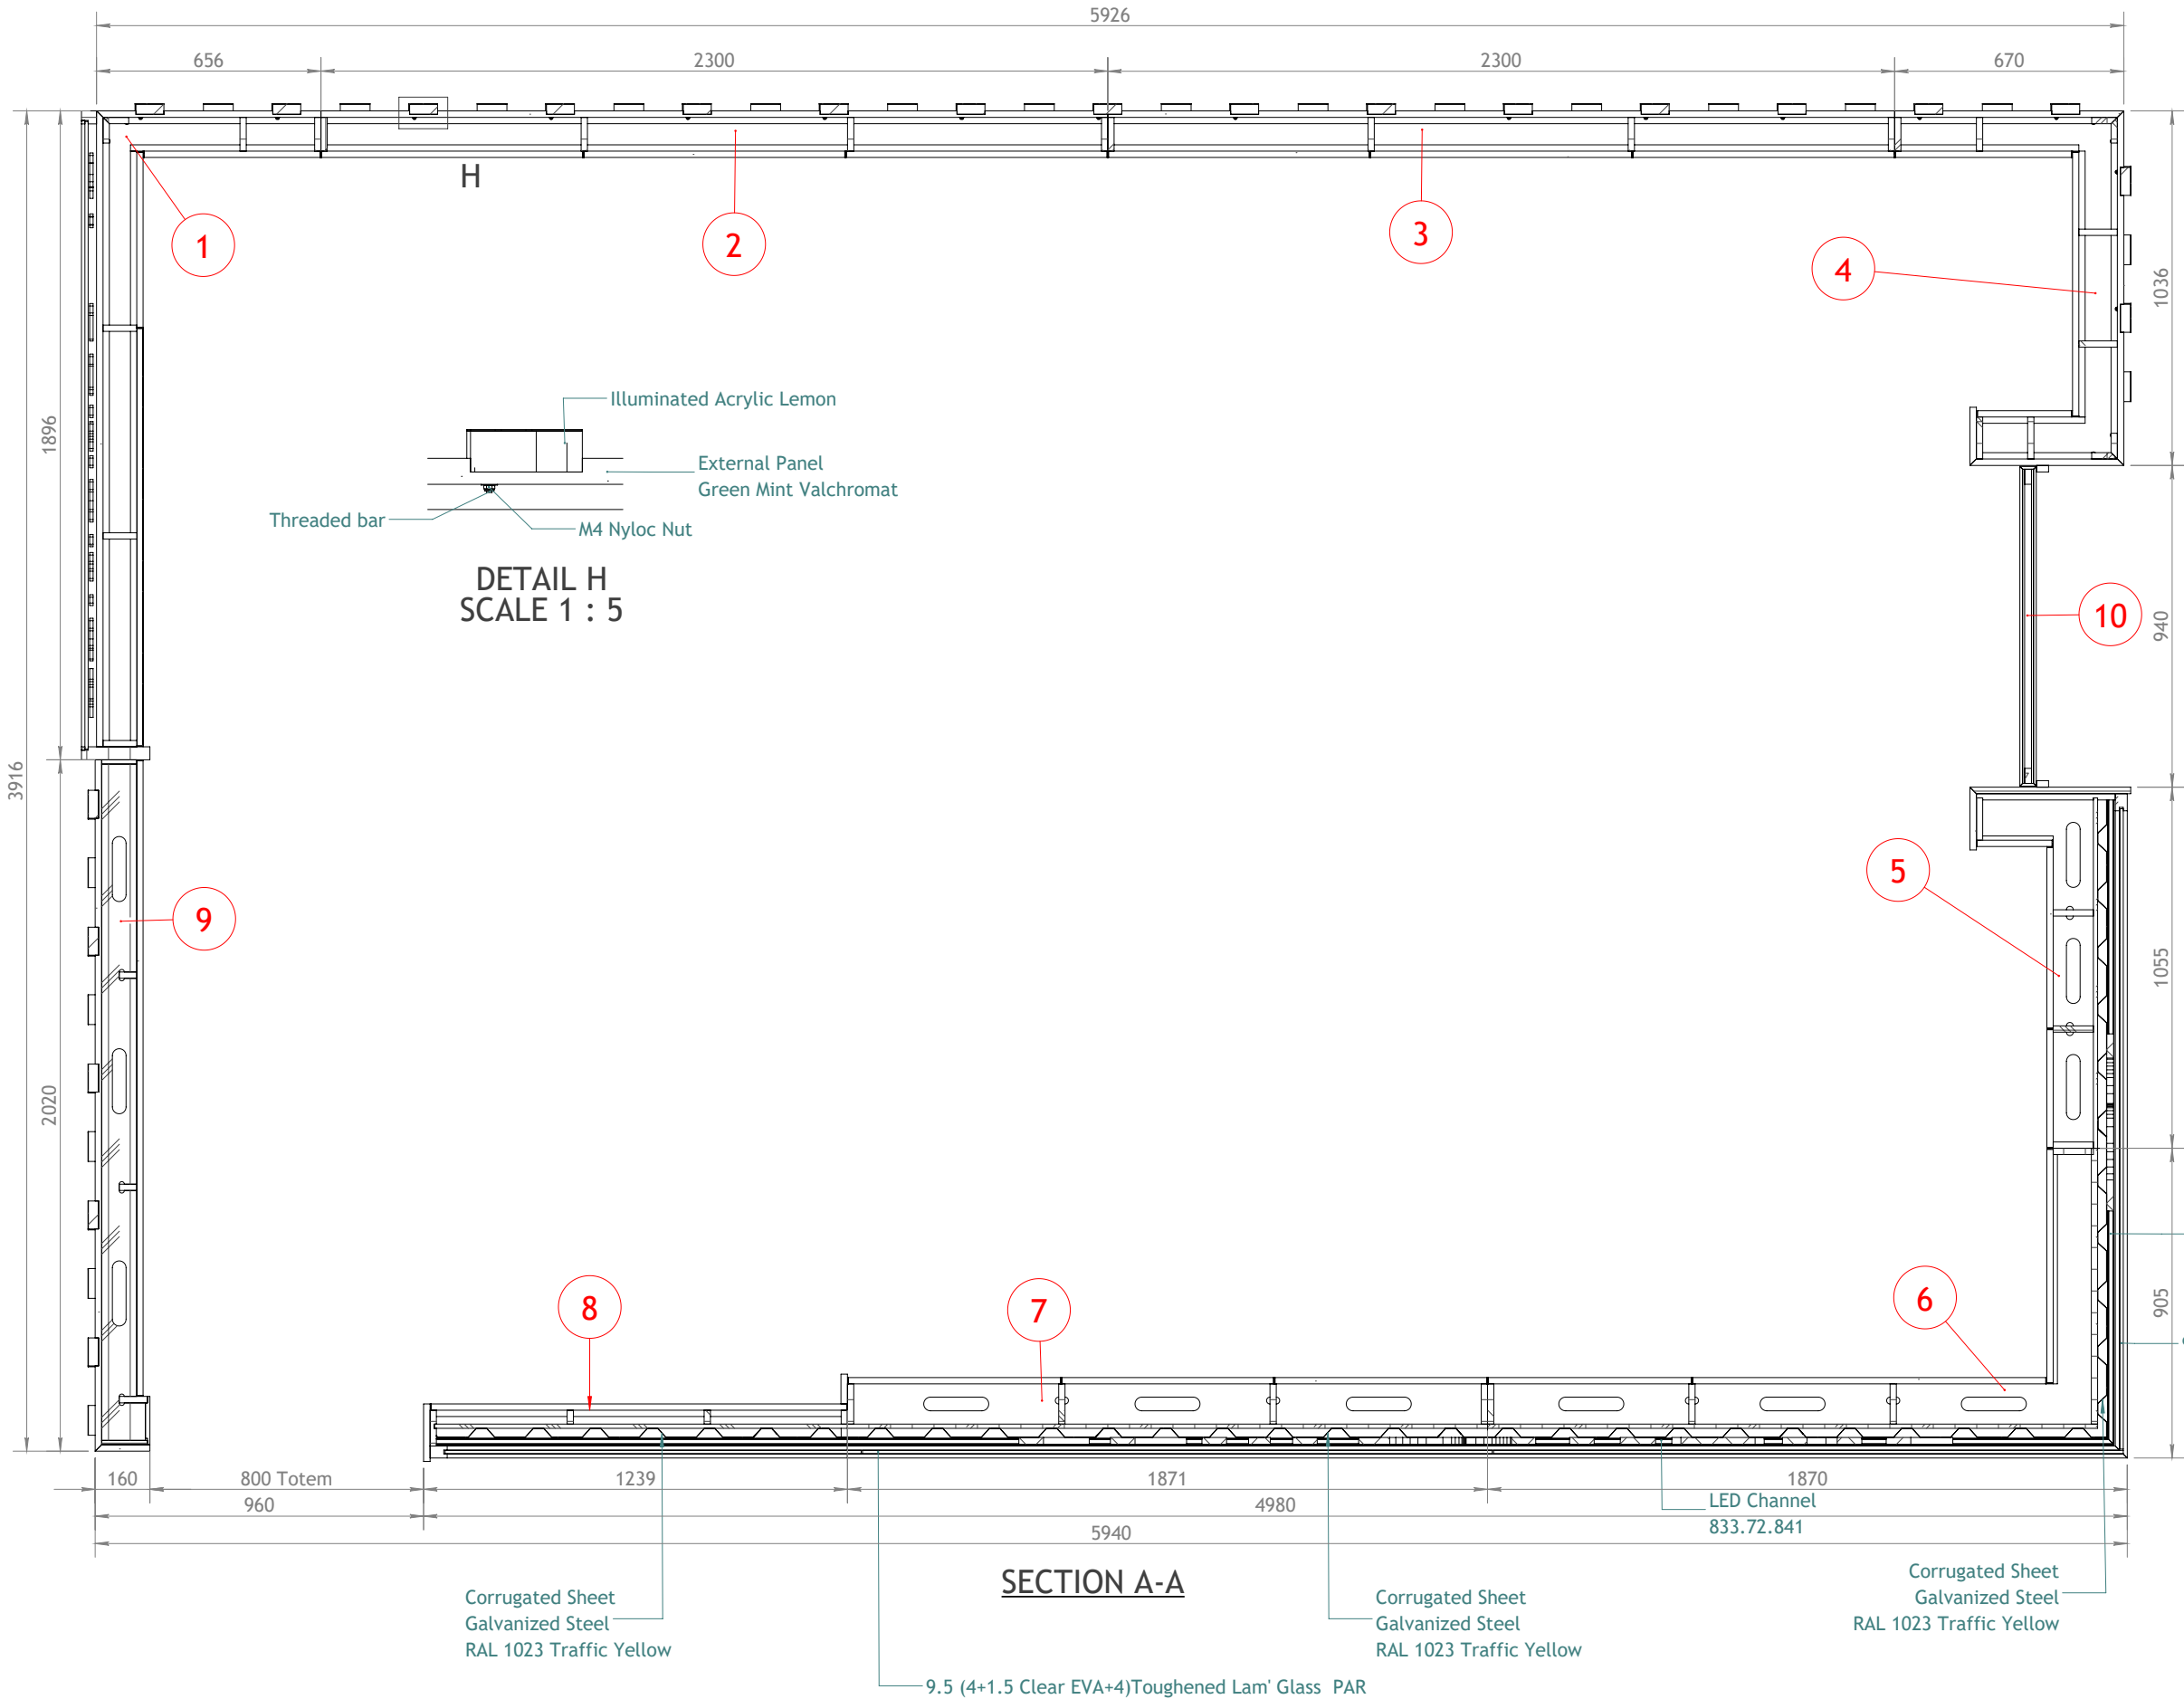

Rev: Description:

A

B

C

D

E

F

G

Weight of Item :- 1182.60KG



Client:
VB Interiors Ltd

Address:
Westfield, White City, London

Project:
Lemonica Kiosk

Title:
Walls
Vertical Sections

Designer:
Jason Young

Date: 17/12/2025 Scale: 1:10 @ A3

Drawing No:
5271-03-02-GA


Dwg Sht: 3 of 3

Revision:


Unit 4
Arundel Works
Claywheels Lane
Sheffield
S6 1LZ

eclipsemanufacturingsolutions.co.uk


Date Last Saved:- 17 December 2025 14:56:50

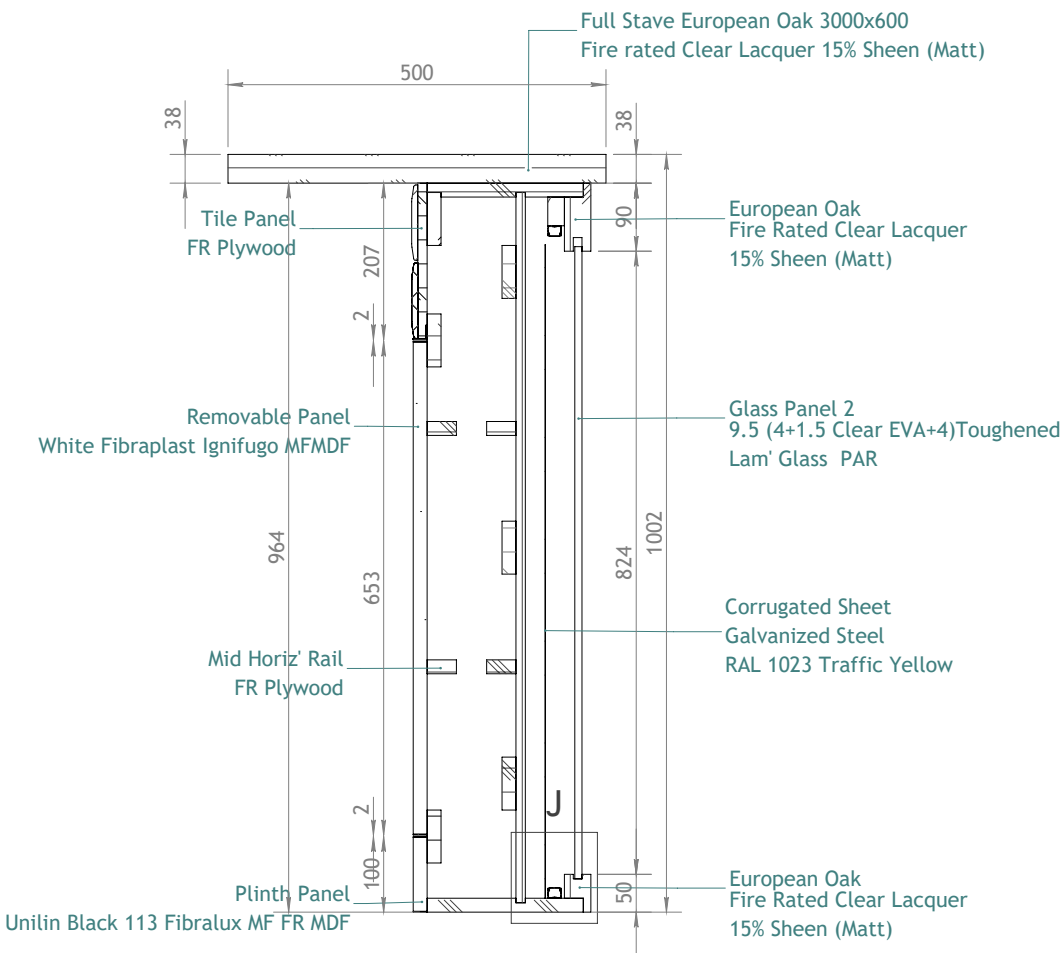



SECTION B-B

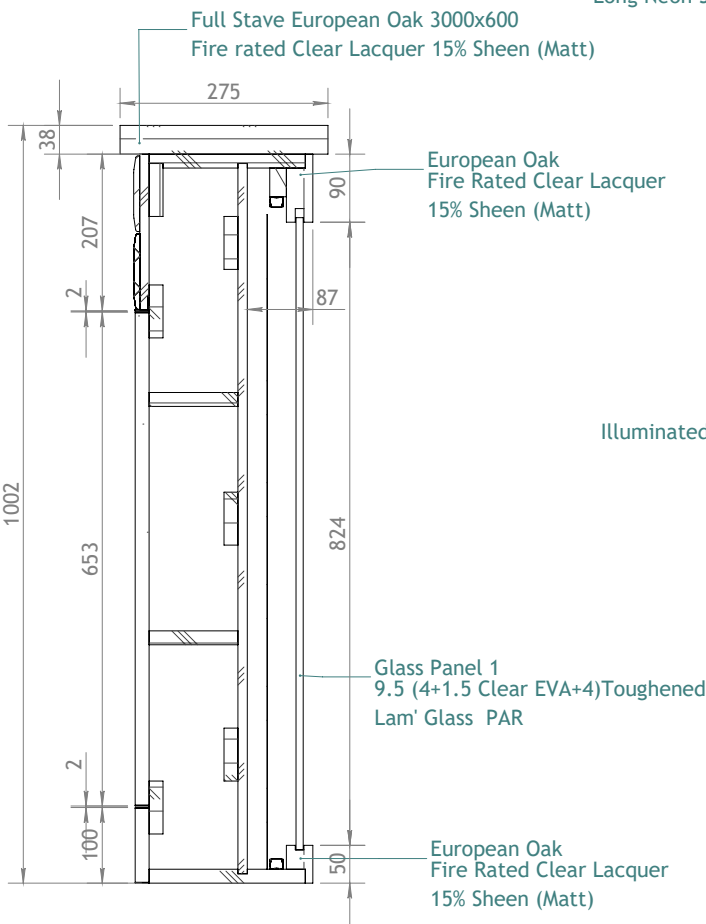


SECTION C-C

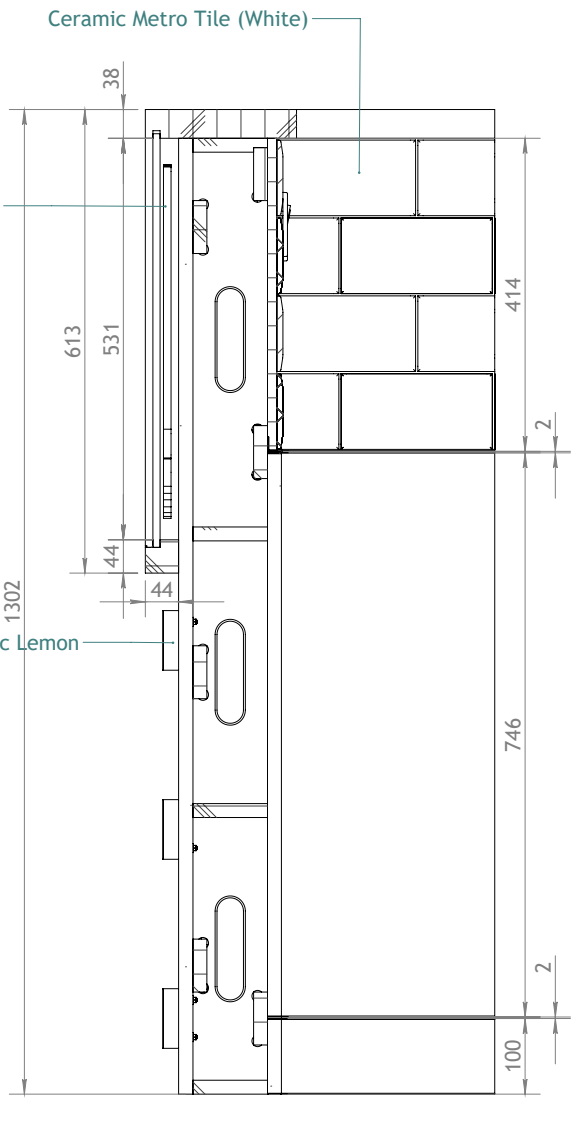

SECTION D-D

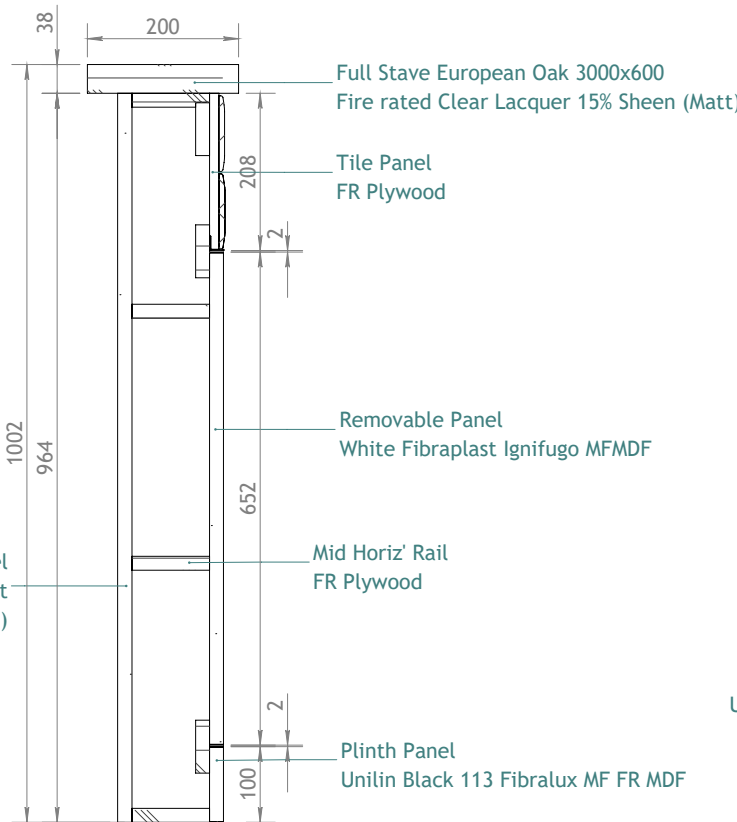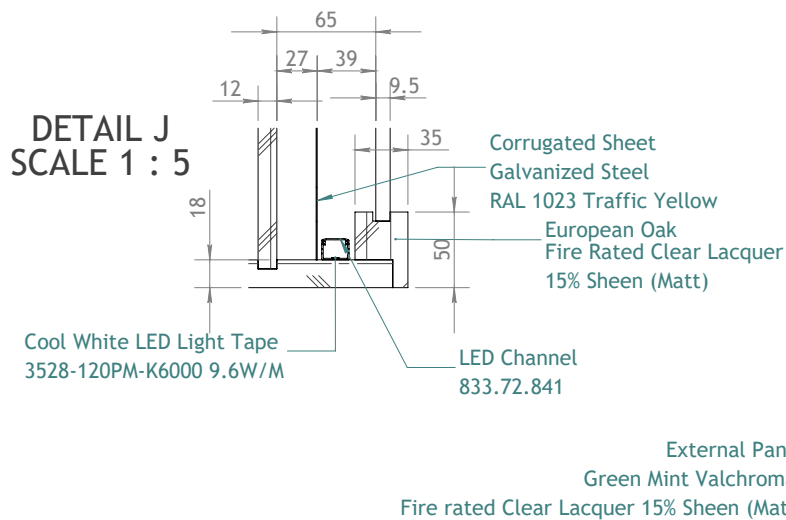

SECTION E-E

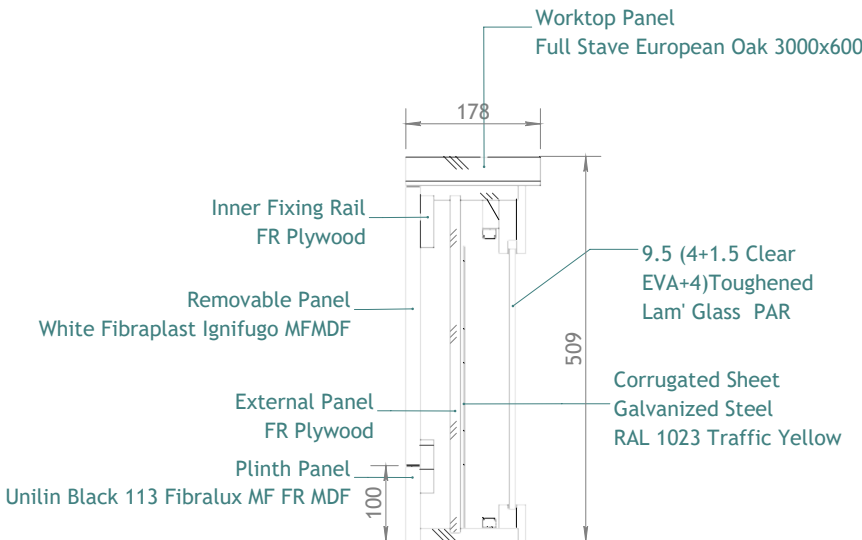

SECTION F-F

Rev: Description:

A
B
C
D
E
F
G

Weight of Item :- 97.43KG



Client:
VB Interiors Ltd

Address:
Westfield, White City, London

Project:
Lemonica Kiosk

Title:
Display Totem

Designer:
Jason Young

Date: 17/12/2025 Scale: 1:20 @ A3


Drawing No:
5271-03-03-SA1

Dwg Sht: 1 of 1 Revision:

Unit 4
Arundel Works
Claywheels Lane
Sheffield
S6 1LZ

eclipsemanufacturingsolutions.co.uk

Date Last Saved:- 17 December 2025 16:06:50

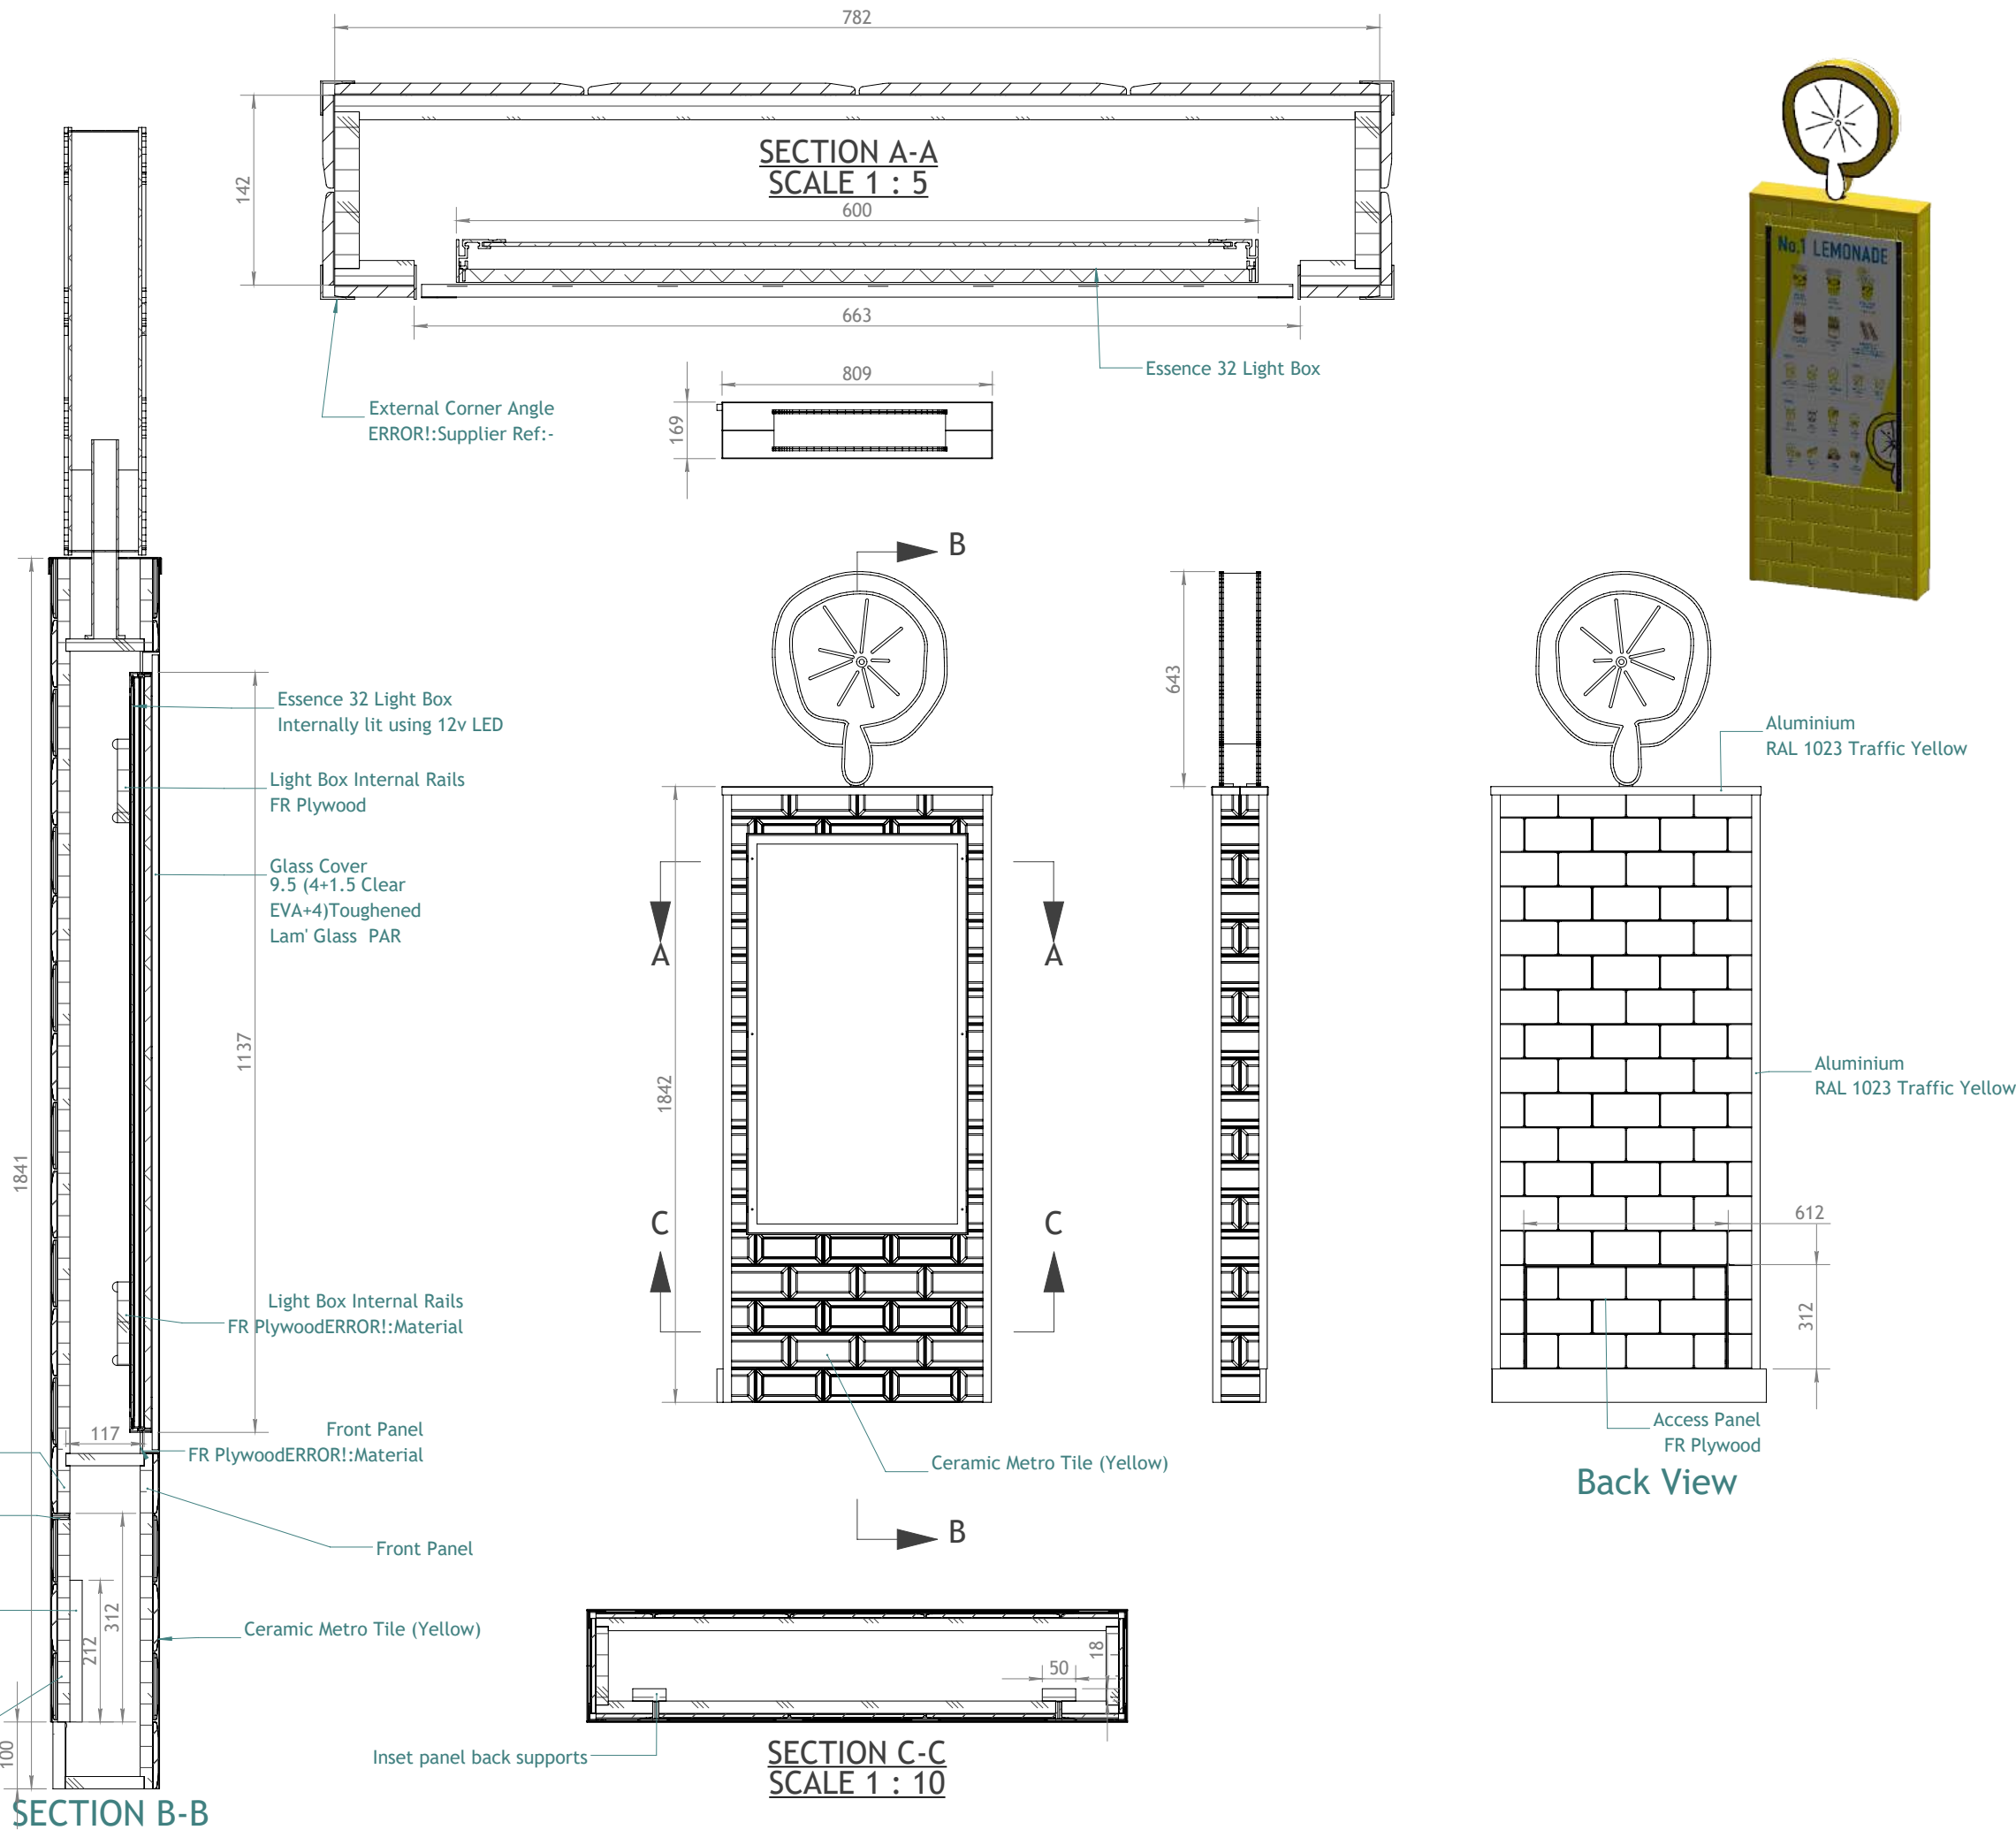

Rev:	Description:
A	21/01/26 Front panel now Glass
B	
C	
D	
E	
F	
G	

Weight of Item :- 6.85KG



Client:
VB Interiors Ltd

Address:
Westfield, White City, London

Project:
Lemonica Kiosk

Title:
Counter Top Menu Board



Designer:
Steve Foster

Date: 22/01/2026 Scale: 1:10 @ A3
Drawing No: 5271-03-06-SA1
Dwg Sht: 1 of 1 Revision: A



Unit 4
Arundel Works
Claywheels Lane
Sheffield
S6 1LZ

eclipsemanufacturingsolutions.co.uk



Date Last Saved:- 21 January 2026 15:04:13

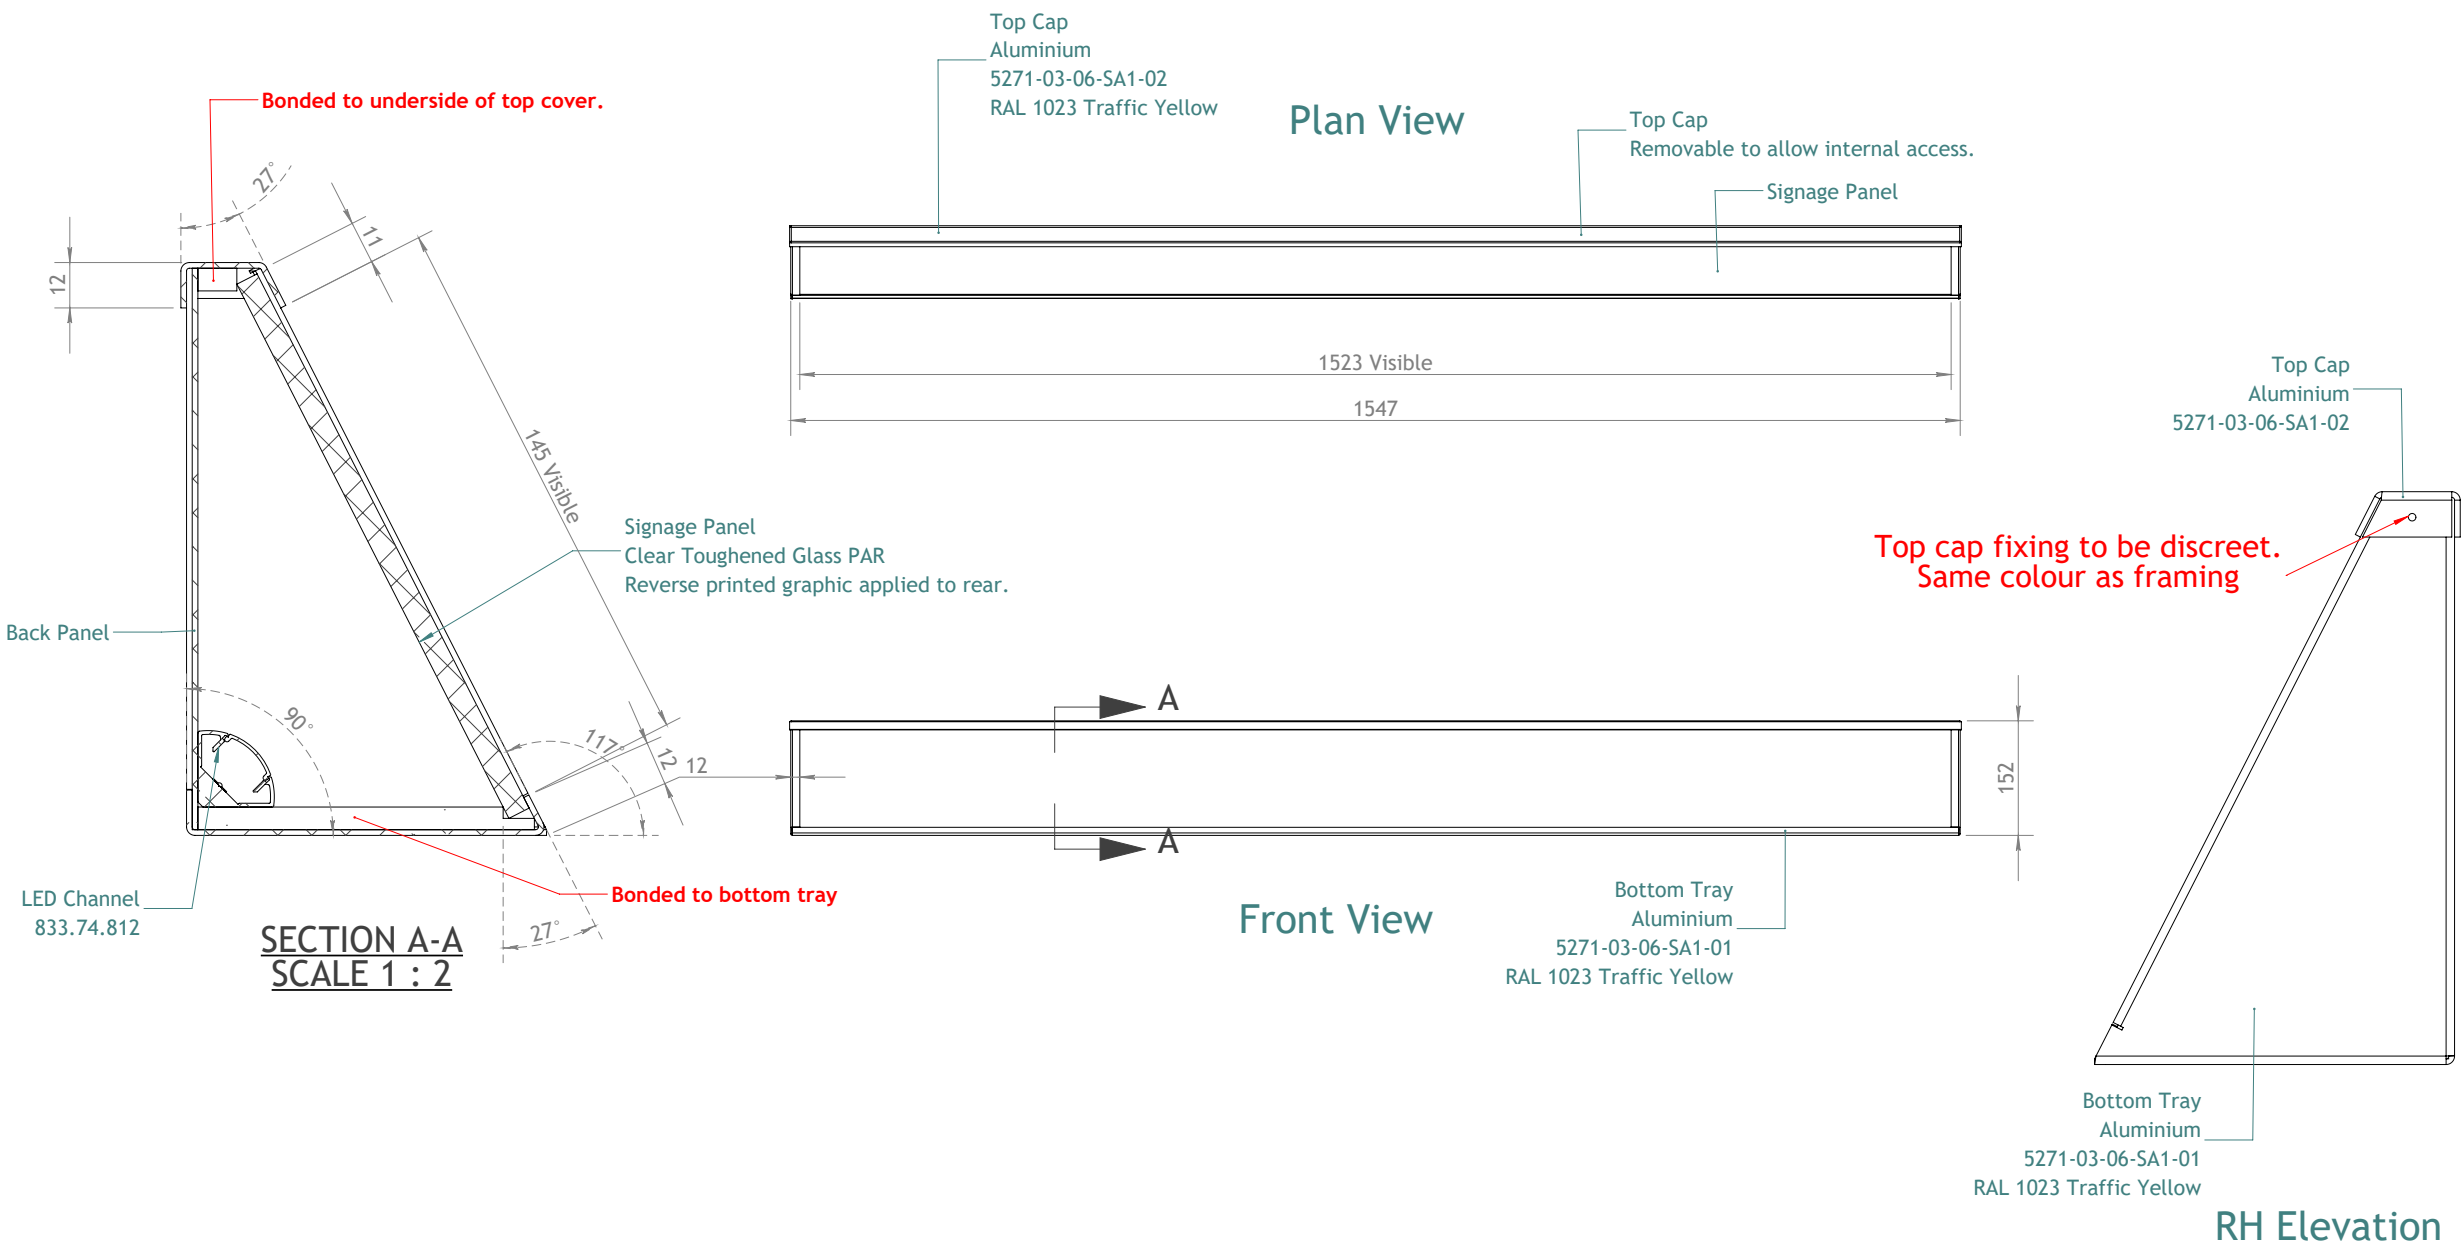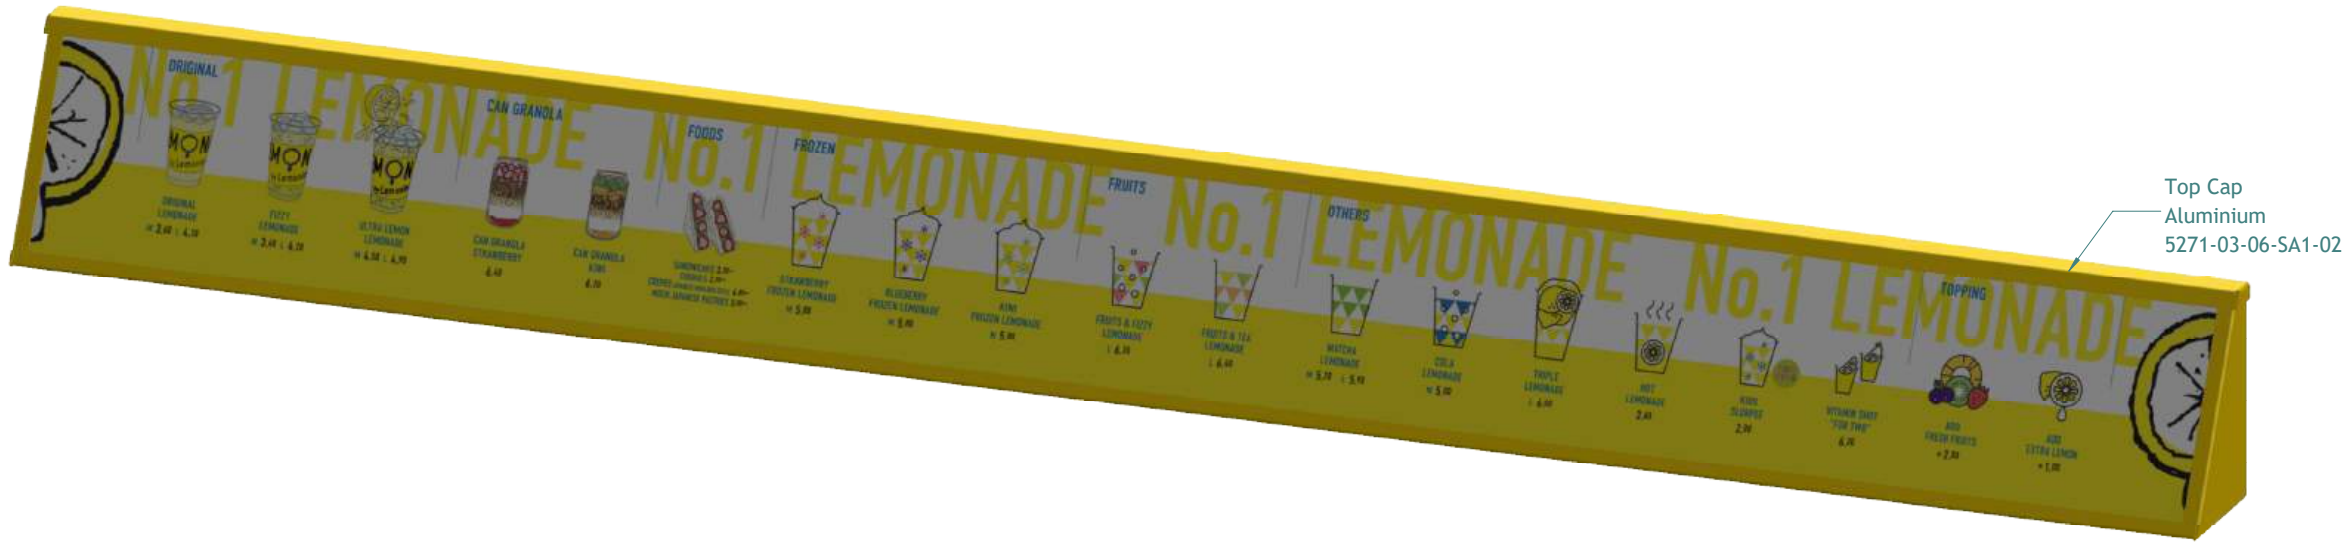


ITEM NO.	PART NUMBER	Item	Weight(Kg)	QTY.
1	5271-03-07-SA2	Stainless Steel Worktop	34.94	1
2	5271-03-07-GA-01	Backing Board for sink	15.80	1
3	5271-03-07-GA-02	Balancer	1.72	1
4	Seville Pull Out Spray Mixer	Pull Out Spray Mixer Tap		1
5	Grease Trap	Grease Trap	1.62 kg	1
6	5271-03-07-GA-03	Fixing Batten	0.76	1
7	5271-03-07-SA1	Stainless Steel Worktop	0.00	1
8	5271-03-07-SA6	Tiered Unit	3.38	2
9	5271-03-07-SA3	Tiered Unit	3.82	1
10	5271-03-07-SA4	Stainless Steel Worktop	12.13	1
11	300mm Hand Wash	300mm Dia Handwash Basin	2.33 kg	1
12	5271-03-07-GA-04	Plinth Panel	1.27 kg	1
13	5271-03-07-GA-06	Folded Shelf	6.96 kg	2
14	5271-03-07-SA5	Wide Base Unit	43.65	1
15	Swirl Bonda Mixer	Swirl Bonda Mixer Tap	0.07 kg	1

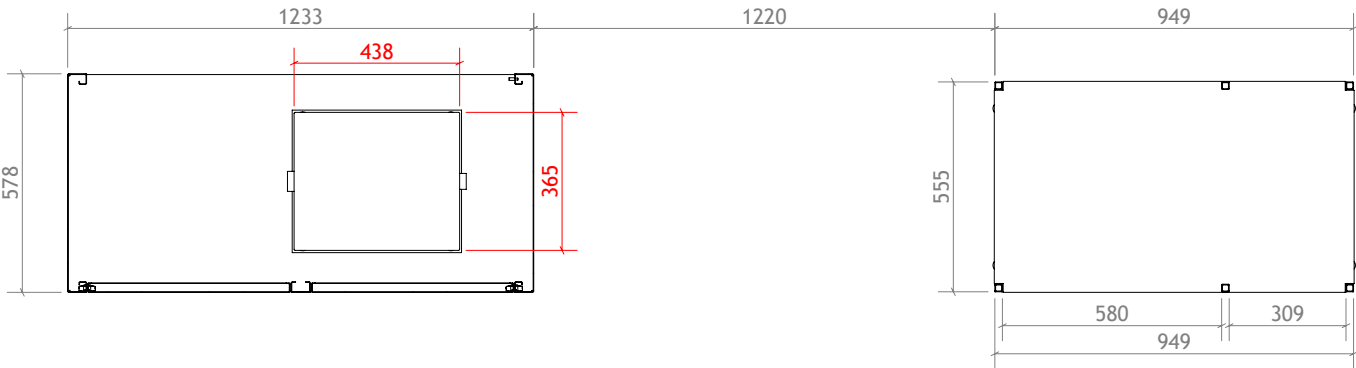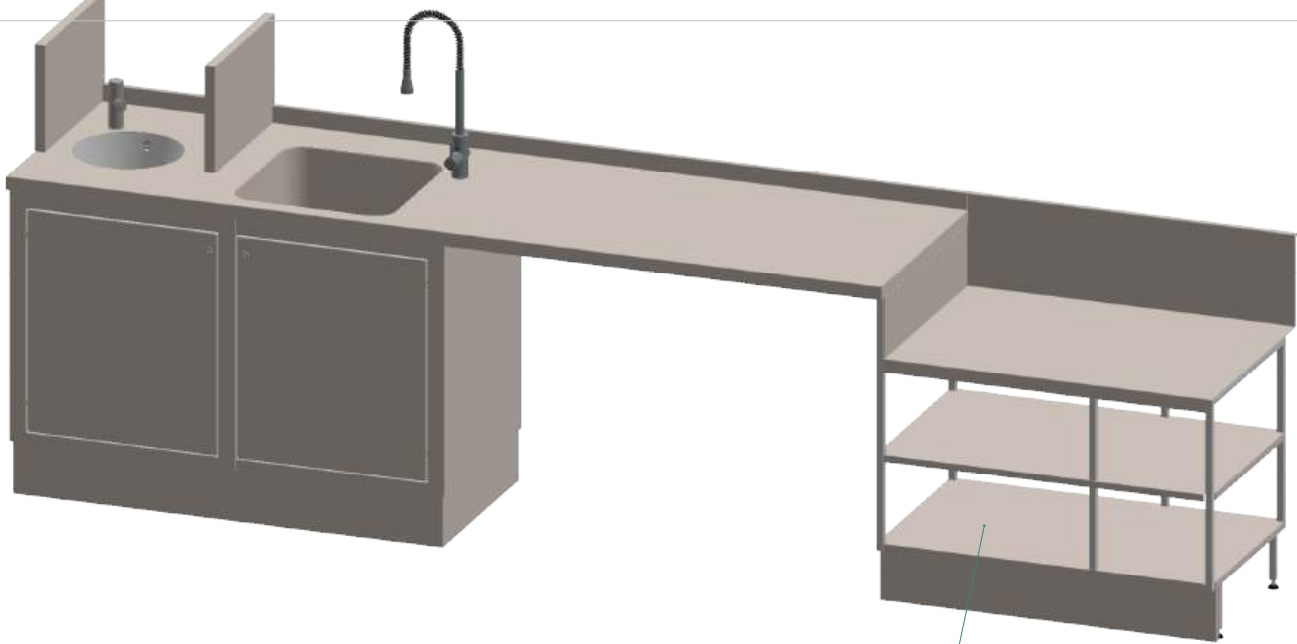

SECTION V-V

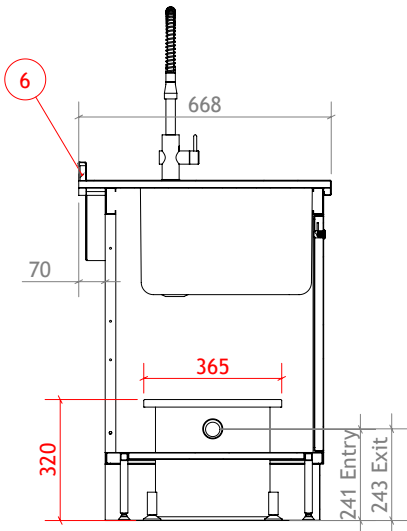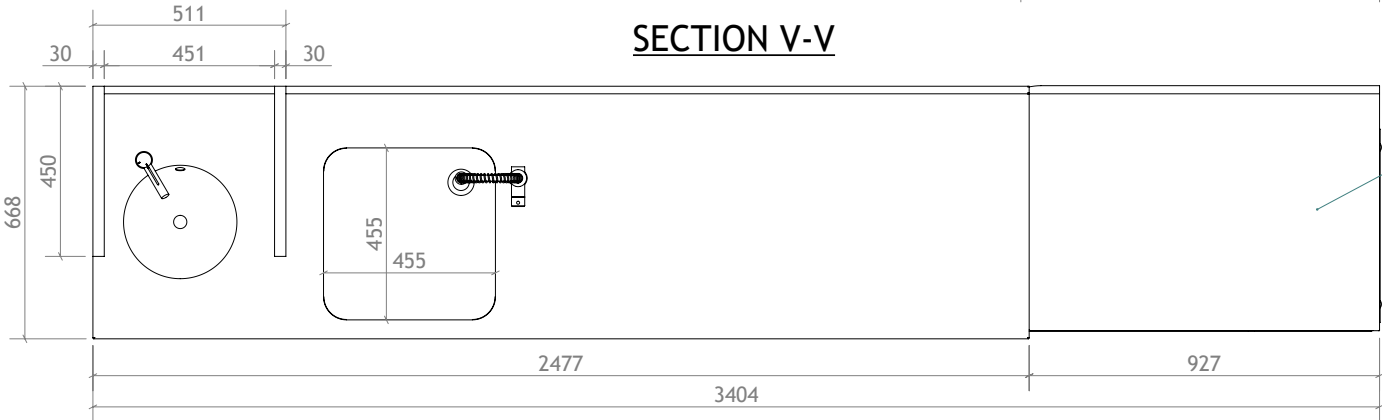

SECTION U-U

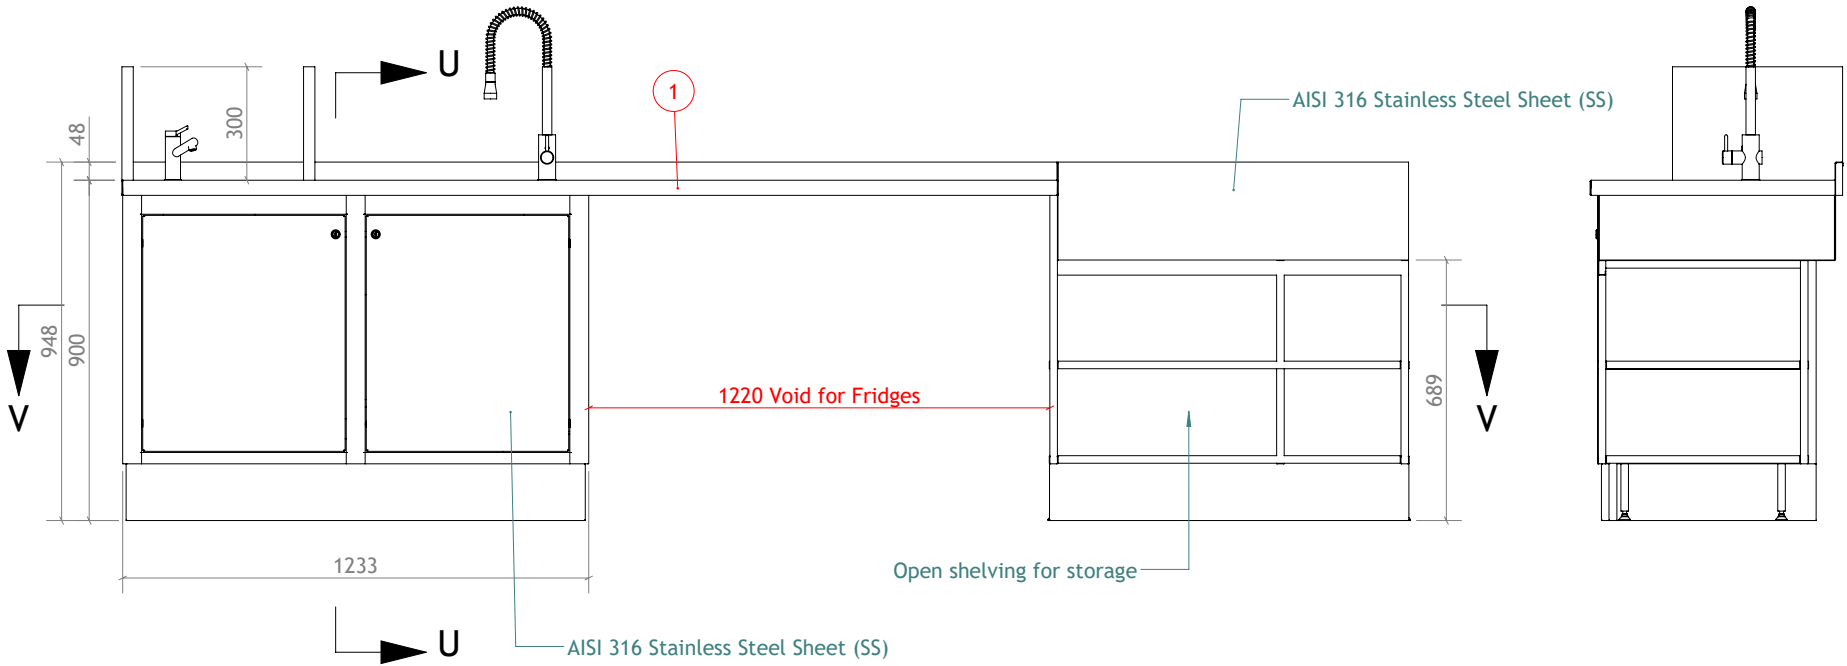

This drawing is the property of Eclipse Manufacturing Solutions: and is protected by the Design Copyright Act 1968. This drawing must not be copied or otherwise reproduced without the express written consent of Eclipse Manufacturing Solutions: Do not scale from this drawing. All dimensions are to be confirmed on site and subject to building control and statutory approvals.		
Rev:	Description:	Drawn:
A	30/01/04 Grease Trap Added	JY
B		
C		
D		
E		
F		
G		

Weight of Item :- 139.27KG



Client:
Optimusblu

Address:
Westfield London

Project:
Smatcha Kiosk

Title:
Stainless Steel Unitry

Designer:
Jason Young


Date: 18/12/2025 Scale: 1:20 @ A3
Drawing No: 5271-03-07-GA
Dwg Sht: 1 of 1 Revision: A

Unit 4
Arundel Works
Claywheels Lane
Sheffield
S6 1LZ


eclipsemanufacturingsolutions.co.uk

Date Last Saved:- 18 December 2025 15:42:55



ITEM NO.	PART NUMBER	Item	Weight(Kg)	QTY.
1	5271-03-08-SA2	Stainless Steel Worktop	45.09	1
2	5271-03-08-GA-01	Backing Board for sink	20.11	1
3	5271-03-08-GA-02	Balancer	2.19	1
4	5271-03-08-GA-03	Fixing Batten	1.08	1
5	5271-03-08-SA5	Wide Base Unit	26.62	1
6	5271-03-08-SA6	Wide Base Unit	38.40	1
7	5271-03-08-SA7	Wide Base Unit	46.61	1
8	5271-03-08-SA8	Wide Base Unit	44.80	1
9	5271-03-08-GA-04	Removable Plinth Panel	5.76 kg	1
10	Ice Core Machine	Ice Core Machine	116.96 kg	1
11	5048-03-08-GA-05	Make-up Table	9.89	1
12	CO2 Cylinder	CO2 Cylinder	1.23 kg	1
13	Crepe Machine	Crepe maker	1.28 kg	1
14	Staychill 525 x 325	Staychill Tray 325x525	0.80 kg	1

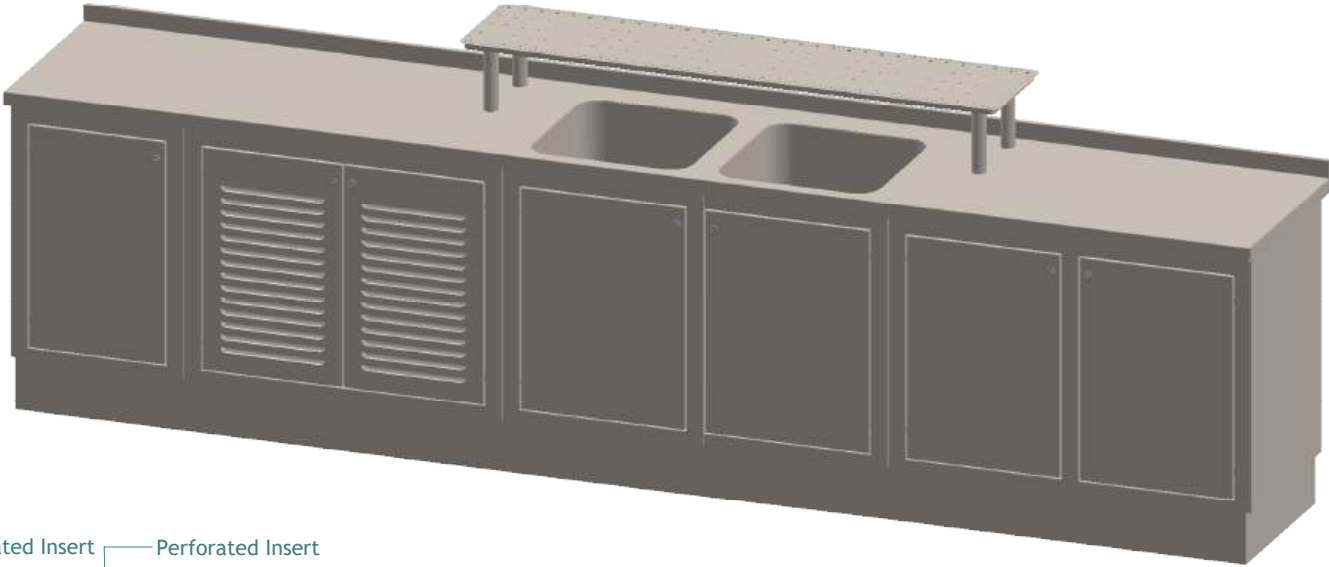


This drawing is the property of Eclipse Manufacturing Solutions: and is protected by the Design Copyright Act 1968. This drawing must not be copied or otherwise reproduced without the express written consent of Eclipse Manufacturing Solutions: Do not scale from this drawing. All dimensions are to be confirmed on site and subject to building control and statutory approvals.		
Rev:	Description:	Drawn:
A		JY
B		
C		
D		
E		
F		
G		

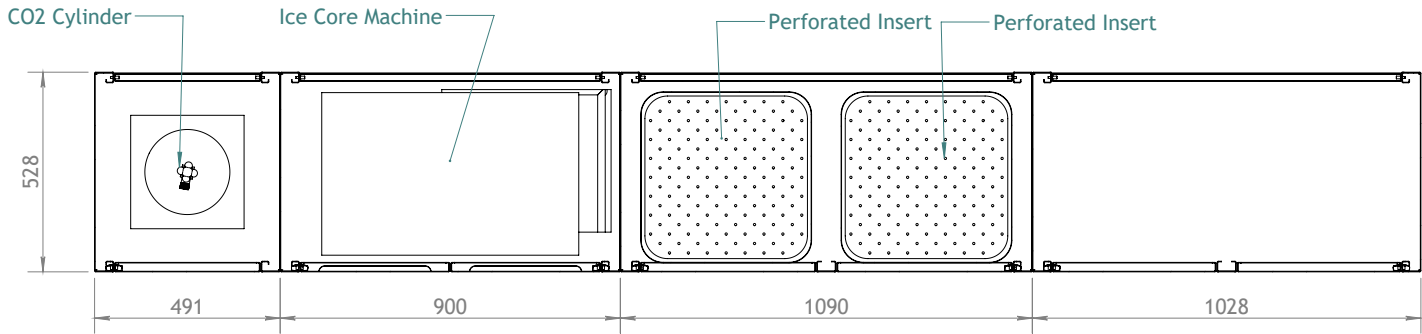

SECTION V-V

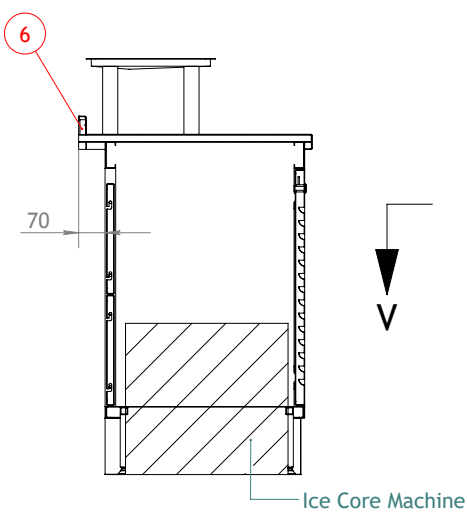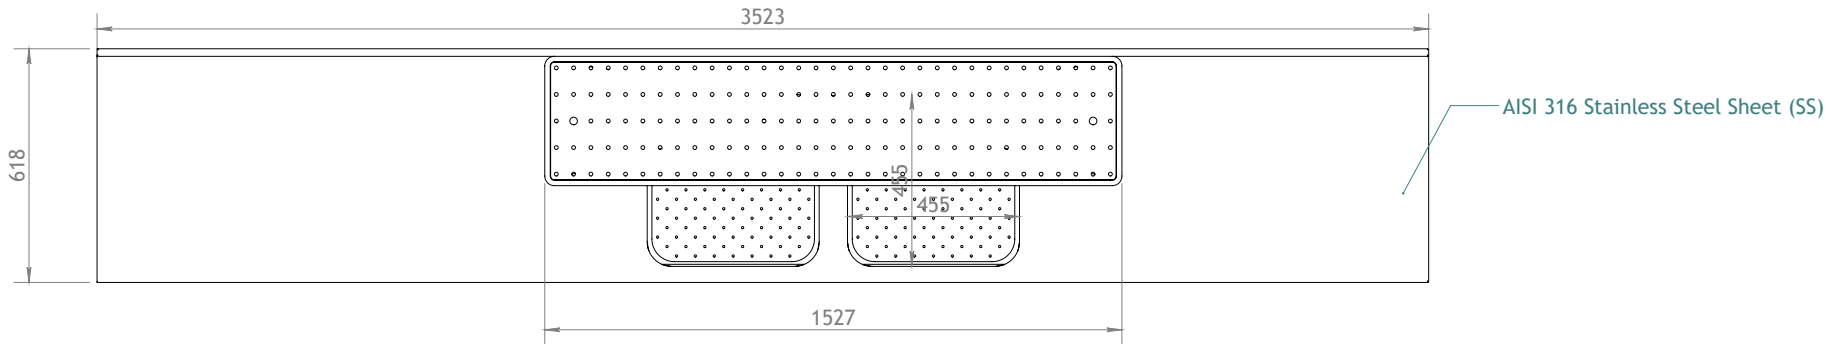

SECTION U-U

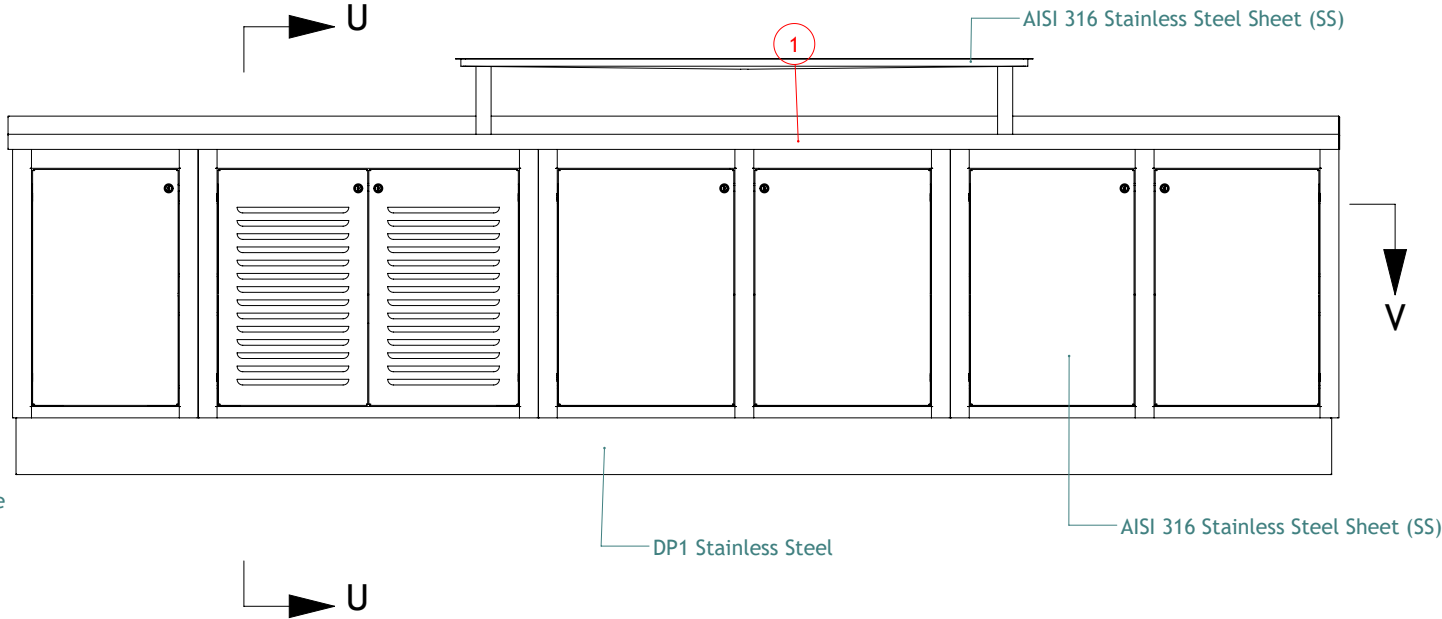

Weight of Item :- 358.72KG



Client:
VB Interiors Ltd

Address:
Westfield, White City, London

Project:
Lemonica Kiosk

Title:
Front Stainless Unitry

Designer:
Jason Young

Date: 18/12/2025 Scale: 1:20 @ A3
Drawing No: 5271-03-08-GA
Dwg Sht: 1 of 1 Revision:




Unit 4
Arundel Works
Claywheels Lane
Sheffield
S6 1LZ

eclipsemanufacturingsolutions.co.uk

Date Last Saved:- 08 December 2025 13:30:39

ITEM NO.	PART NUMBER	Item	Weight(Kg)	QTY.
1	5271-03-09-GA-01	Plinth Panel	1.02 kg	1
2	5271-03-09-SA2	Wide Base Unit	16.26	1

No back panel

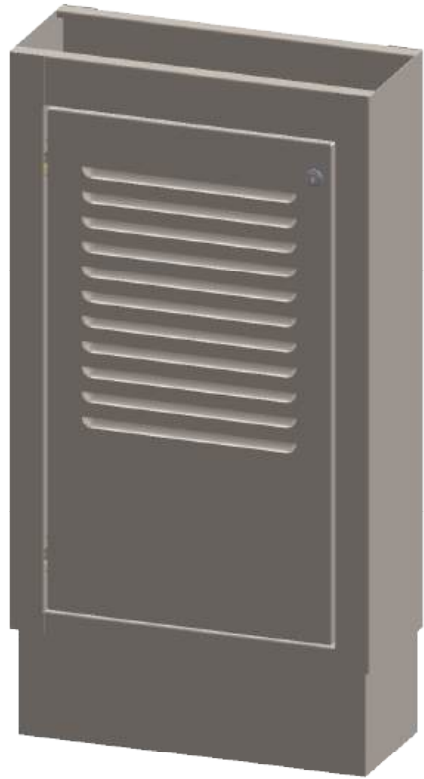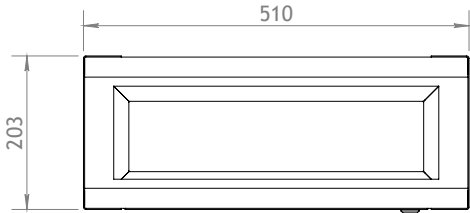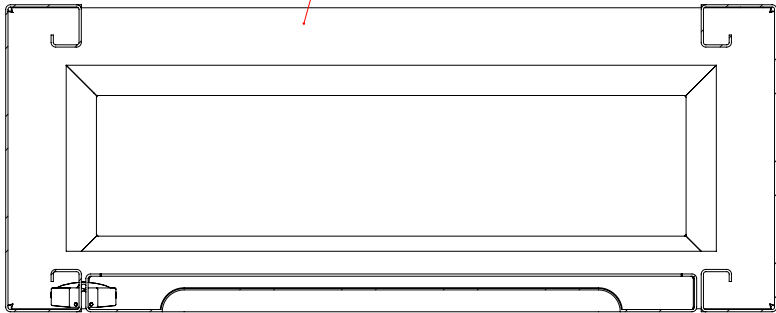

This drawing is the property of Eclipse Manufacturing Solutions: and is protected by the Design Copyright Act 1968. This drawing must not be copied or otherwise reproduced without the express written consent of Eclipse Manufacturing Solutions:
Do not scale from this drawing. All dimensions are to be confirmed on site and subject to building control and statutory approvals.

Rev:	Description:	Drawn:
A		JY
B		
C		
D		
E		
F		
G		

Weight of Item :- 17.28KG





Client:
VB Interiors Ltd
Address:
Westfield, White City, London
Project:
Lemonica Kiosk
Title:
Front Stainless Unitry
Designer:
Jason Young


Date: 18/12/2025 Scale: 1:10 @ A3
Drawing No:
5271-03-09-GA
Dwg Sht: 1 of 1 Revision:

Unit 4
Arundel Works
Claywheels Lane
Sheffield
S6 1LZ
eclipsemanufacturingsolutions.co.uk
Date Last Saved:- 08 December 2025 13:34:41

No back panel


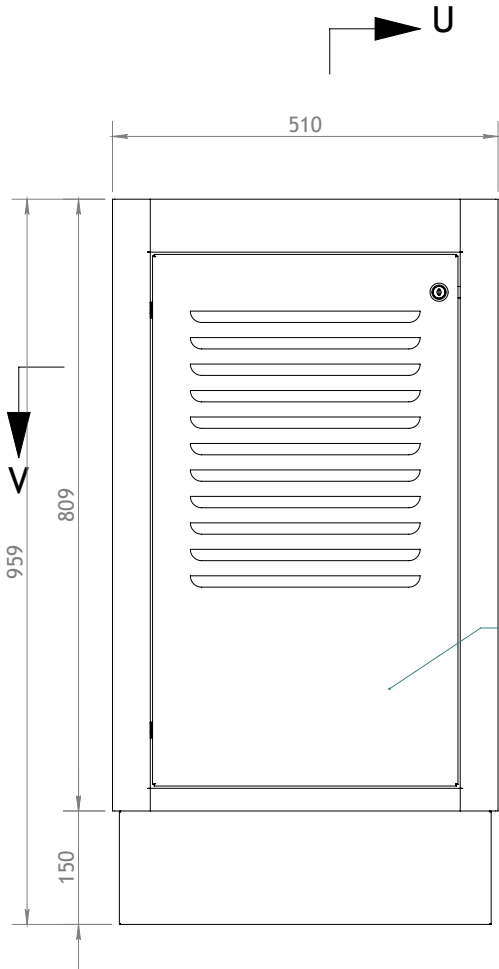
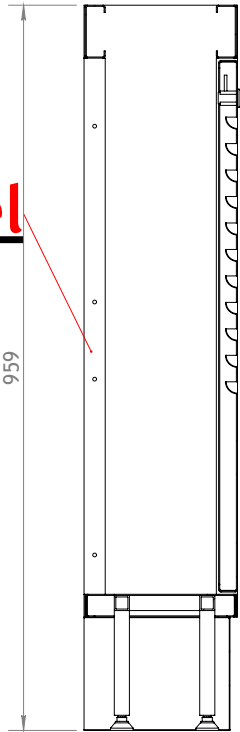


AISI 316 Stainless Steel Sheet (SS)

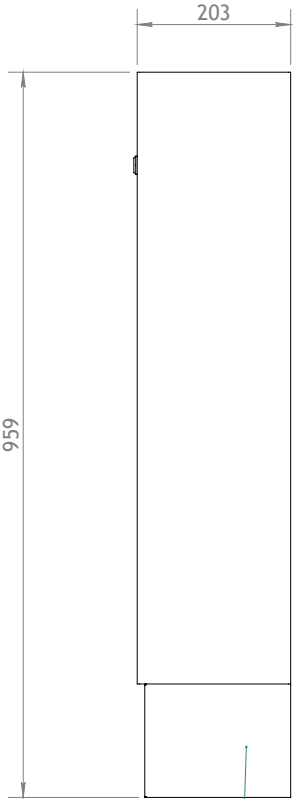

DP1 Stainless Steel

Rev:	Description:
A	
B	
C	
D	
E	
F	
G	

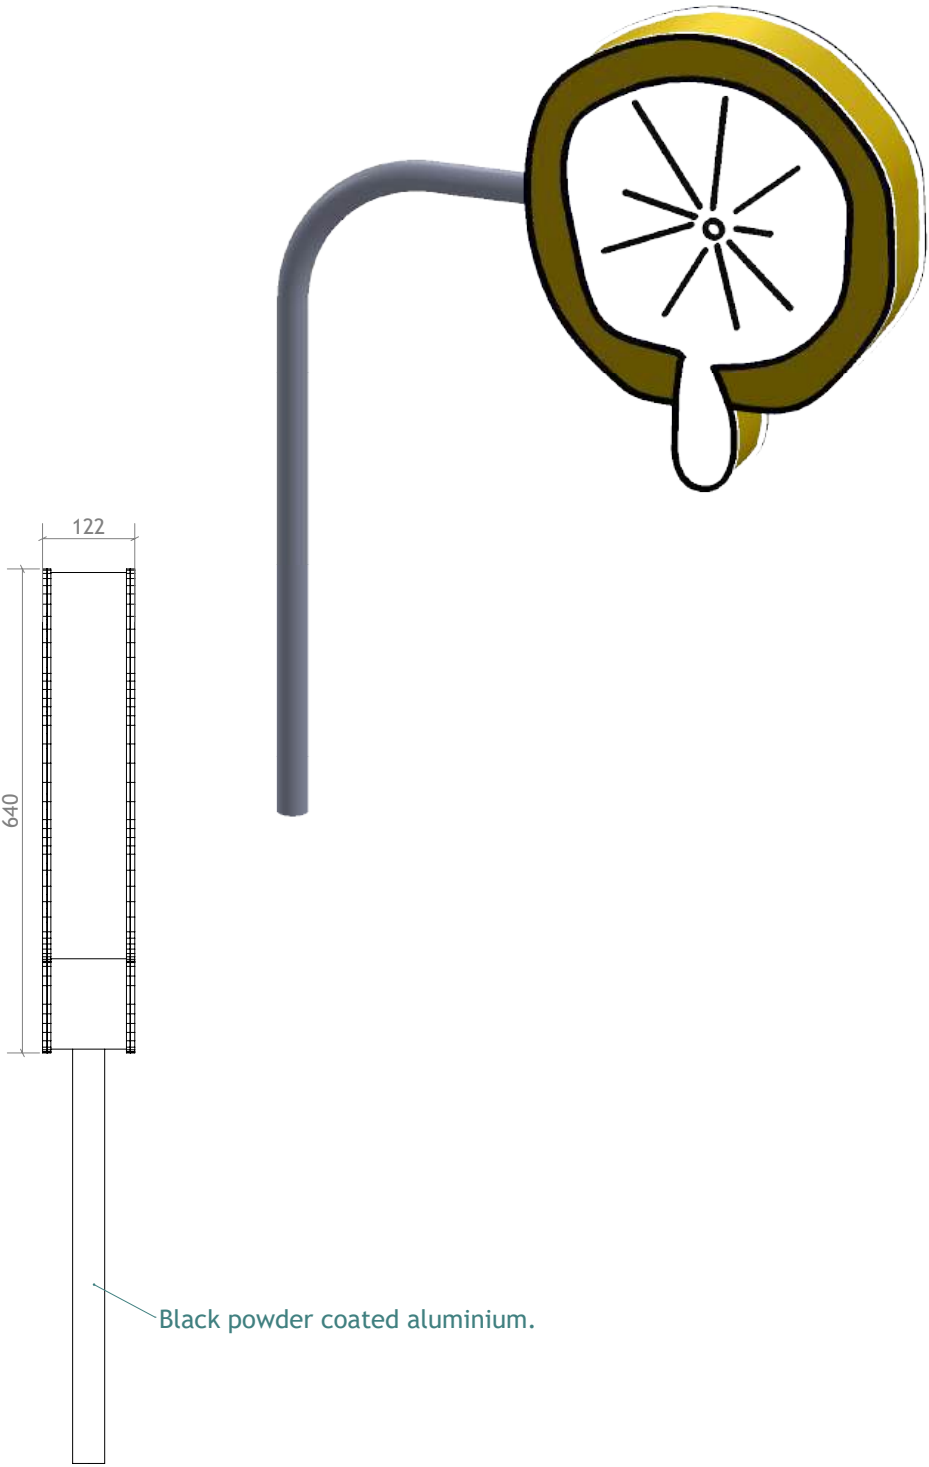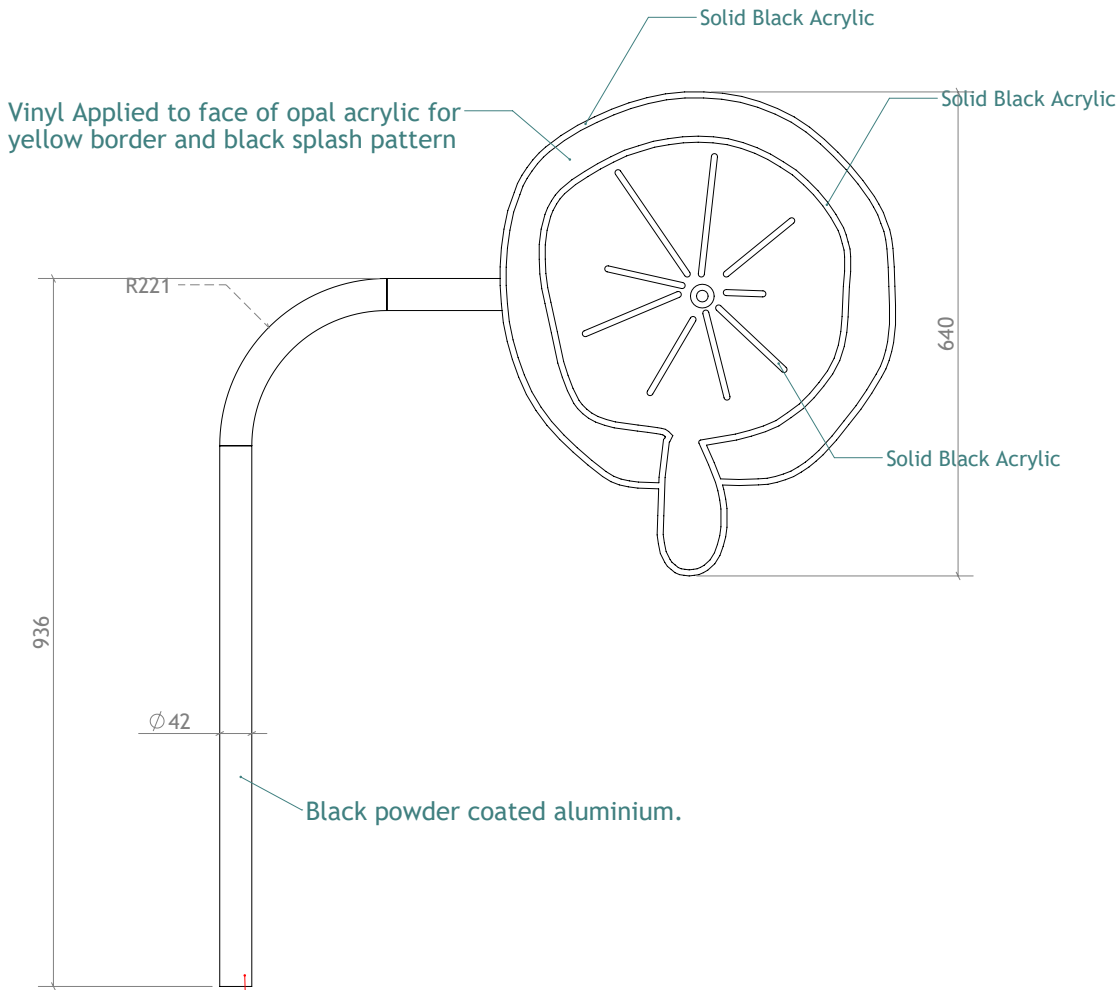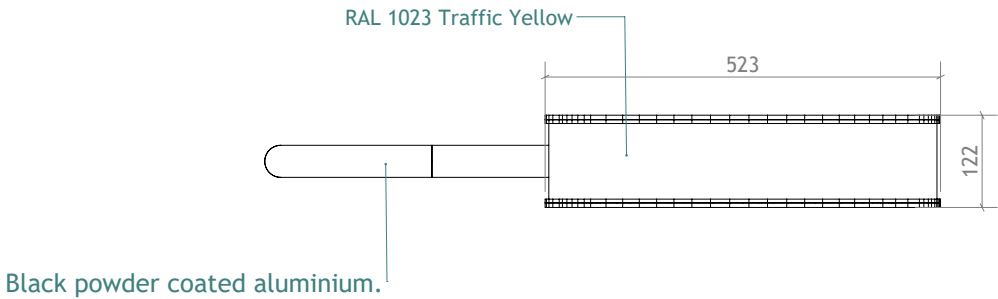

Fixing solution required

Weight of Item :- 4.18KG



Client:
*****CHANGE ME*****

Address:
*****CHANGE ME*****

Project:
*****CHANGE ME*****

Title:
*****CHANGE ME*****

Designer:
Jason Young

Date: 19/12/2025 Scale: 1:10 @ A3
Drawing No:
5271-03-10-SA1
Dwg Sht: 1 of 1 Revision:

Unit 4
Arundel Works
Claywheels Lane
Sheffield
S6 1LZ

eclipsemanufacturingsolutions.co.uk

Date Last Saved:- 19 December 2025 10:32:31

Rev: Description:

A
B
C
D
E
F
G

Weight of Item :- 18.40 kgKG



Client:
VB Interiors Ltd

Address:
Westfield, White City, London

Project:
Lemonica Kiosk

Title:
Lemonade Acrylic Sign

Designer:
Jason Young

Date: 19/12/2025 Scale: 1:20 @ A3


Drawing No:
5271-03-10-SA1-01

Dwg Sht: 1 of 1 Revision:



Unit 4
Arundel Works
Claywheels Lane
Sheffield
S6 1LZ

eclipsemanufacturingsolutions.co.uk



Date Last Saved:- 19 December 2025 11:12:59

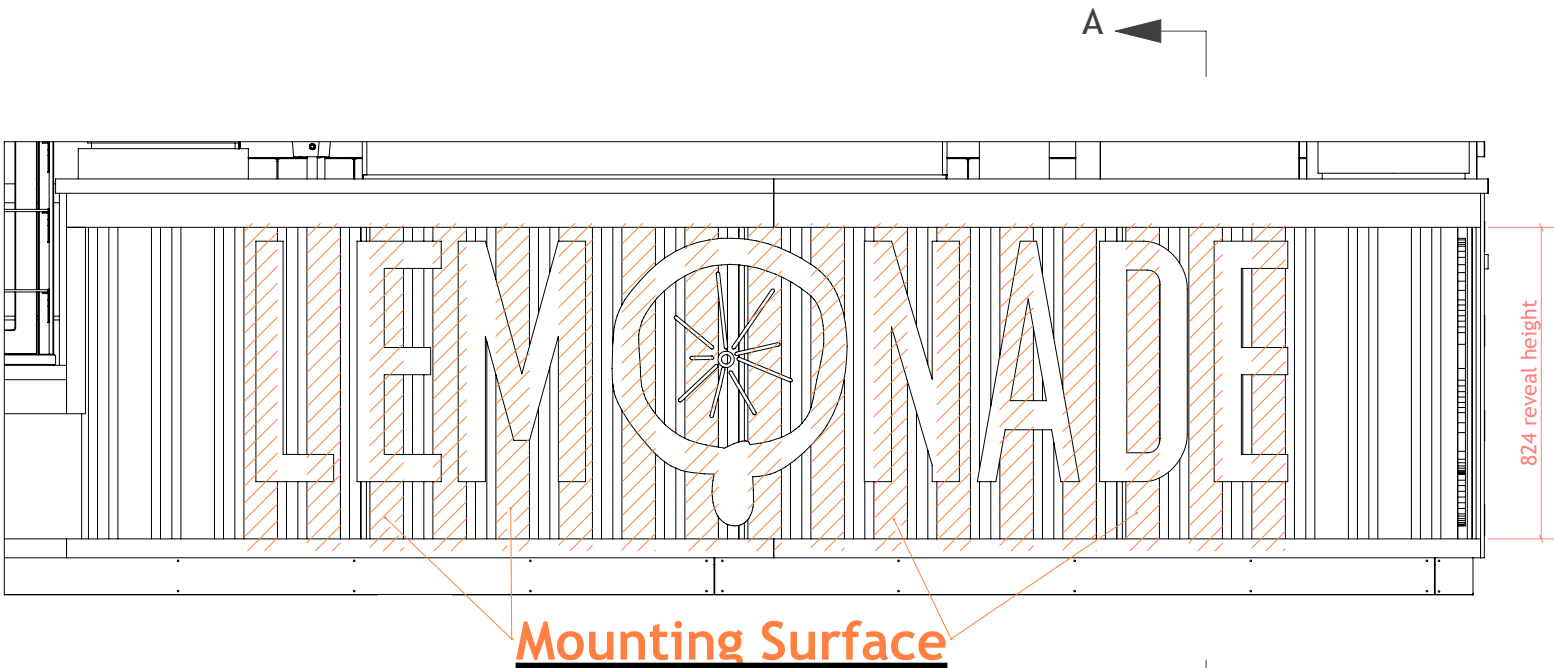

LEM^QNADE

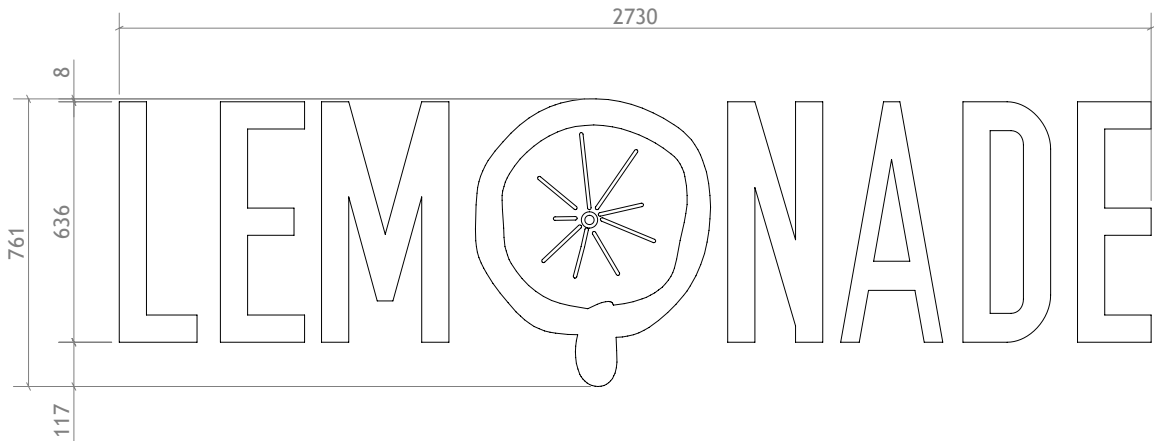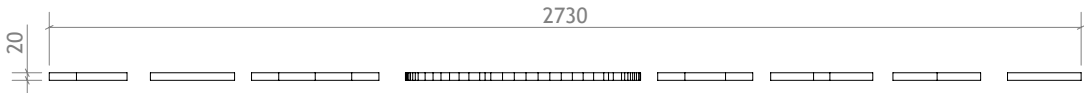

Mounting Surface

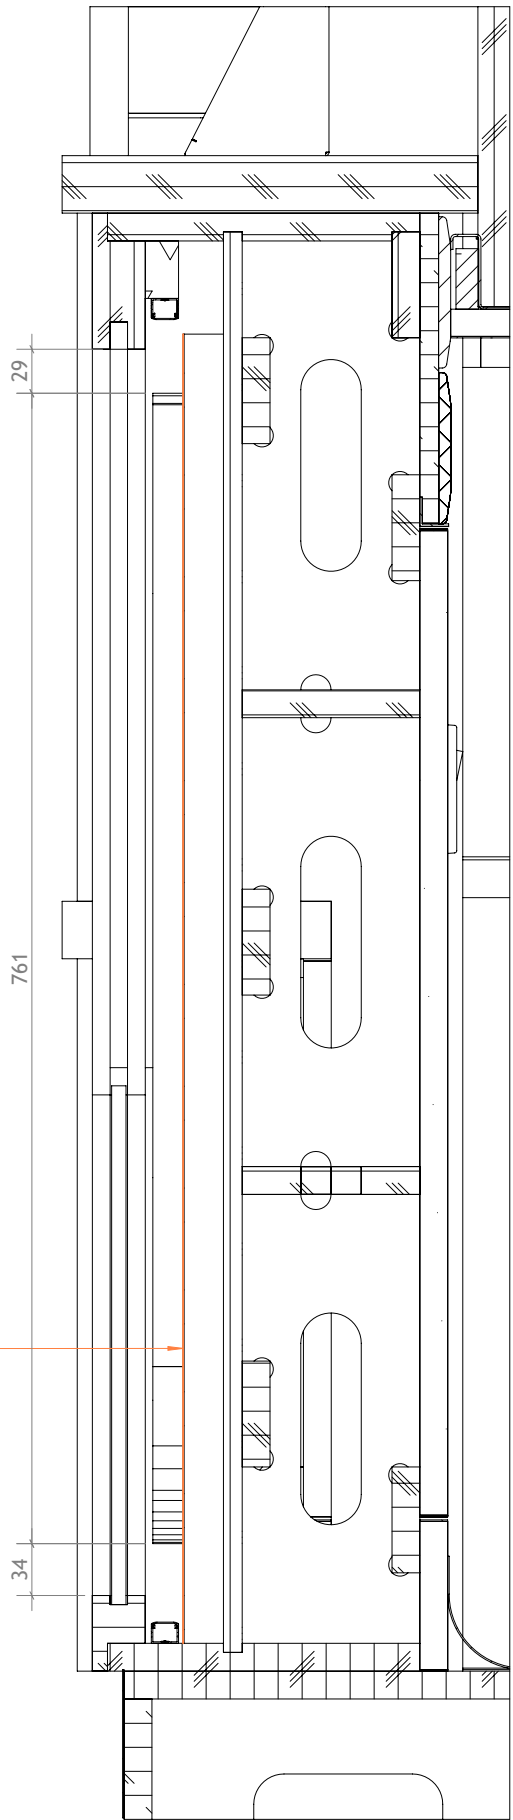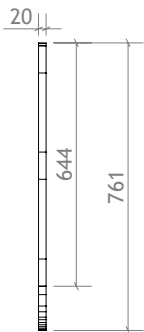

SECTION A-A
SCALE 1 : 5

Rev: Description:

A
B
C
D
E
F
G

Weight of Item :- 3.55 kgKG



Client:
VB Interiors Ltd

Address:
Westfield, White City, London

Project:
Lemonica Kiosk

Title:
Lemonade Acrylic Logo

Designer:
Jason Young

Date: 19/12/2025 Scale: 1:10 @ A3


Drawing No:
5271-03-10-SA1-02

Dwg Sht: 1 of 1 Revision:

Unit 4
Arundel Works
Claywheels Lane
Sheffield
S6 1LZ



eclipsemanufacturingsolutions.co.uk

Date Last Saved:- 19 December 2025 10:55:49


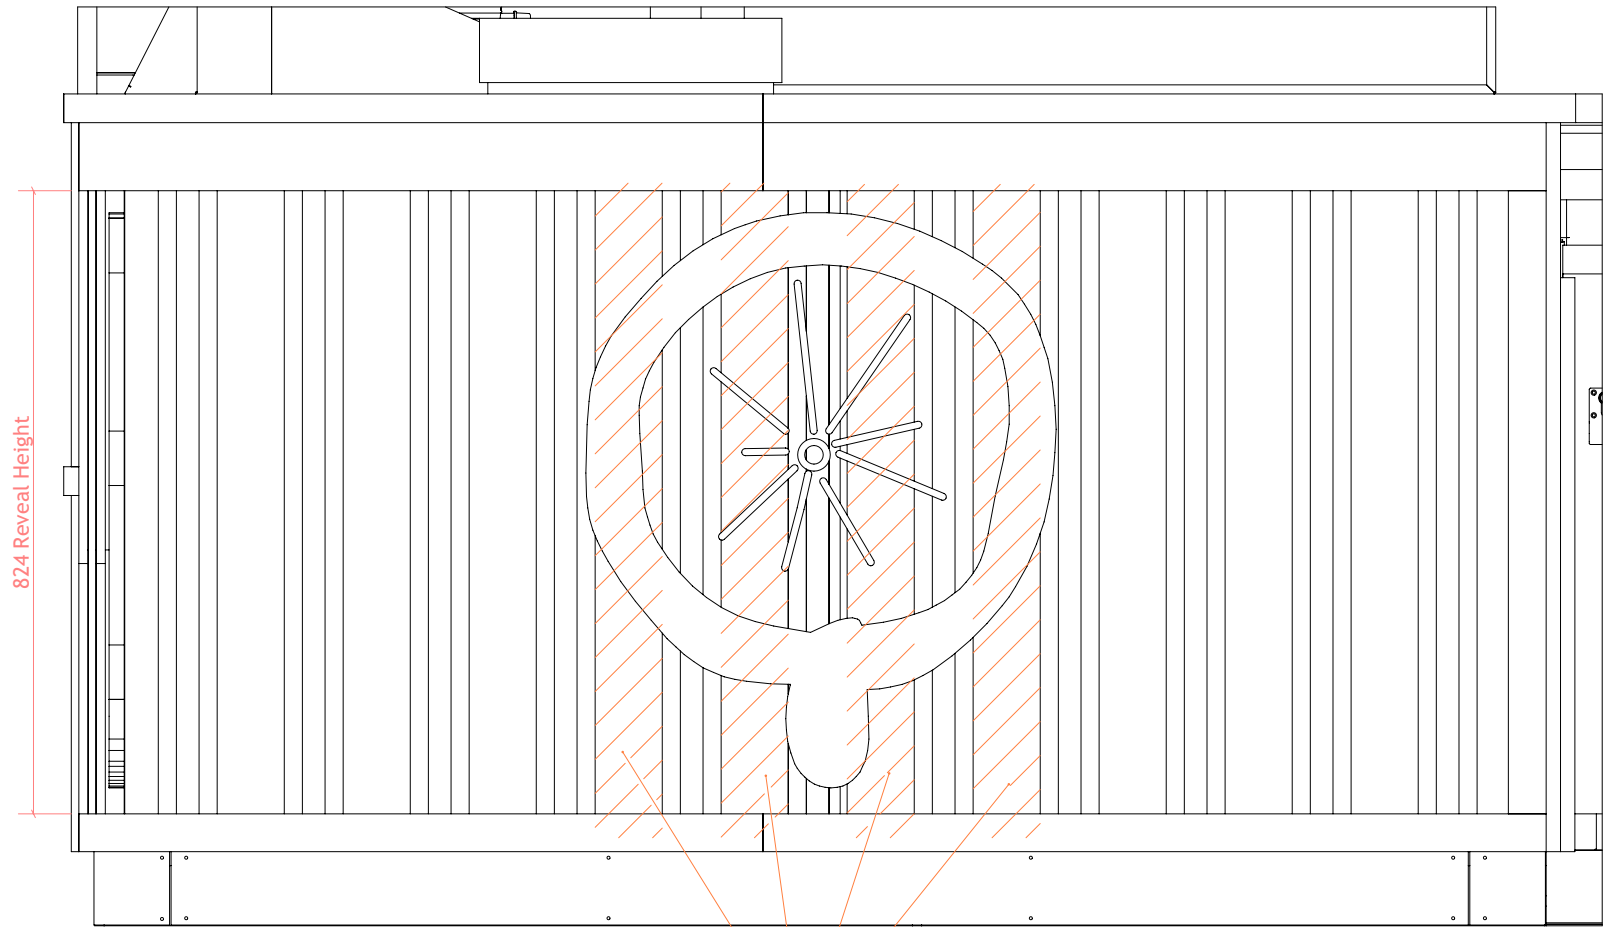


Mounting Surface

A

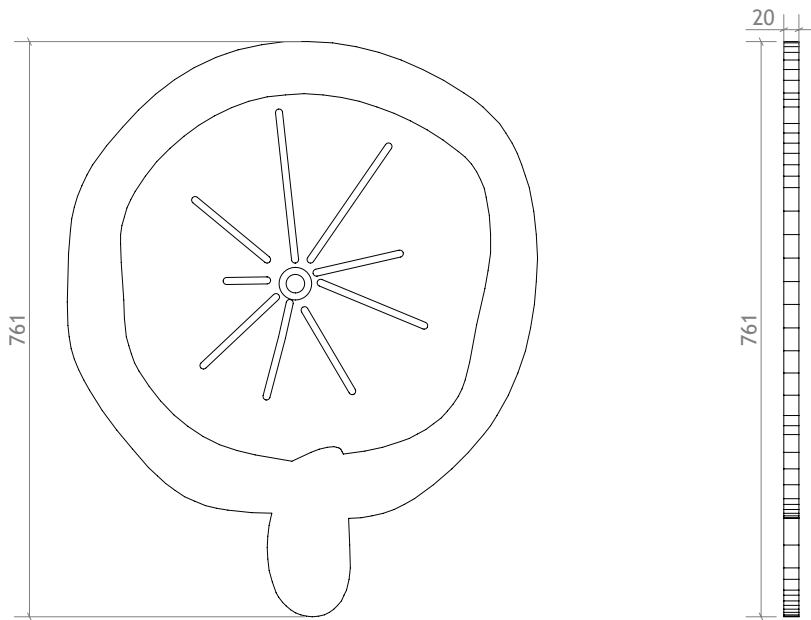
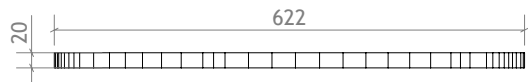


Mounting Surface

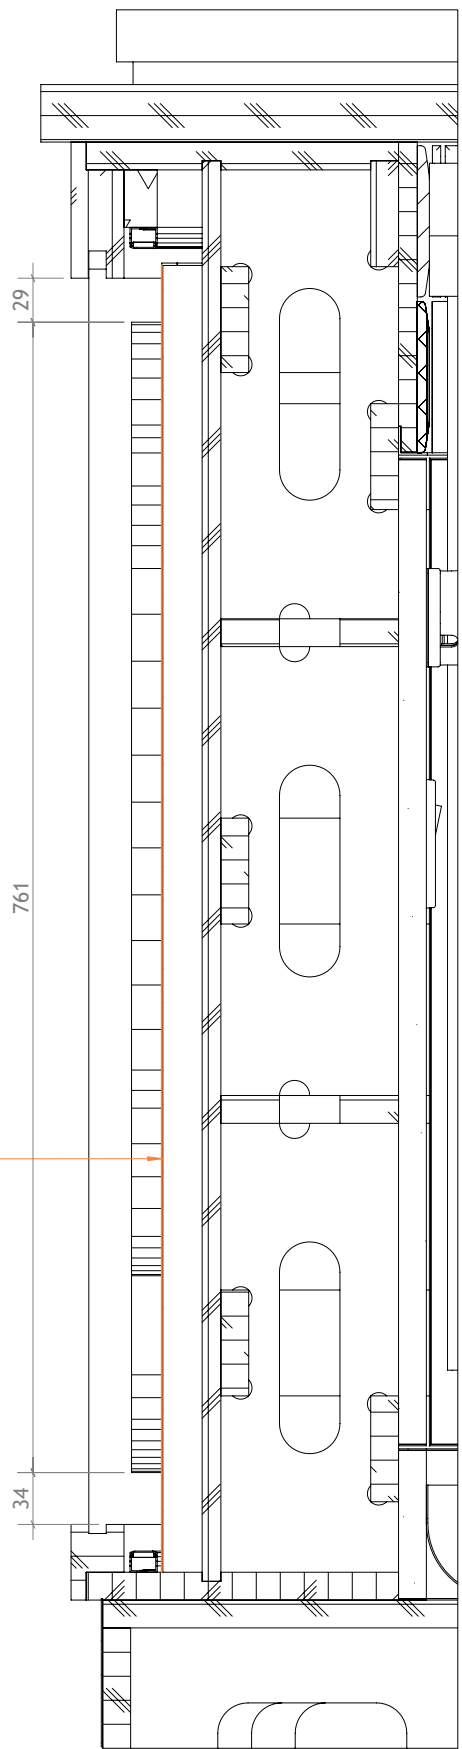
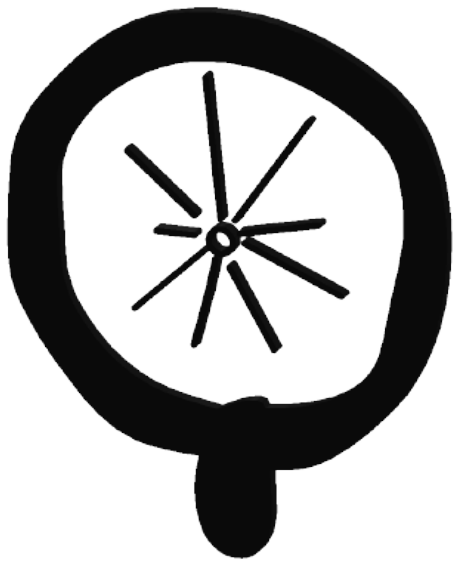


SECTION A-A
SCALE 1 : 5

Rev:	Description:
A	
B	
C	
D	
E	
F	
G	

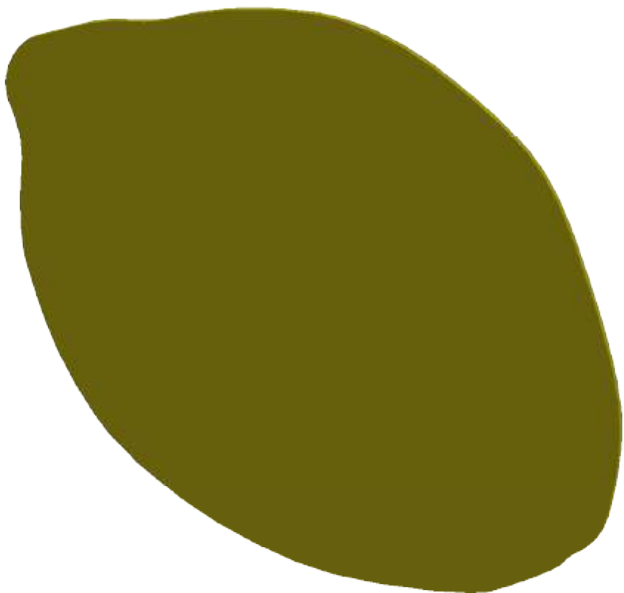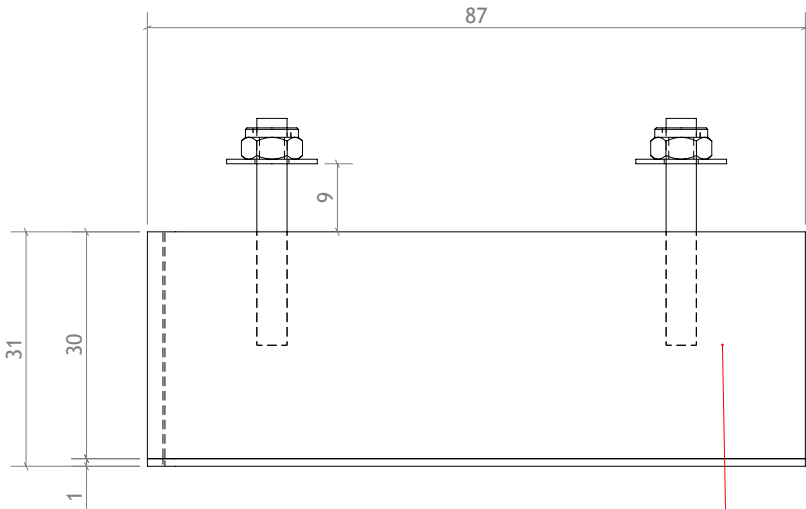

30mm opal acrylic cut out with bevel
- Faced with 1mm SS coated RAL 1023

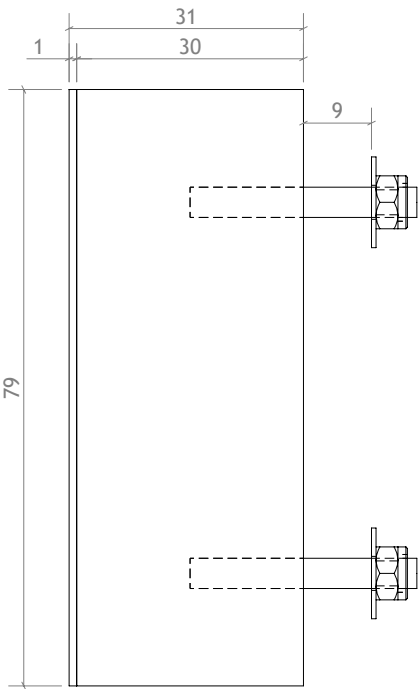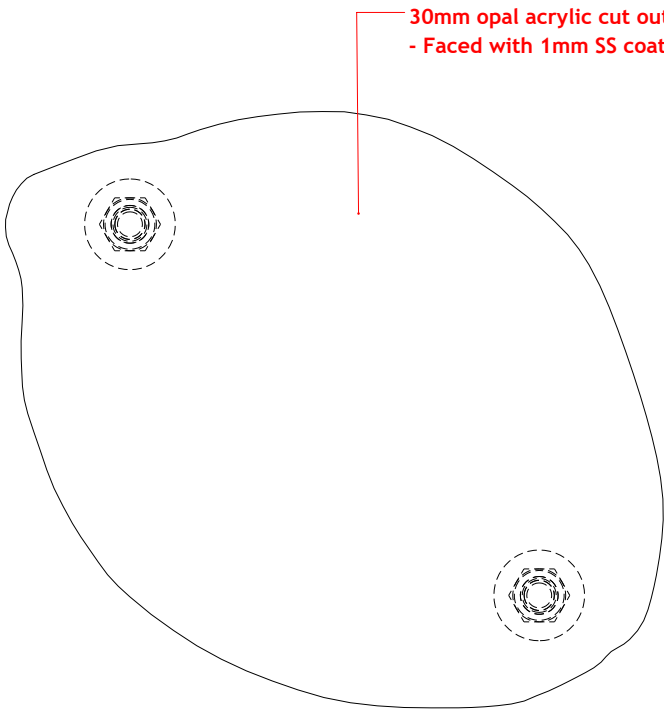

Weight of Item :- 1.27 kgKG



Client:
VB Interiors Ltd

Address:
Westfield, White City, London

Project:
Lemonica Kiosk

Title:
Illuminated Acrylic Lemon

Designer:
Jason Young

Date: 19/12/2025 Scale: 1:1 @ A3
Drawing No: 5271-03-10-SA2-01
Dwg Sht: 1 of 1 Revision:

Unit 4
Arundel Works
Claywheels Lane
Sheffield
S6 1LZ

eclipsemanufacturingsolutions.co.uk

Date Last Saved:- 17 December 2025 13:51:42

Rev: Description:

A
B
C
D
E
F
G

Weight of Item :- 4.12 kgKG



Client:
VB Interiors Ltd

Address:
Westfield, White City, London

Project:
Lemonica Kiosk

Title:
Totem Illuminated Signage

Designer:
Jason Young

Date: 19/12/2025 Scale: 1:5 @ A3


Drawing No:
5271-03-10-SA4-
SA1-01
Dwg Sh: 1 of 1

Revision:


Unit 4
Arundel Works
Claywheels Lane
Sheffield
S6 1LZ

eclipsemanufacturingsolutions.co.uk

Date Last Saved:- 19 December 2025 10:27:06

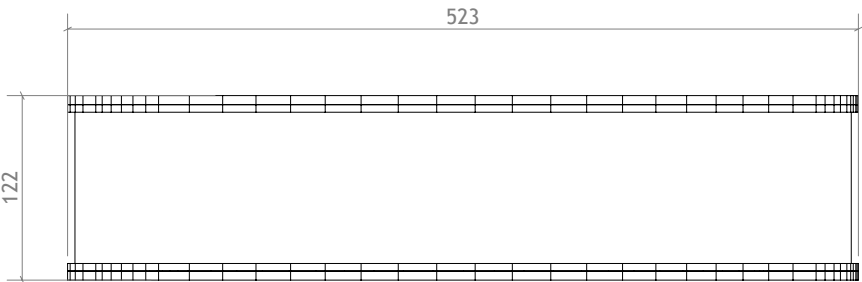

Vinyl Applied to face of opal acrylic for yellow border and black splash pattern


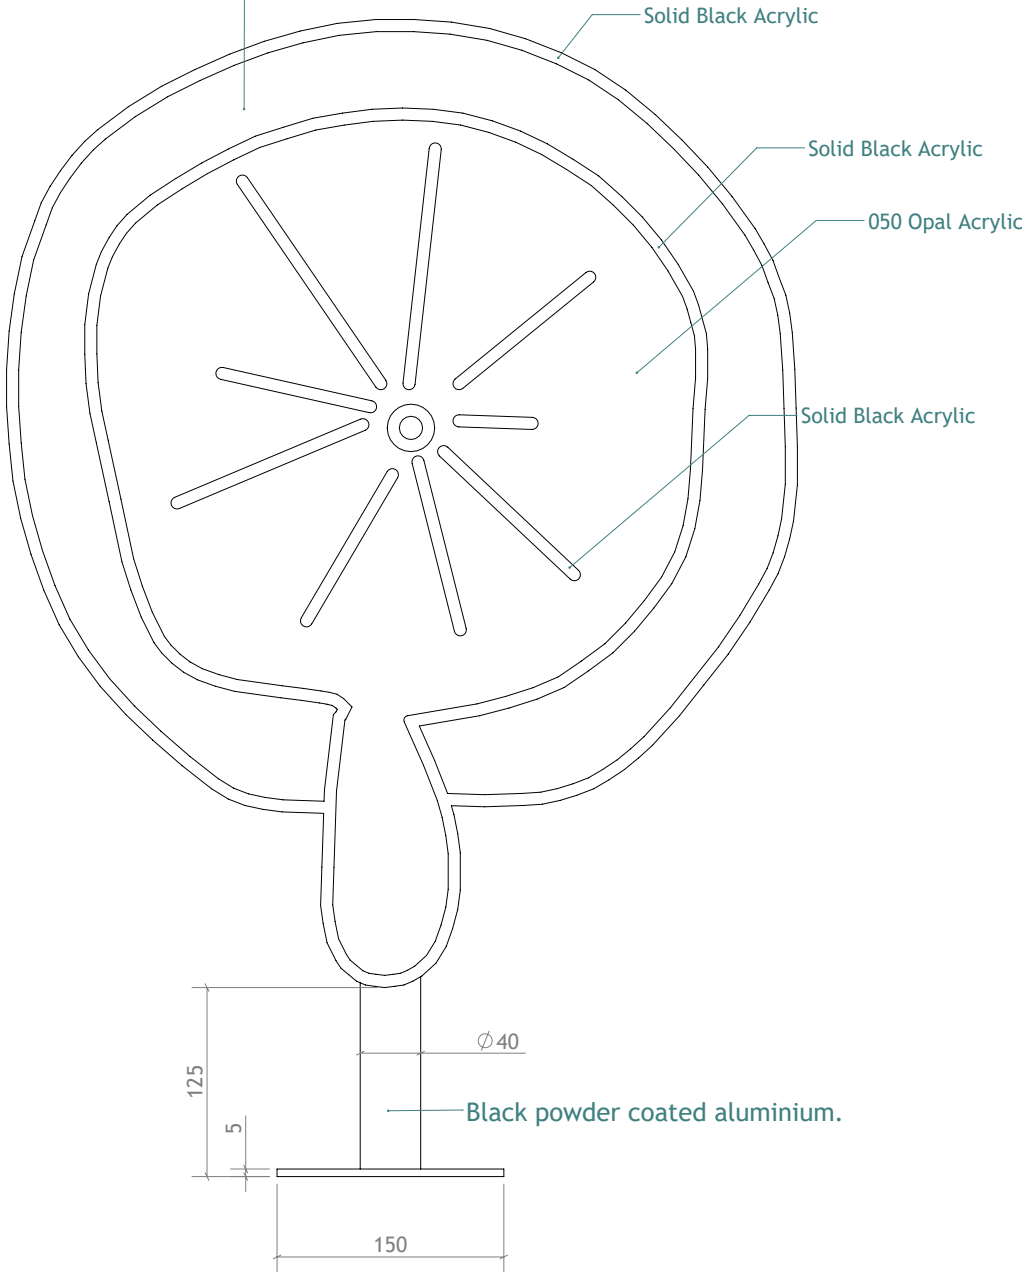


Vinyl Applied to face of opal acrylic for yellow border and black splash pattern




Solid Black Acrylic

Solid Black Acrylic

Material <not specified>

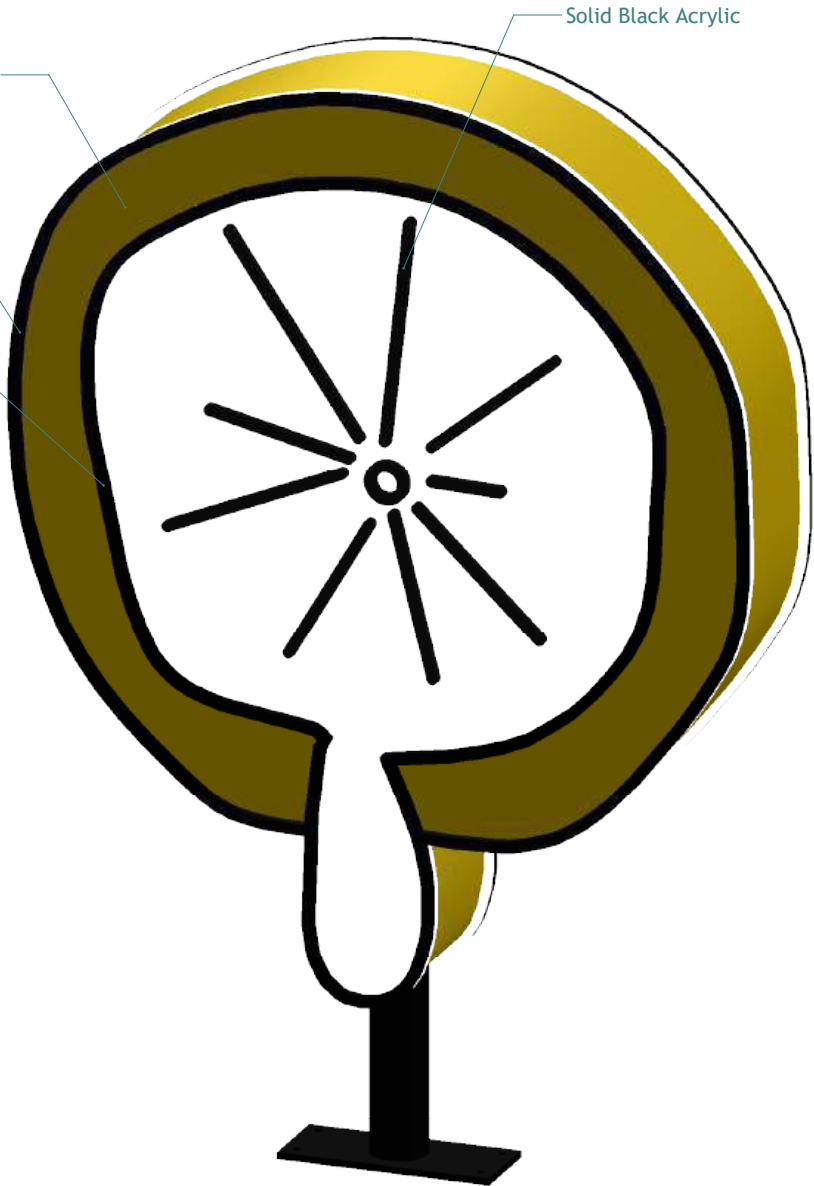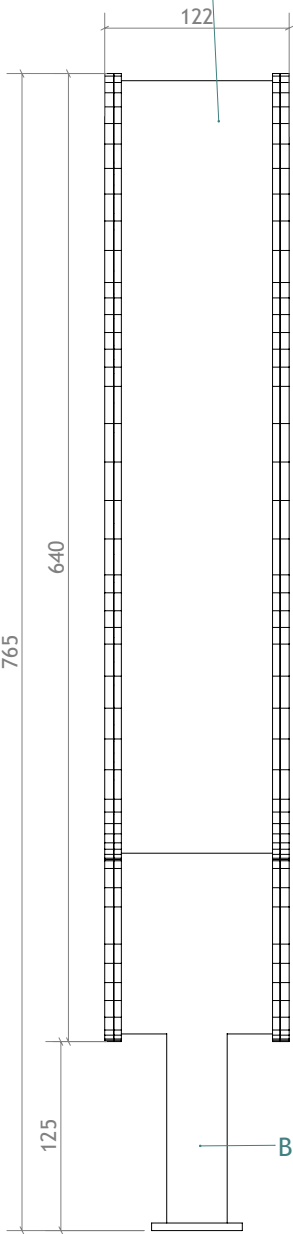

Rev:	Description:
A	
B	
C	
D	
E	
F	
G	

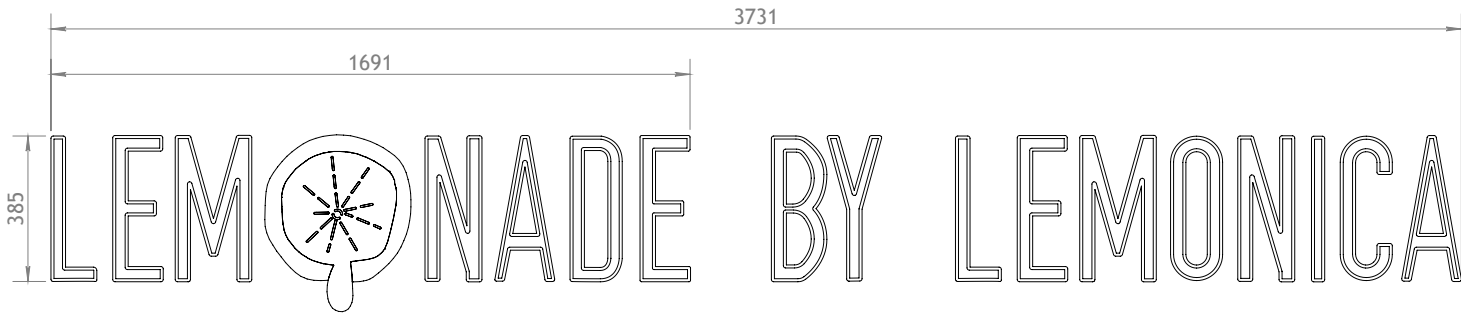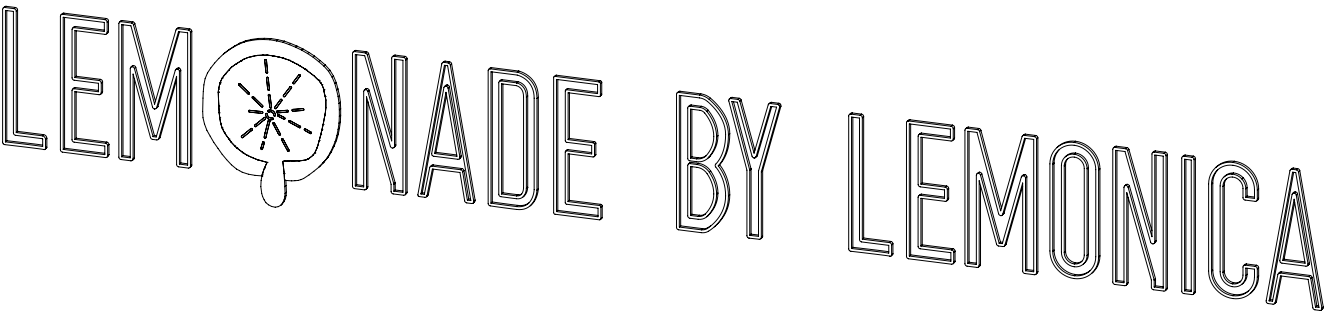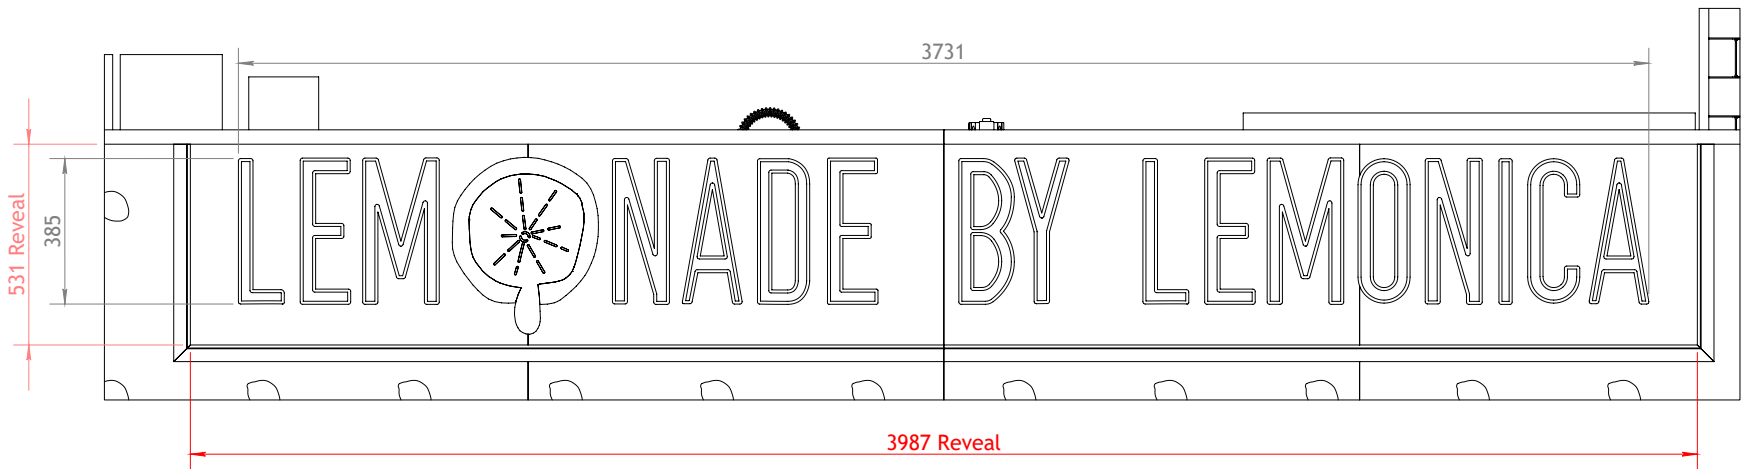

Weight of Item :- 3.32 kgKG



Client:
VB Interiors Ltd

Address:
Westfield, White City, London

Project:
Lemonica Kiosk

Title:
Neon Signage

Designer:
Jason Young

Date: 05/01/2026 Scale: 1:20 @ A3
Drawing No: 5271-03-10-SA5-
SA1-01
Dwg No: 1 of 1 Revision:

Unit 4
Arundel Works
Claywheels Lane
Sheffield
S6 1LZ

eclipsemanufacturingsolutions.co.uk

Date Last Saved:- 19 December 2025 10:21:13

Rev: Description:

A
B
C
D
E
F
G

Weight of Item :- 2.71 kgKG



Client:
VB Interiors Ltd

Address:
Westfield, White City, London

Project:
Lemonica Kiosk

Title:
Stacked Neon Signage

Designer:
Jason Young

Date: 19/12/2025 Scale: 1:10 @ A3

Drawing No:
5271-03-10-SA5-
SA1-02


DWG SHEET 1 of 1

Revision:



Unit 4
Arundel Works
Claywheels Lane
Sheffield
S6 1LZ

eclipsemanufacturingsolutions.co.uk

Date Last Saved:- 19 December 2025 10:07:38

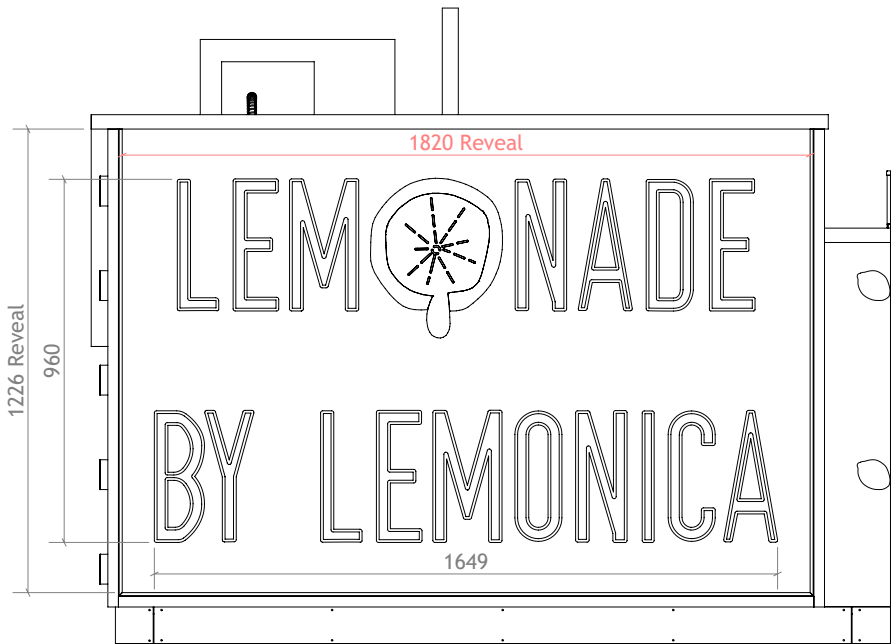

SCALE 1 : 20

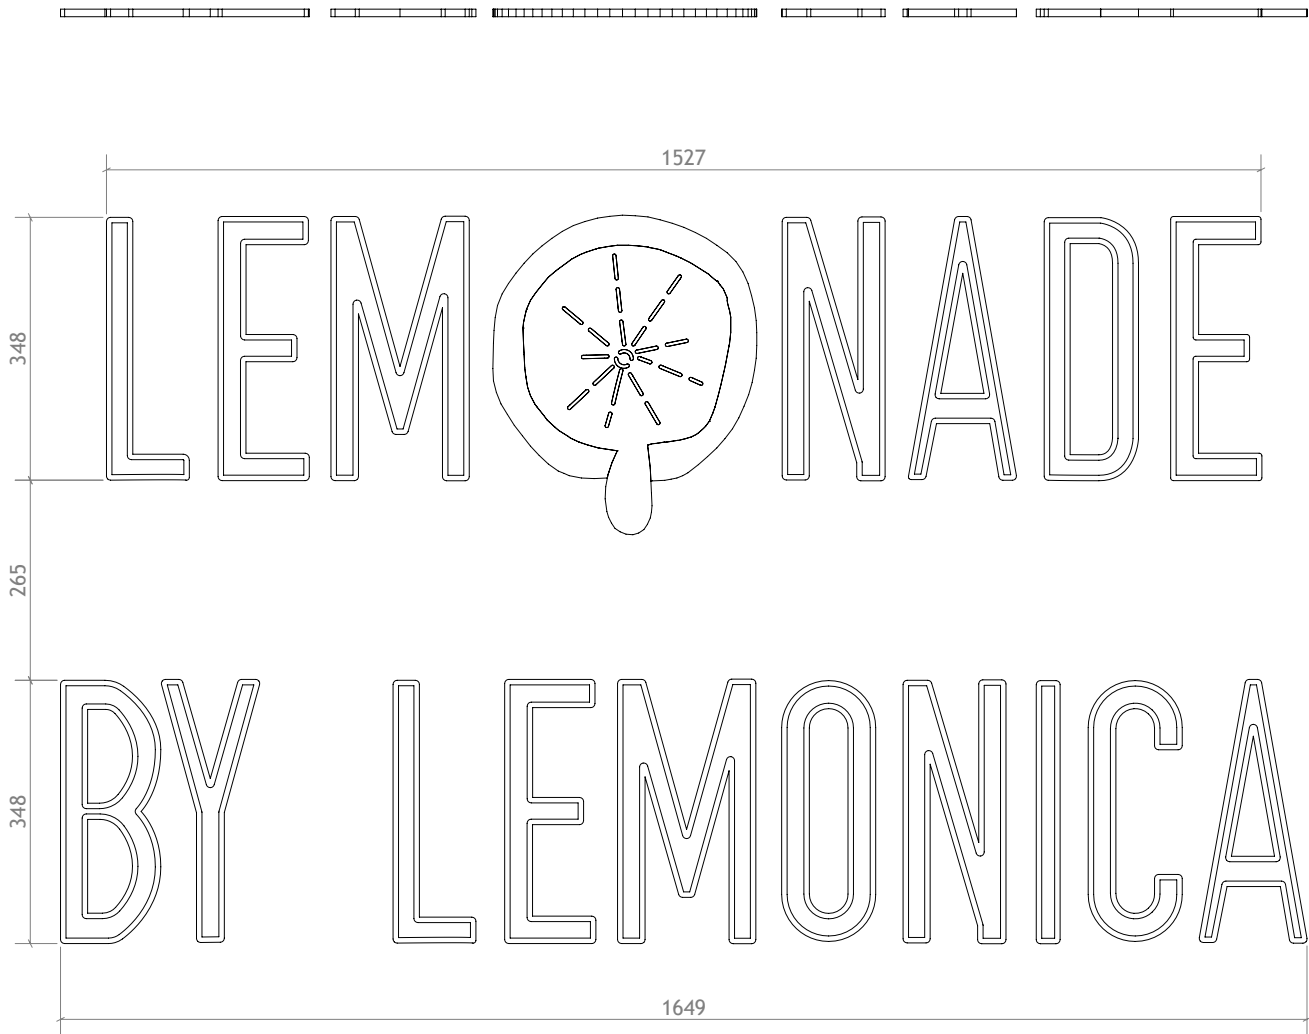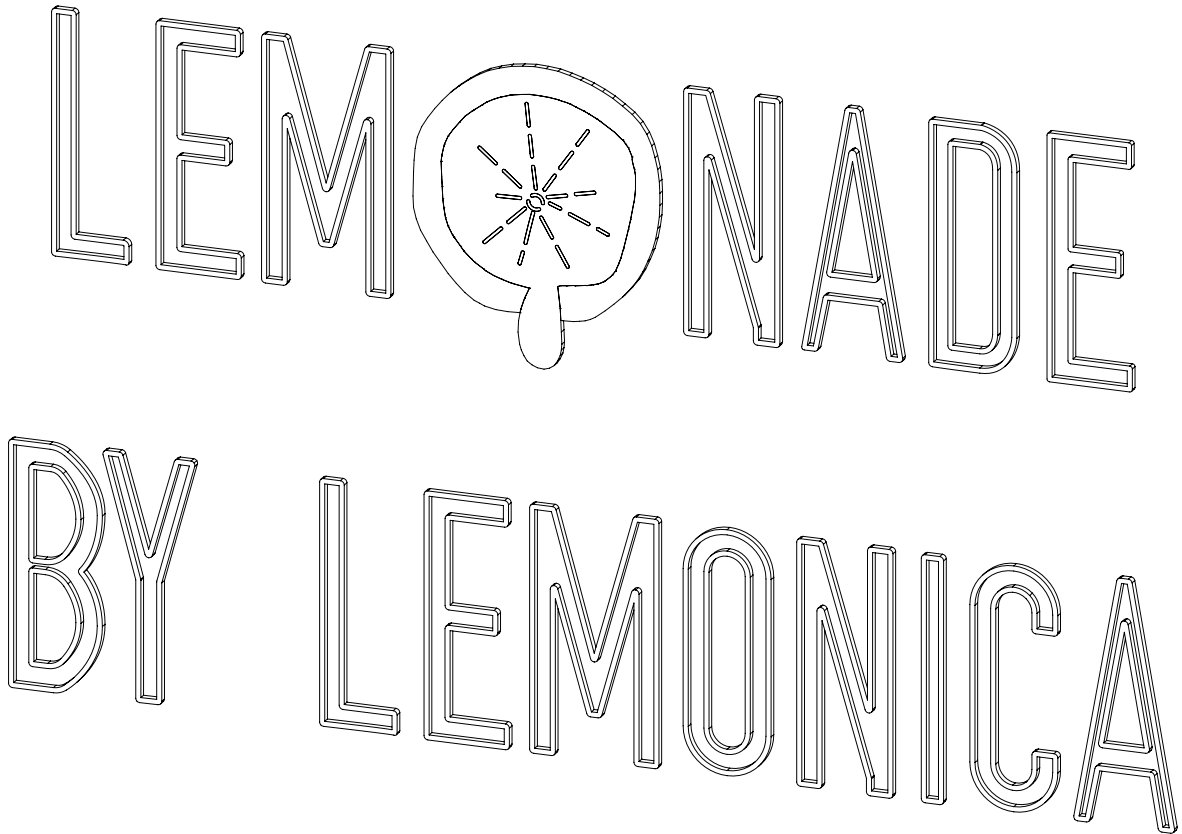


ITEM NO.	PART NUMBER	Item	Weight(Kg)	QTY.
1	5271-03-12-SA2	Stainless Steel Worktop	22.06	1
2	5271-03-12-GA-01	Backing Board for sink	18.75	1
3	5271-03-12-GA-02	Balancer	2.04	1
4	5271-03-12-GA-03	Fixing Batten	0.57	1
5	5271-03-12-SA5	Wide Base Unit	96.62	1




This drawing is the property of Eclipse Manufacturing Solutions: and is protected by the Design Copyright Act 1968. This drawing must not be copied or otherwise reproduced without the express written consent of Eclipse Manufacturing Solutions:

Do not scale from this drawing. All dimensions are to be confirmed on site and subject to building control and statutory approvals.

Rev:	Description:	Drawn:
A	30/01/04 Grease Trap Added	JY
B		
C		
D		
E		
F		
G		

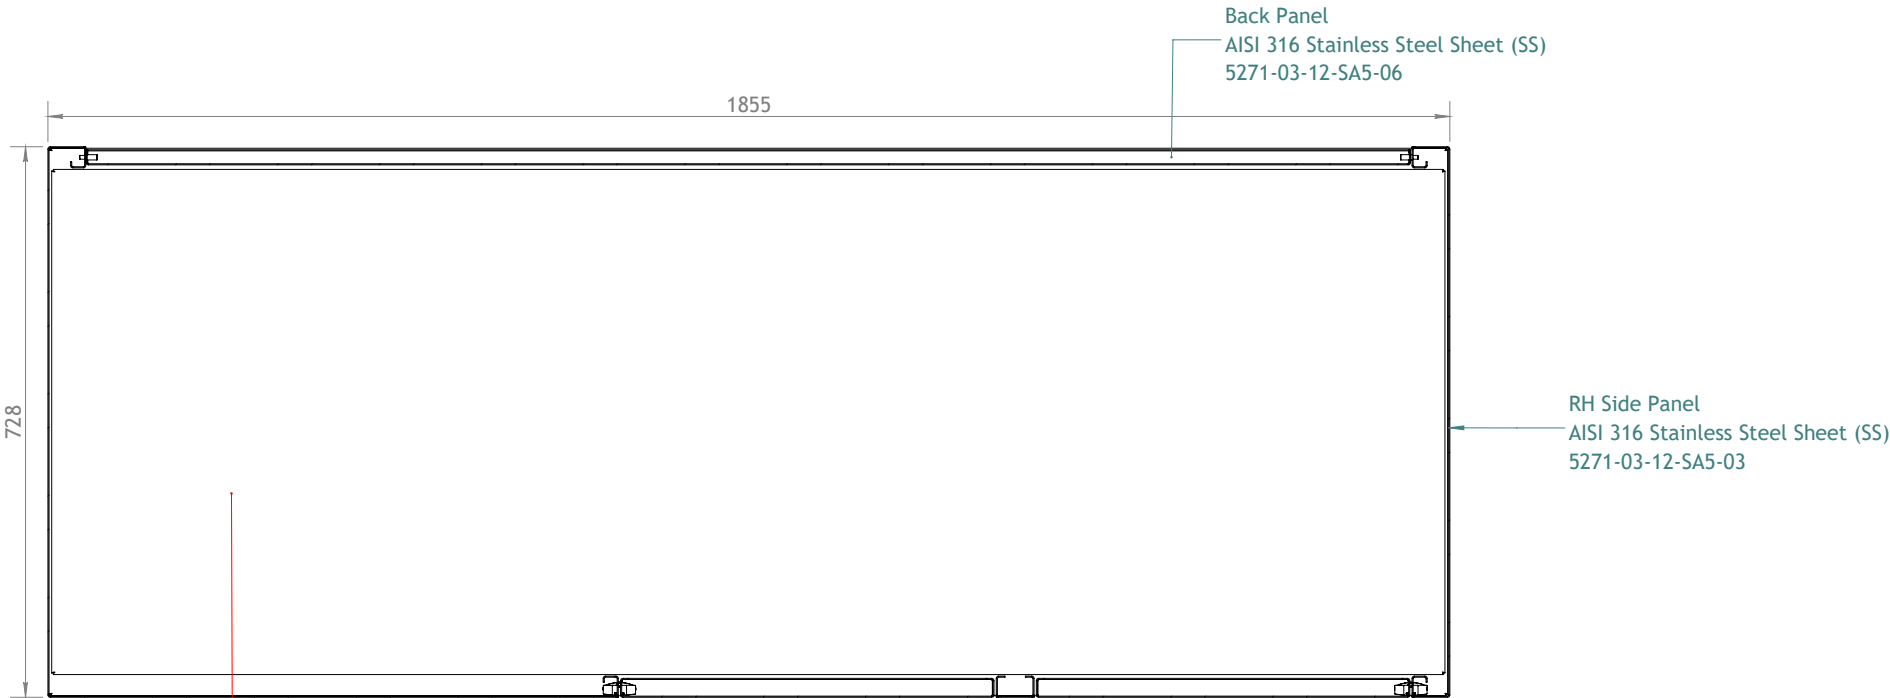

storage space

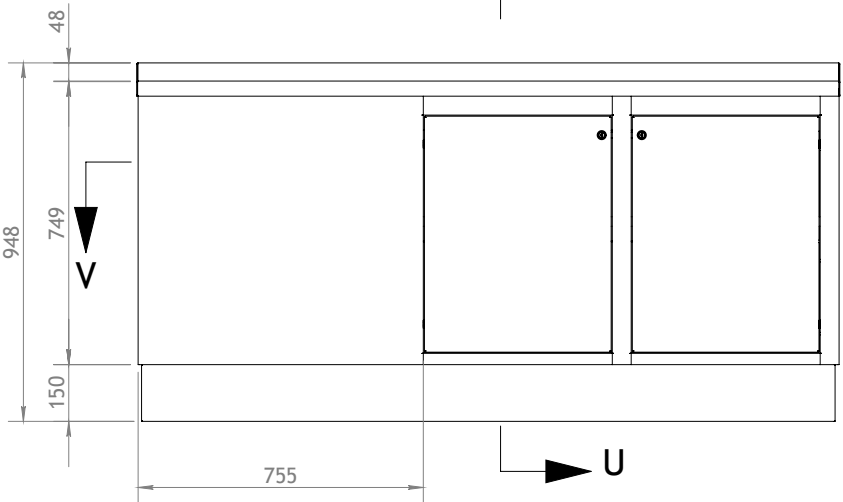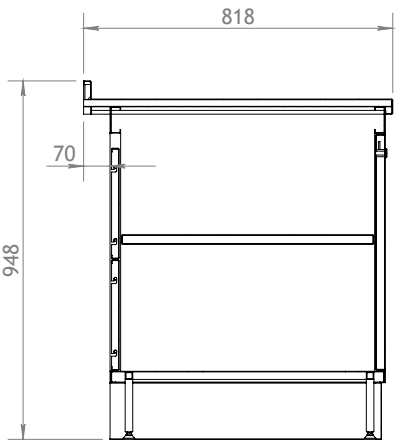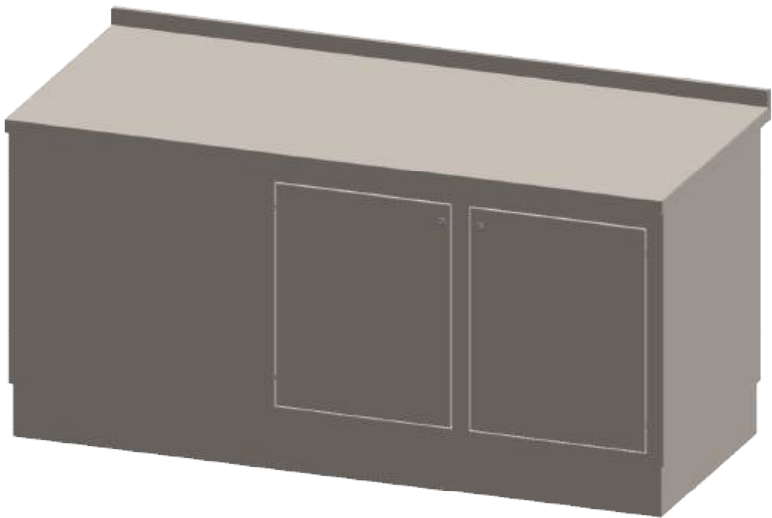

Weight of Item :- 140.03KG



Client:
Optimusblu

Address:
Westfield London

Project:
Smatcha Kiosk

Title:
Stainless Steel Unitry

Designer:
Jason Young

Date: 18/12/2025 Scale: 1:20 @ A3

Drawing No: 5271-03-12-GA

Dwg Sht: 1 of 1 Revision: A

Unit 4
Arundel Works
Claywheels Lane
Sheffield
S6 1LZ

eclipsemanufacturingsolutions.co.uk

Date Last Saved:- 08 December 2025 13:42:20

Rev:	Description:
A	05/01/26 With tight sheet.
B	
C	
D	
E	
F	
G	

Weight of Item :- 4.99KG



Client:
VB Interiors Ltd

Address:
Westfield, White City, London

Project:
Lemonica Kiosk

Title:
Shot Display

Designer:
Jason Young

Date: 05/01/2026 Scale: 1:5 @ A3

Drawing No:
5271-03-13-SA1


Dwg Sht: 1 of 1

Revision: A

Unit 4
Arundel Works
Claywheels Lane
Sheffield
S6 1LZ

eclipsemanufacturingsolutions.co.uk

Date Last Saved:- 18 December 2025 08:47:58

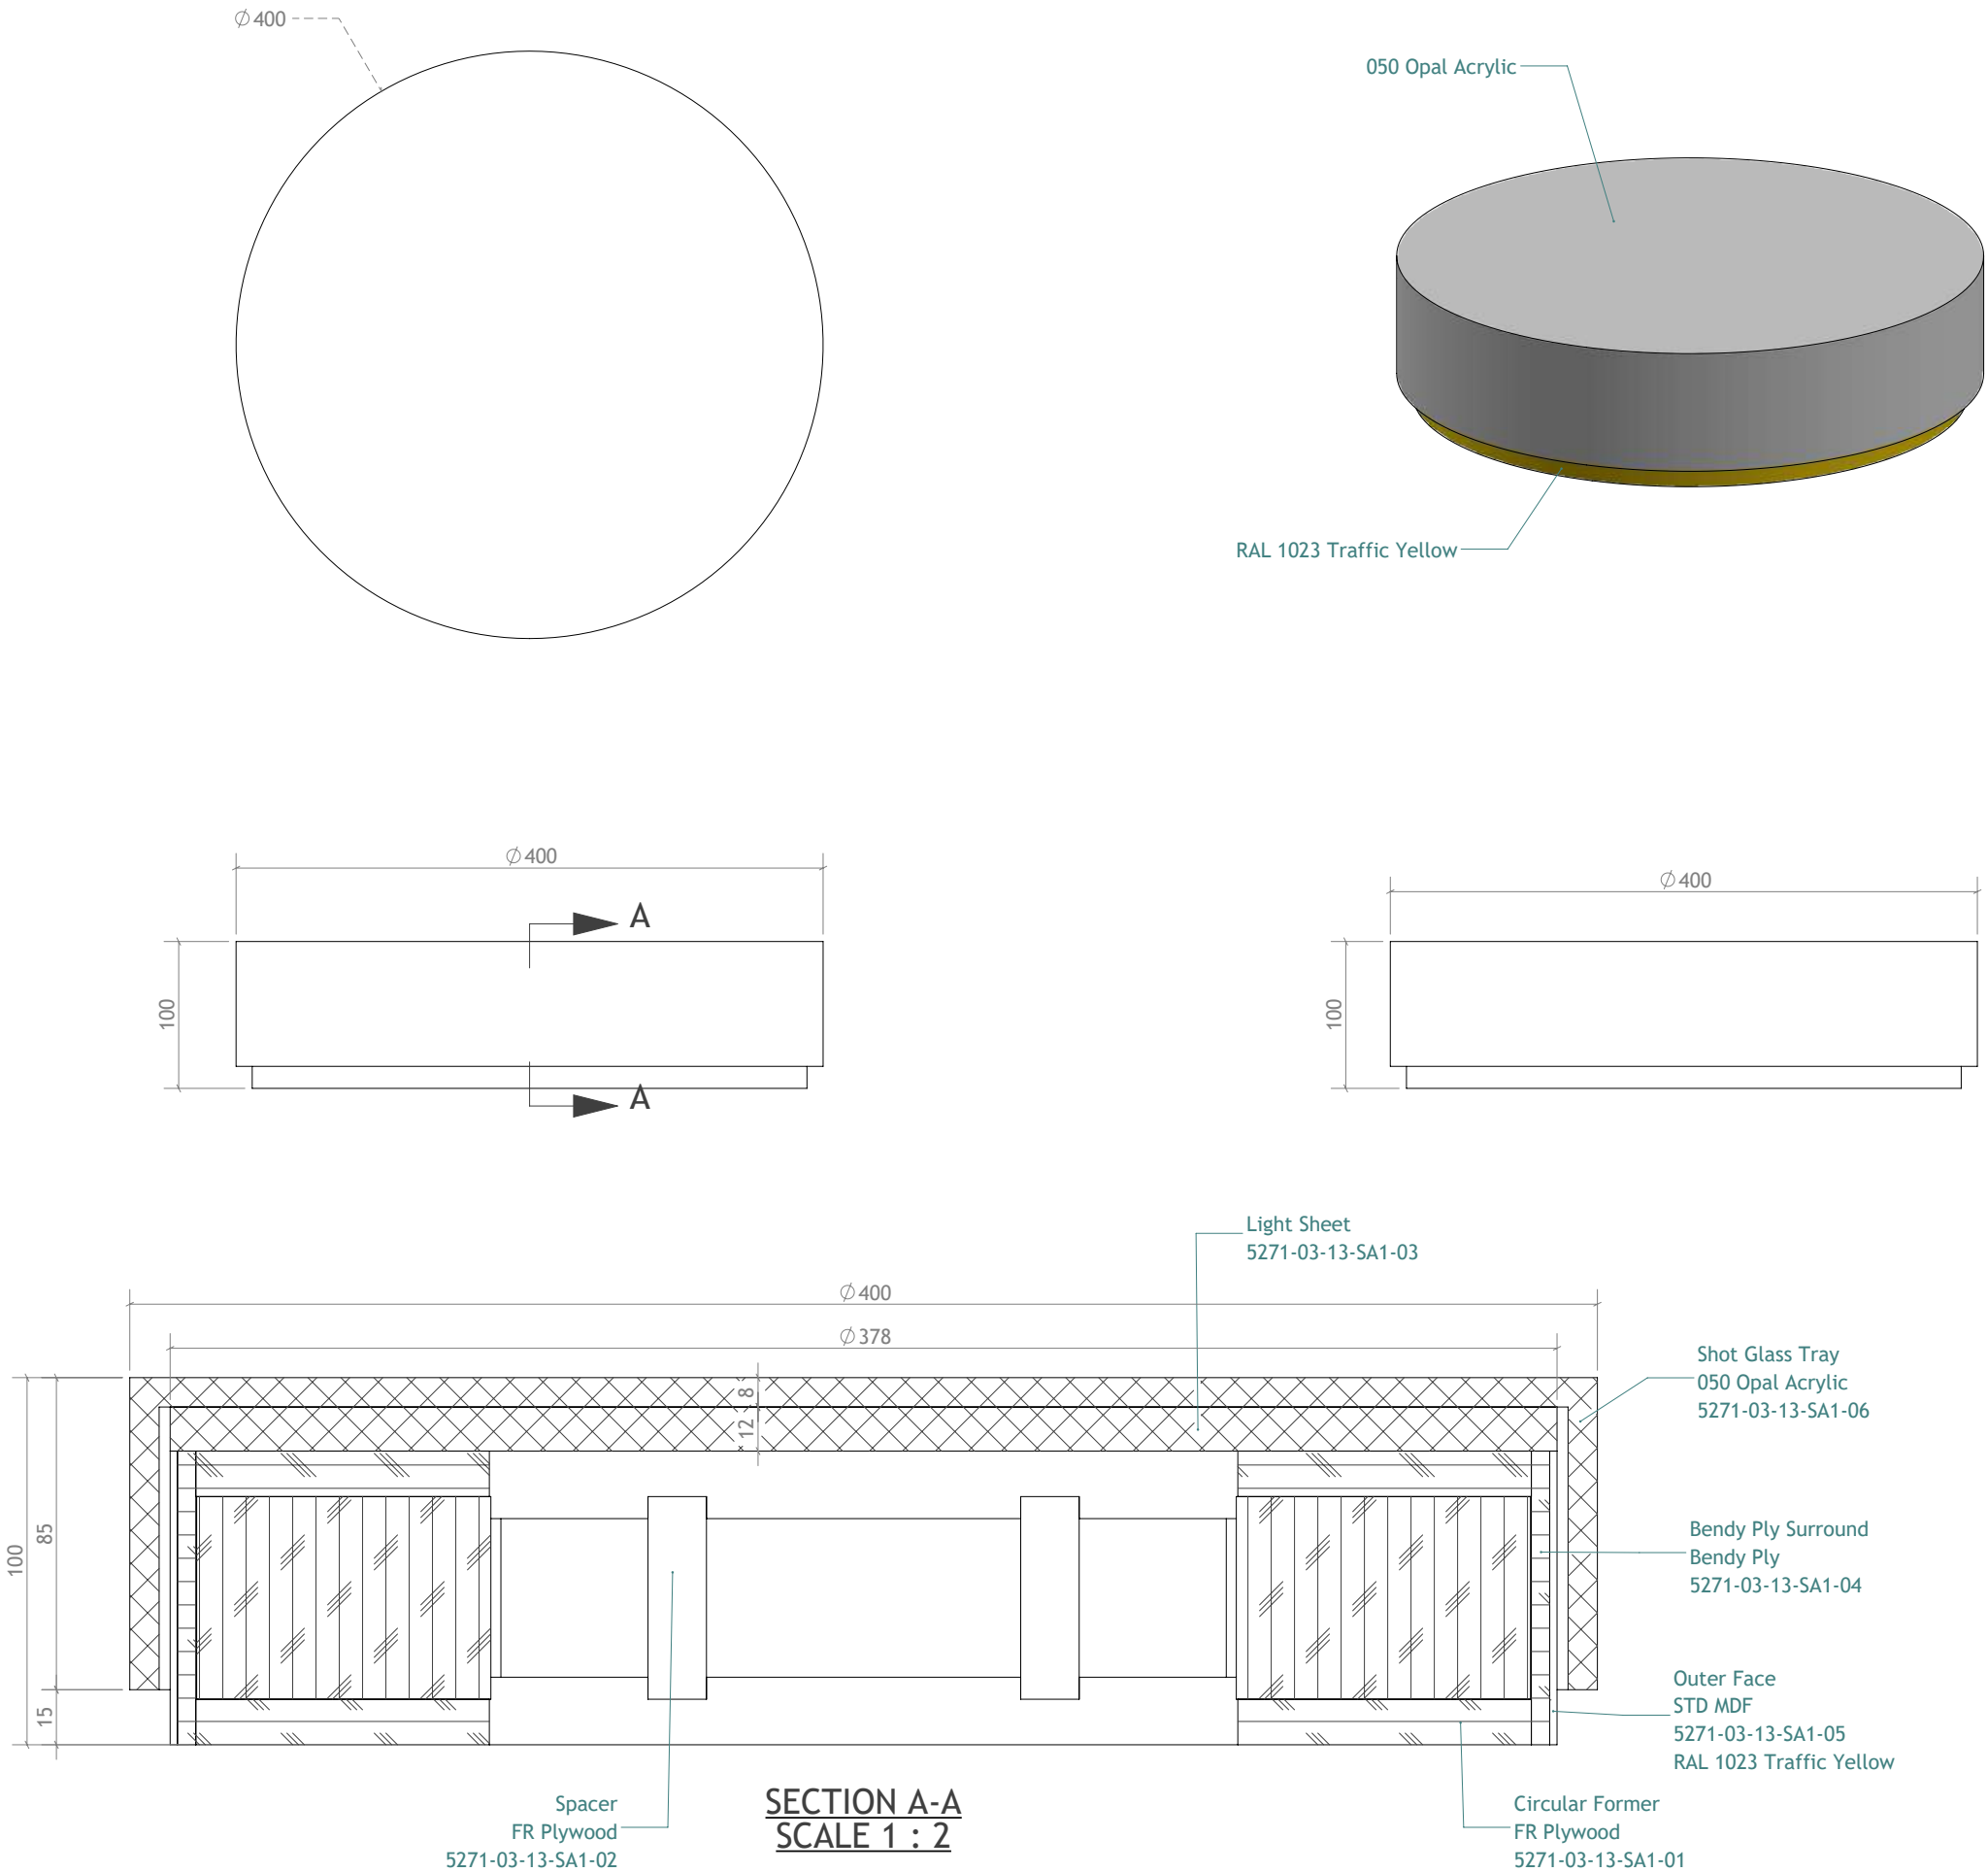

Rev:	Description:	Drawn:
A		JY
B		
C		
D		
E		
F		
G		


Weight of Item :- 380.61KG



Client:
VB Interiors Ltd
Address:
Westfield, White City, London
Project:
Lemonica Kiosk
Title:
Lemonica Hording
Designer:
Jason Young

Date: 10/02/2026 Scale: 1:50 @ A3
Drawing No:
5271-03-14-GA
Dwg Sht: 1 of 2 Revision:


Unit 4
Arundel Works
Claywheels Lane
Sheffield
S6 1LZ
eclipsemanufacturingsolutions.co.uk
Date Last Saved:- 10 February 2026 15:29:47

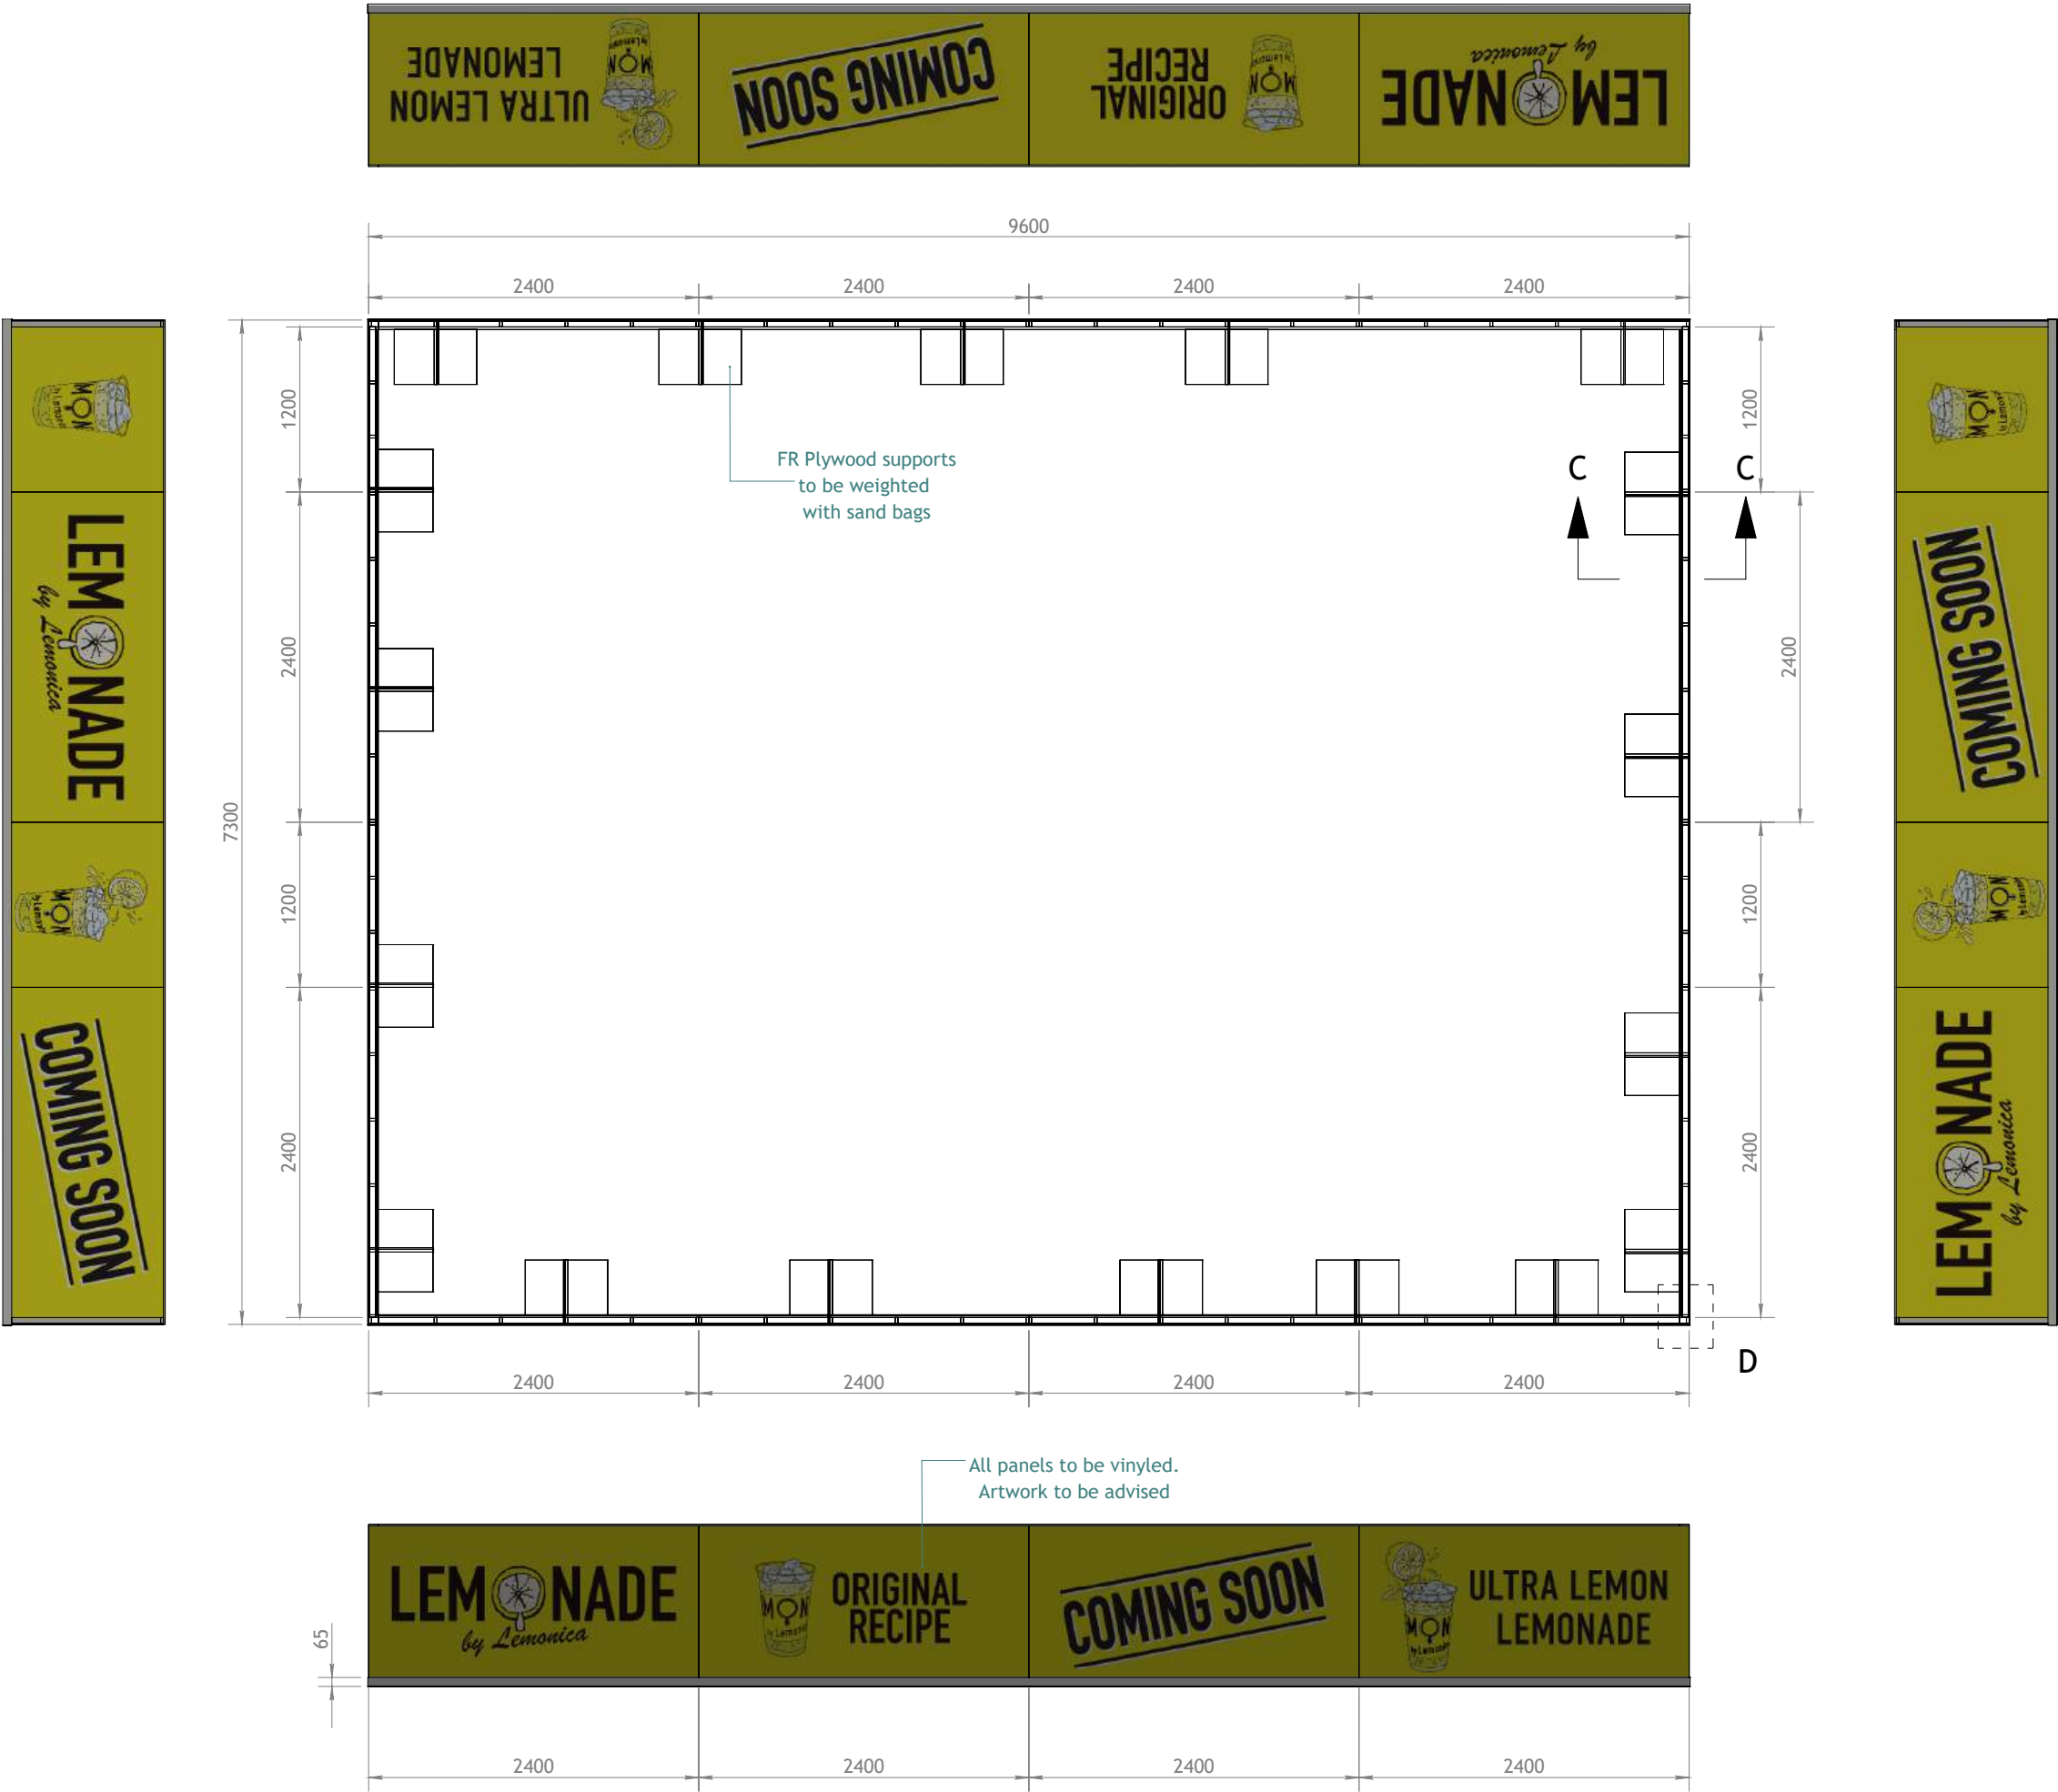


This drawing is the property of Eclipse Manufacturing Solutions: and is protected by the Design Copyright Act 1988. This drawing must not be copied or otherwise reproduced without the express written consent of Eclipse Manufacturing Solutions:

Do not scale from this drawing. All dimensions are to be confirmed on site and subject to building control and statutory approvals.

Rev:	Description:	Drawn:
A		JY
B		
C		
D		
E		
F		
G		

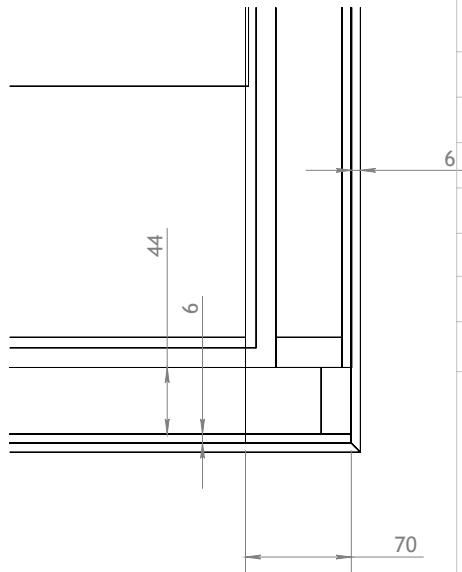

DETAIL D
SCALE 1 : 5

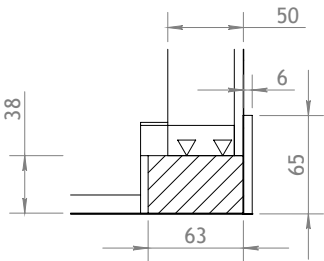

DETAIL Y
SCALE 1 : 5

Weight of Item :- 380.61KG



Client:
VB Interiors Ltd

Address:
Westfield, White City, London

Project:
Lemonica Kiosk

Title:
Lemonica Hording - Hoarding Graphics

Designer:
Jason Young


Date: 10/02/2026 Scale: 1:50 @ A3
Drawing No:5271-03-14-GA - Images

Dwg Sht: 2 of 2 Revision:

Unit 4
Arundel Works
Claywheels Lane
Sheffield
S6 1LZ

eclipsemanufacturingsolutions.co.uk

Date Last Saved:- 10 February 2026 15:29:47

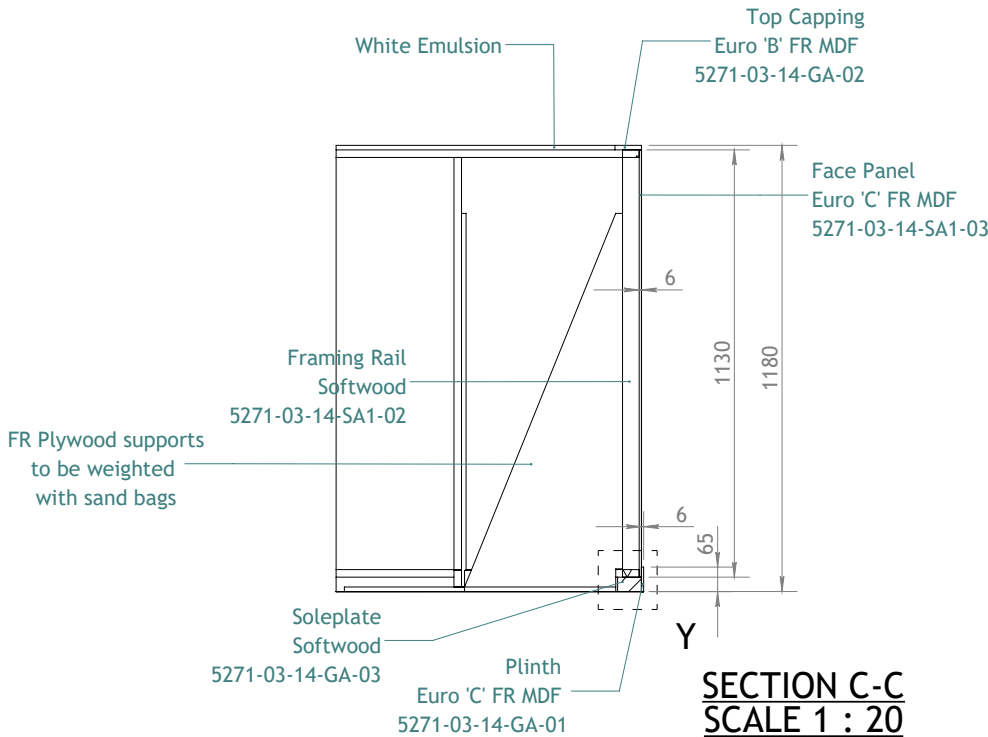



The **GUILD**
of MASTER CRAFTSMEN

